




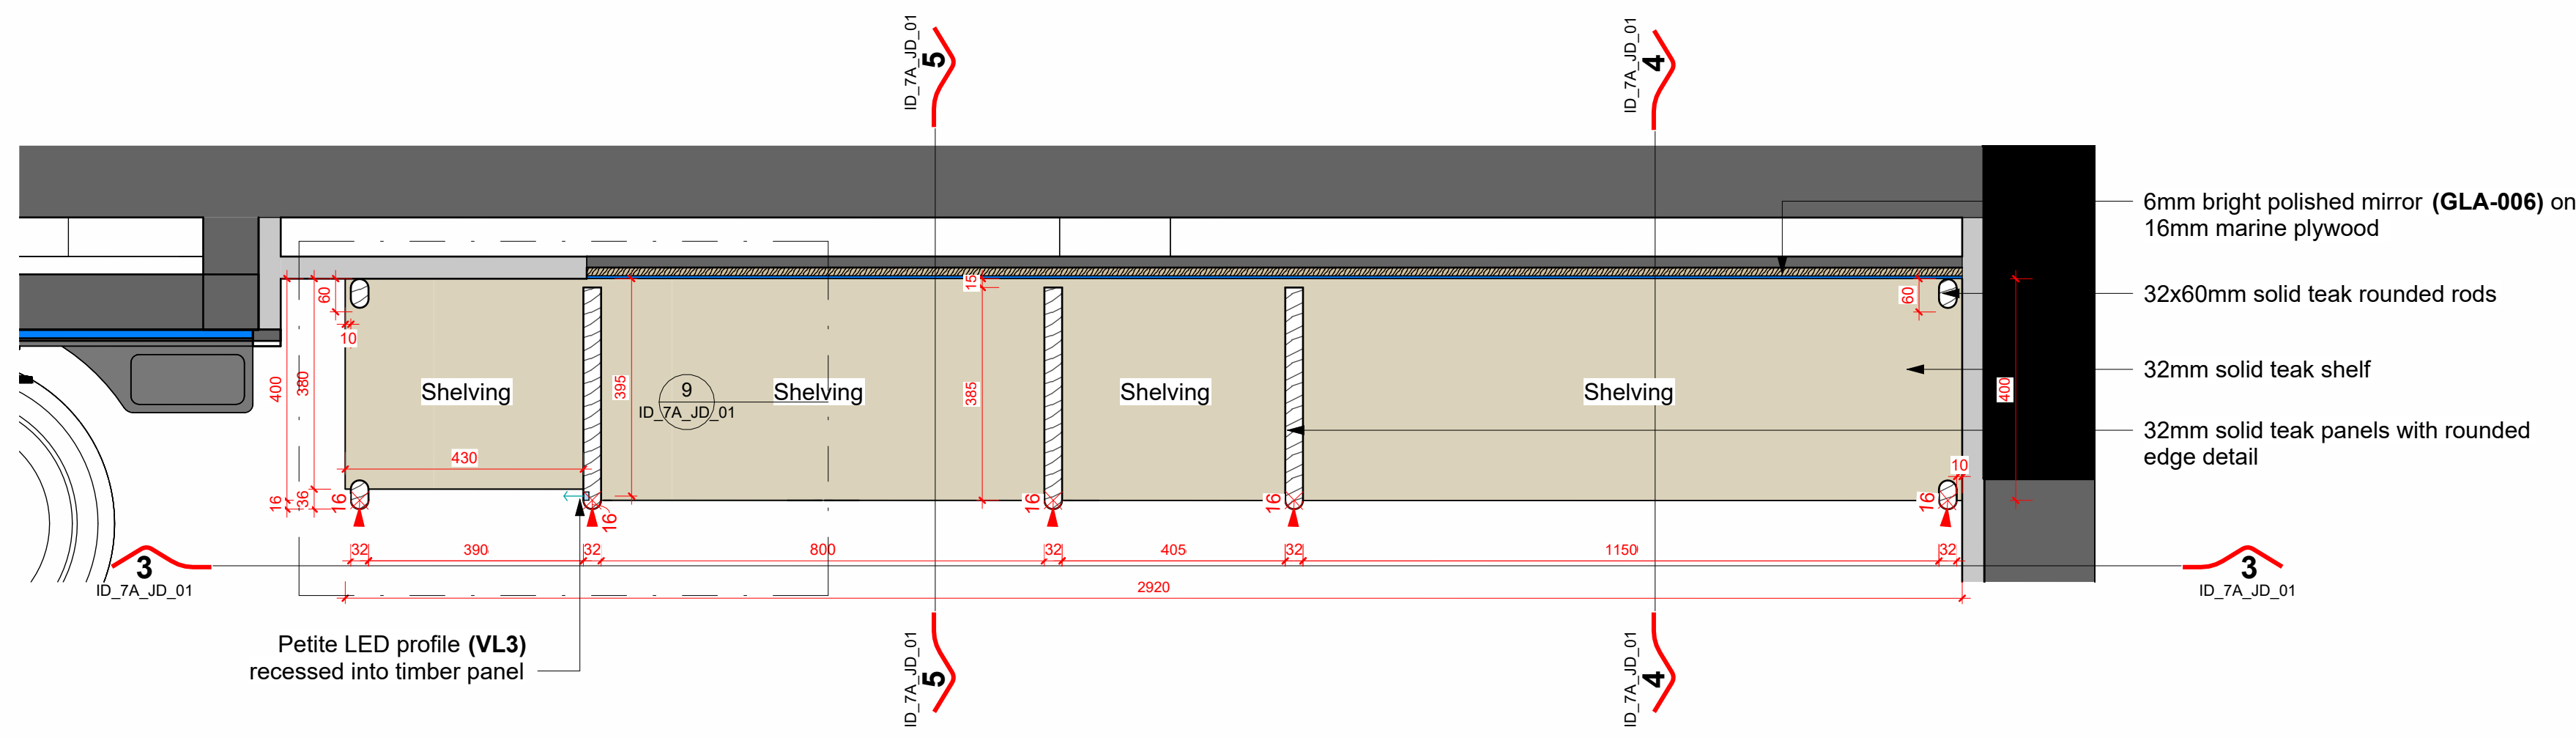


Floor Plan Upper View - Lockers | 1:10

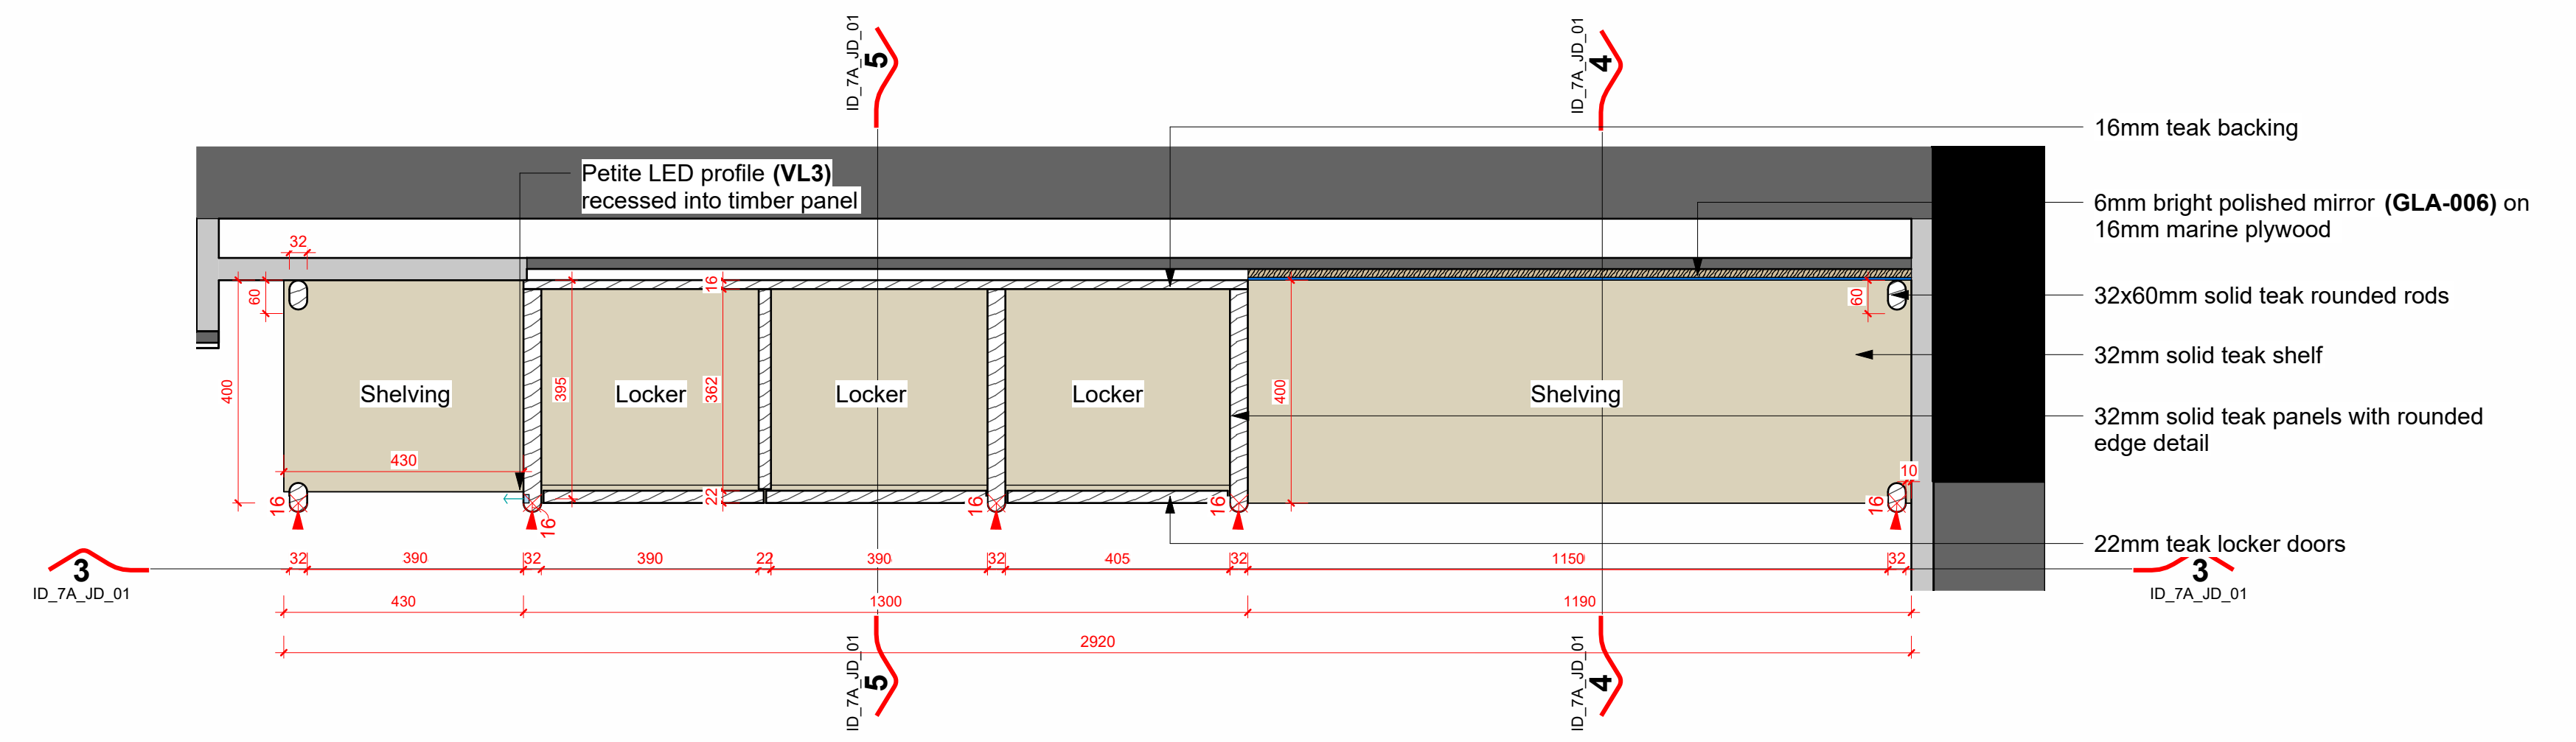


Floor Plan Lower View - Lockers | 1:10

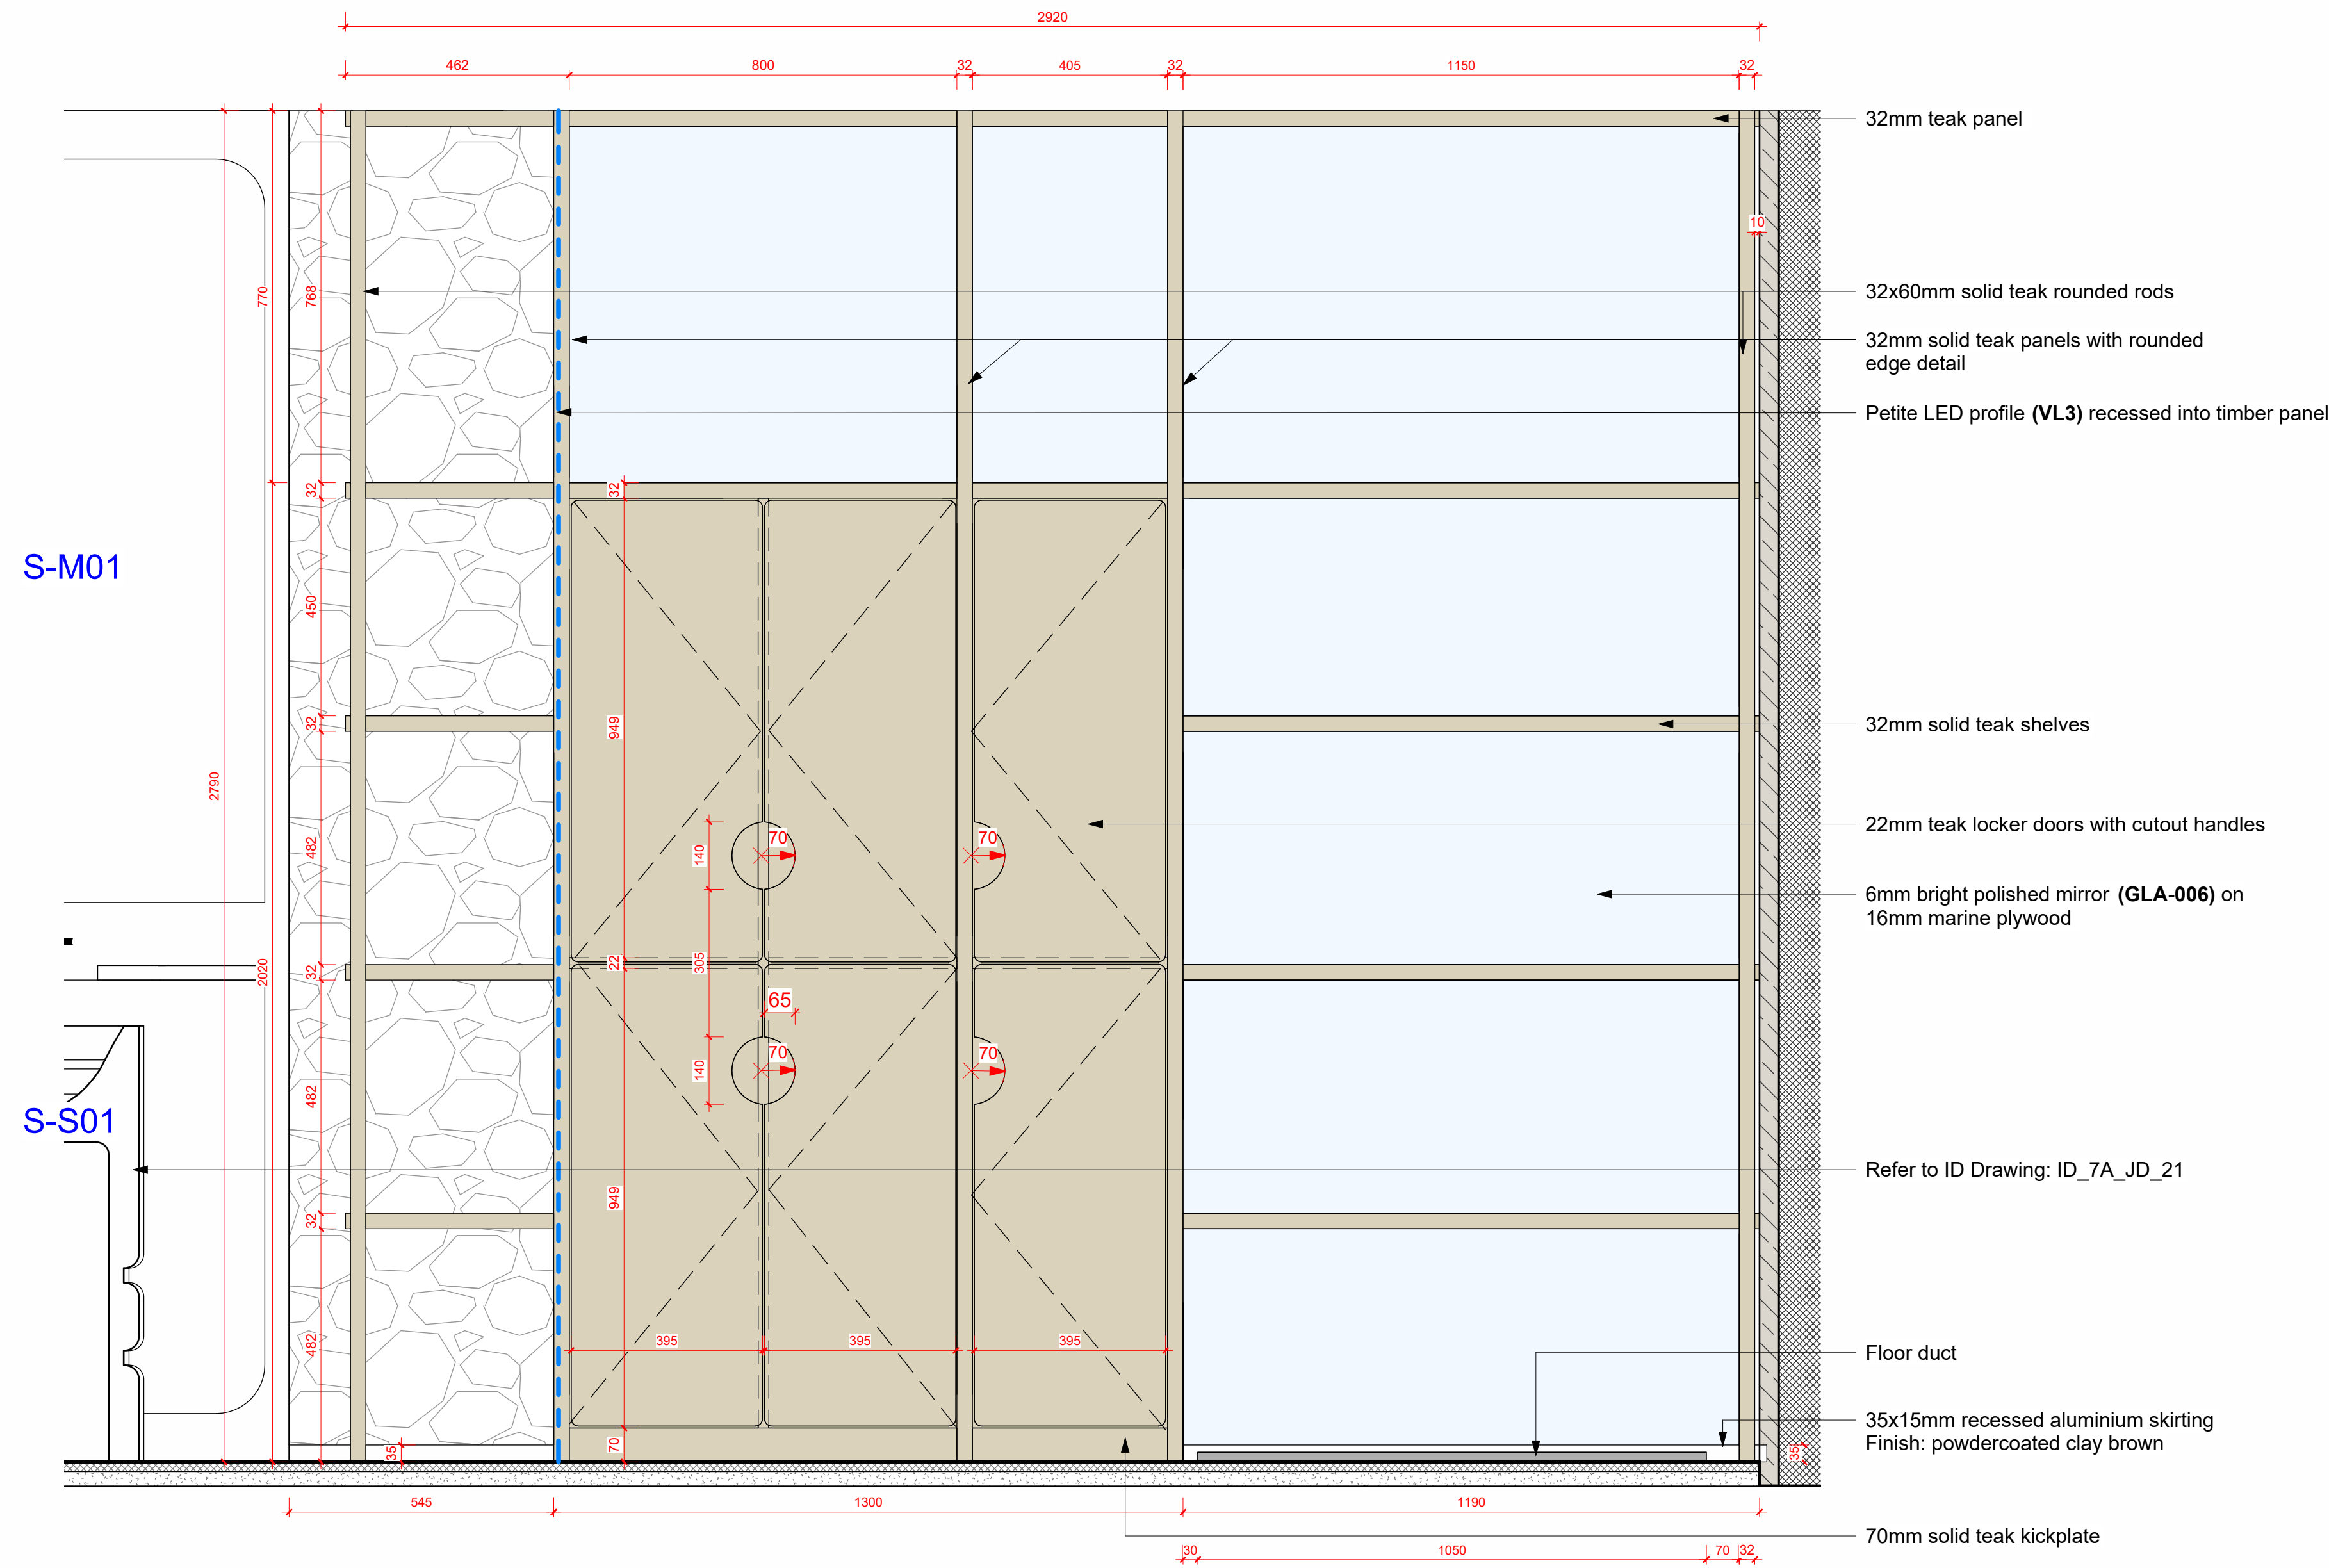


Front Elevation - Lockers | 1:10

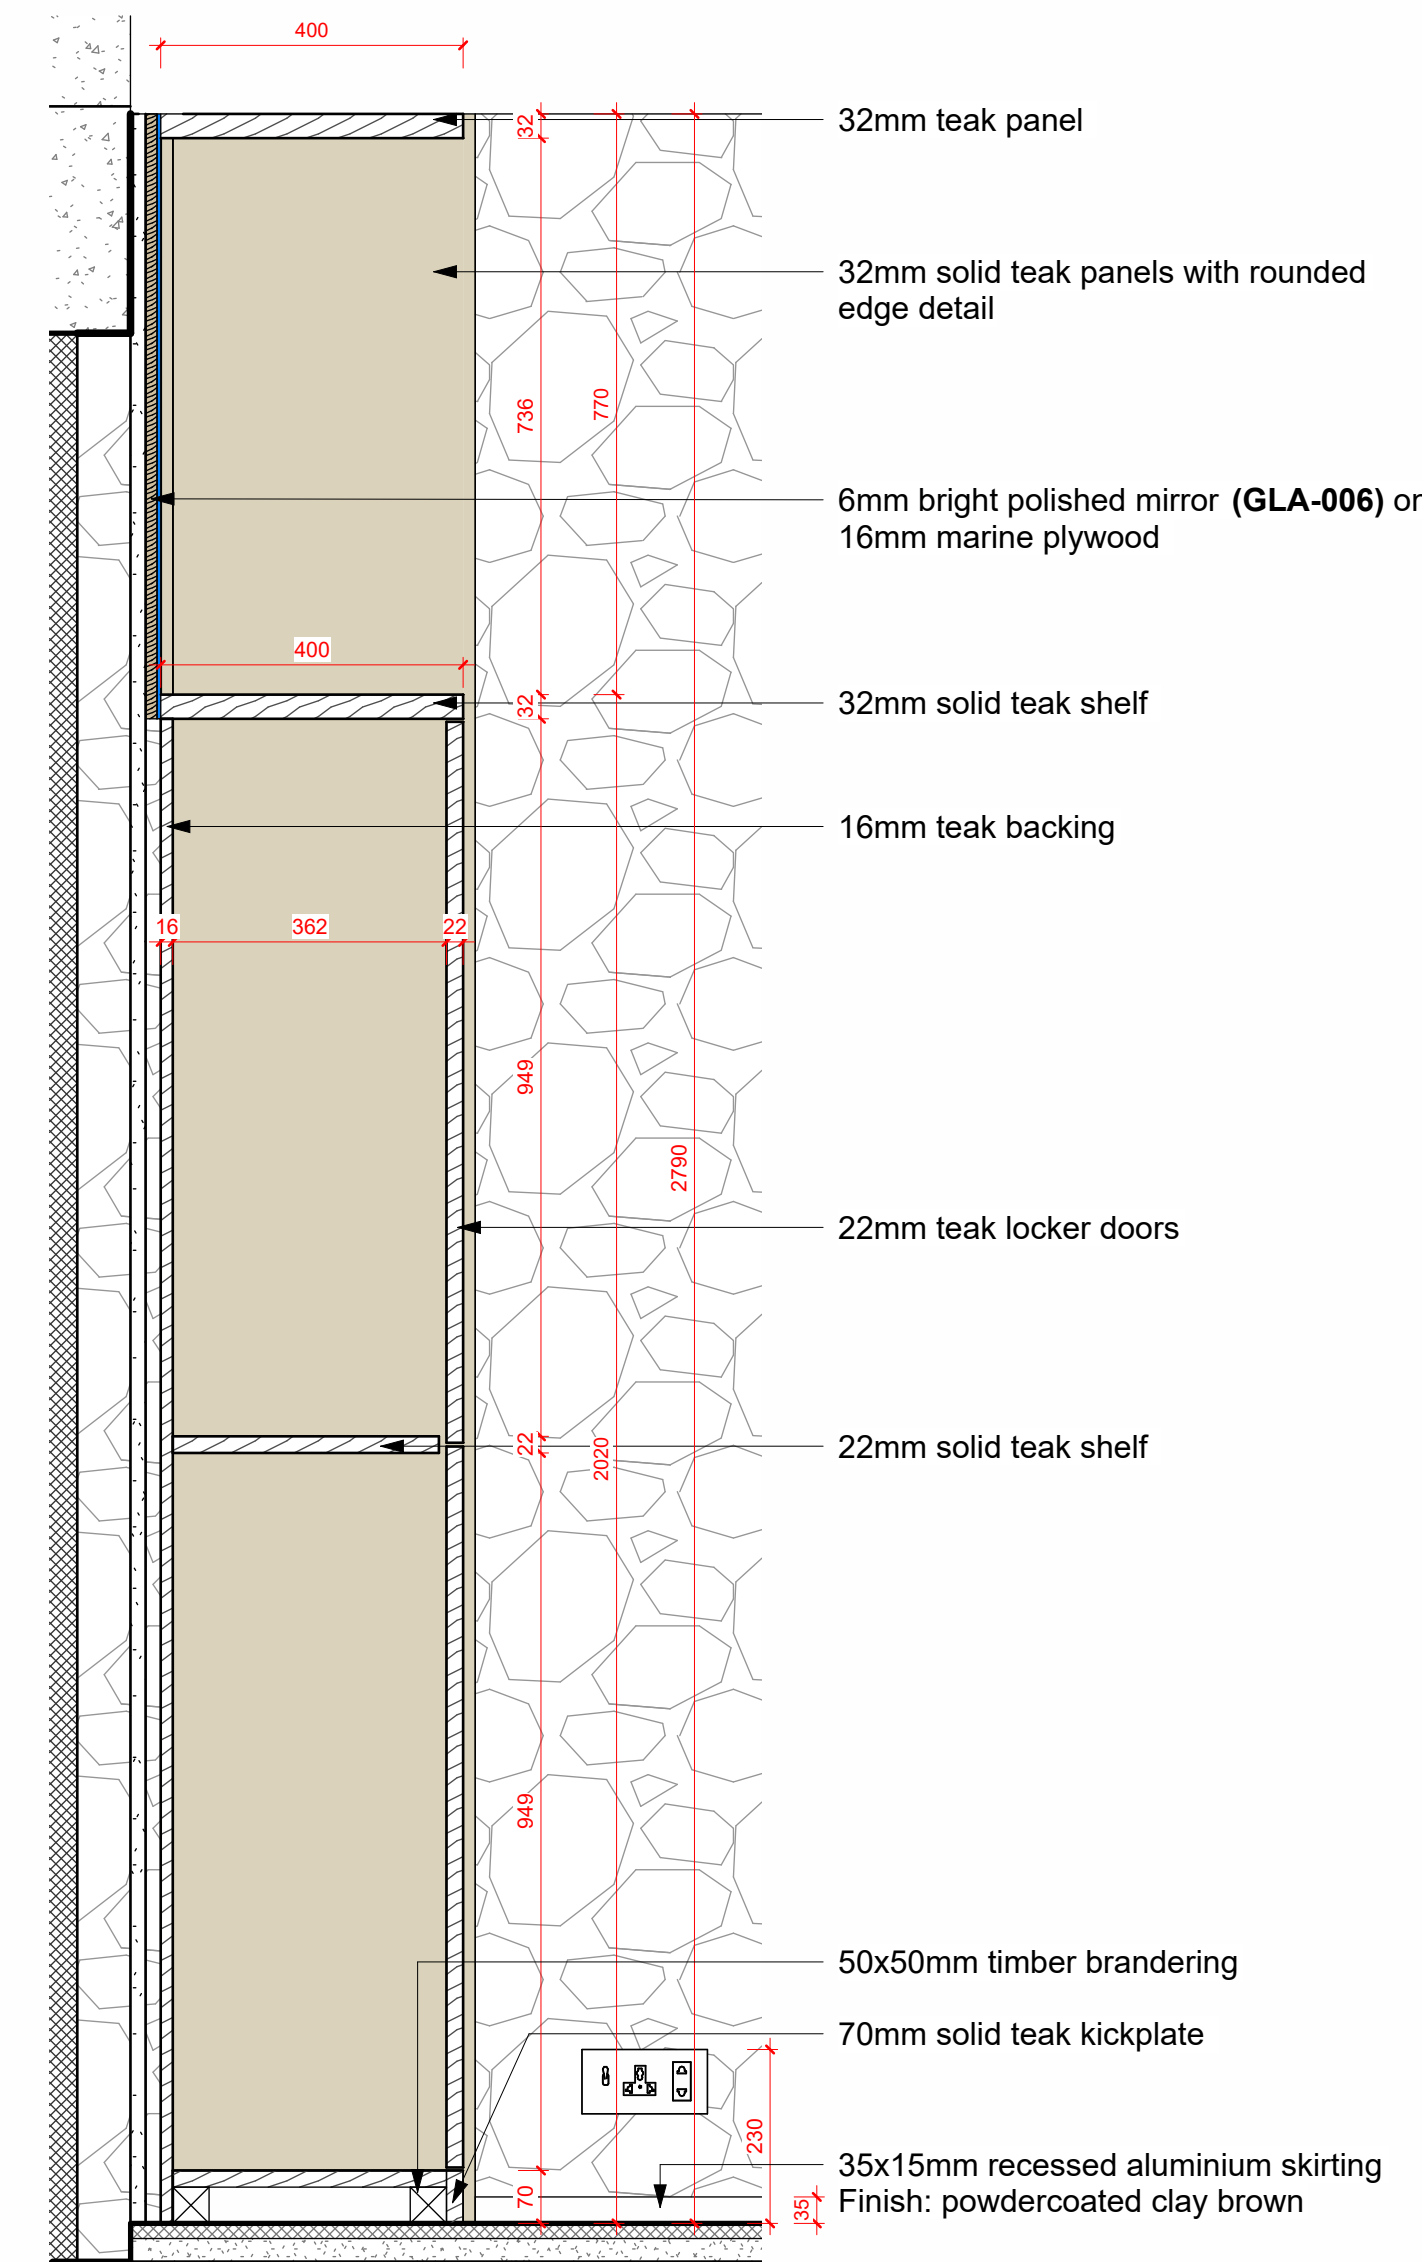


Section - Locker Cupboards | 1:10

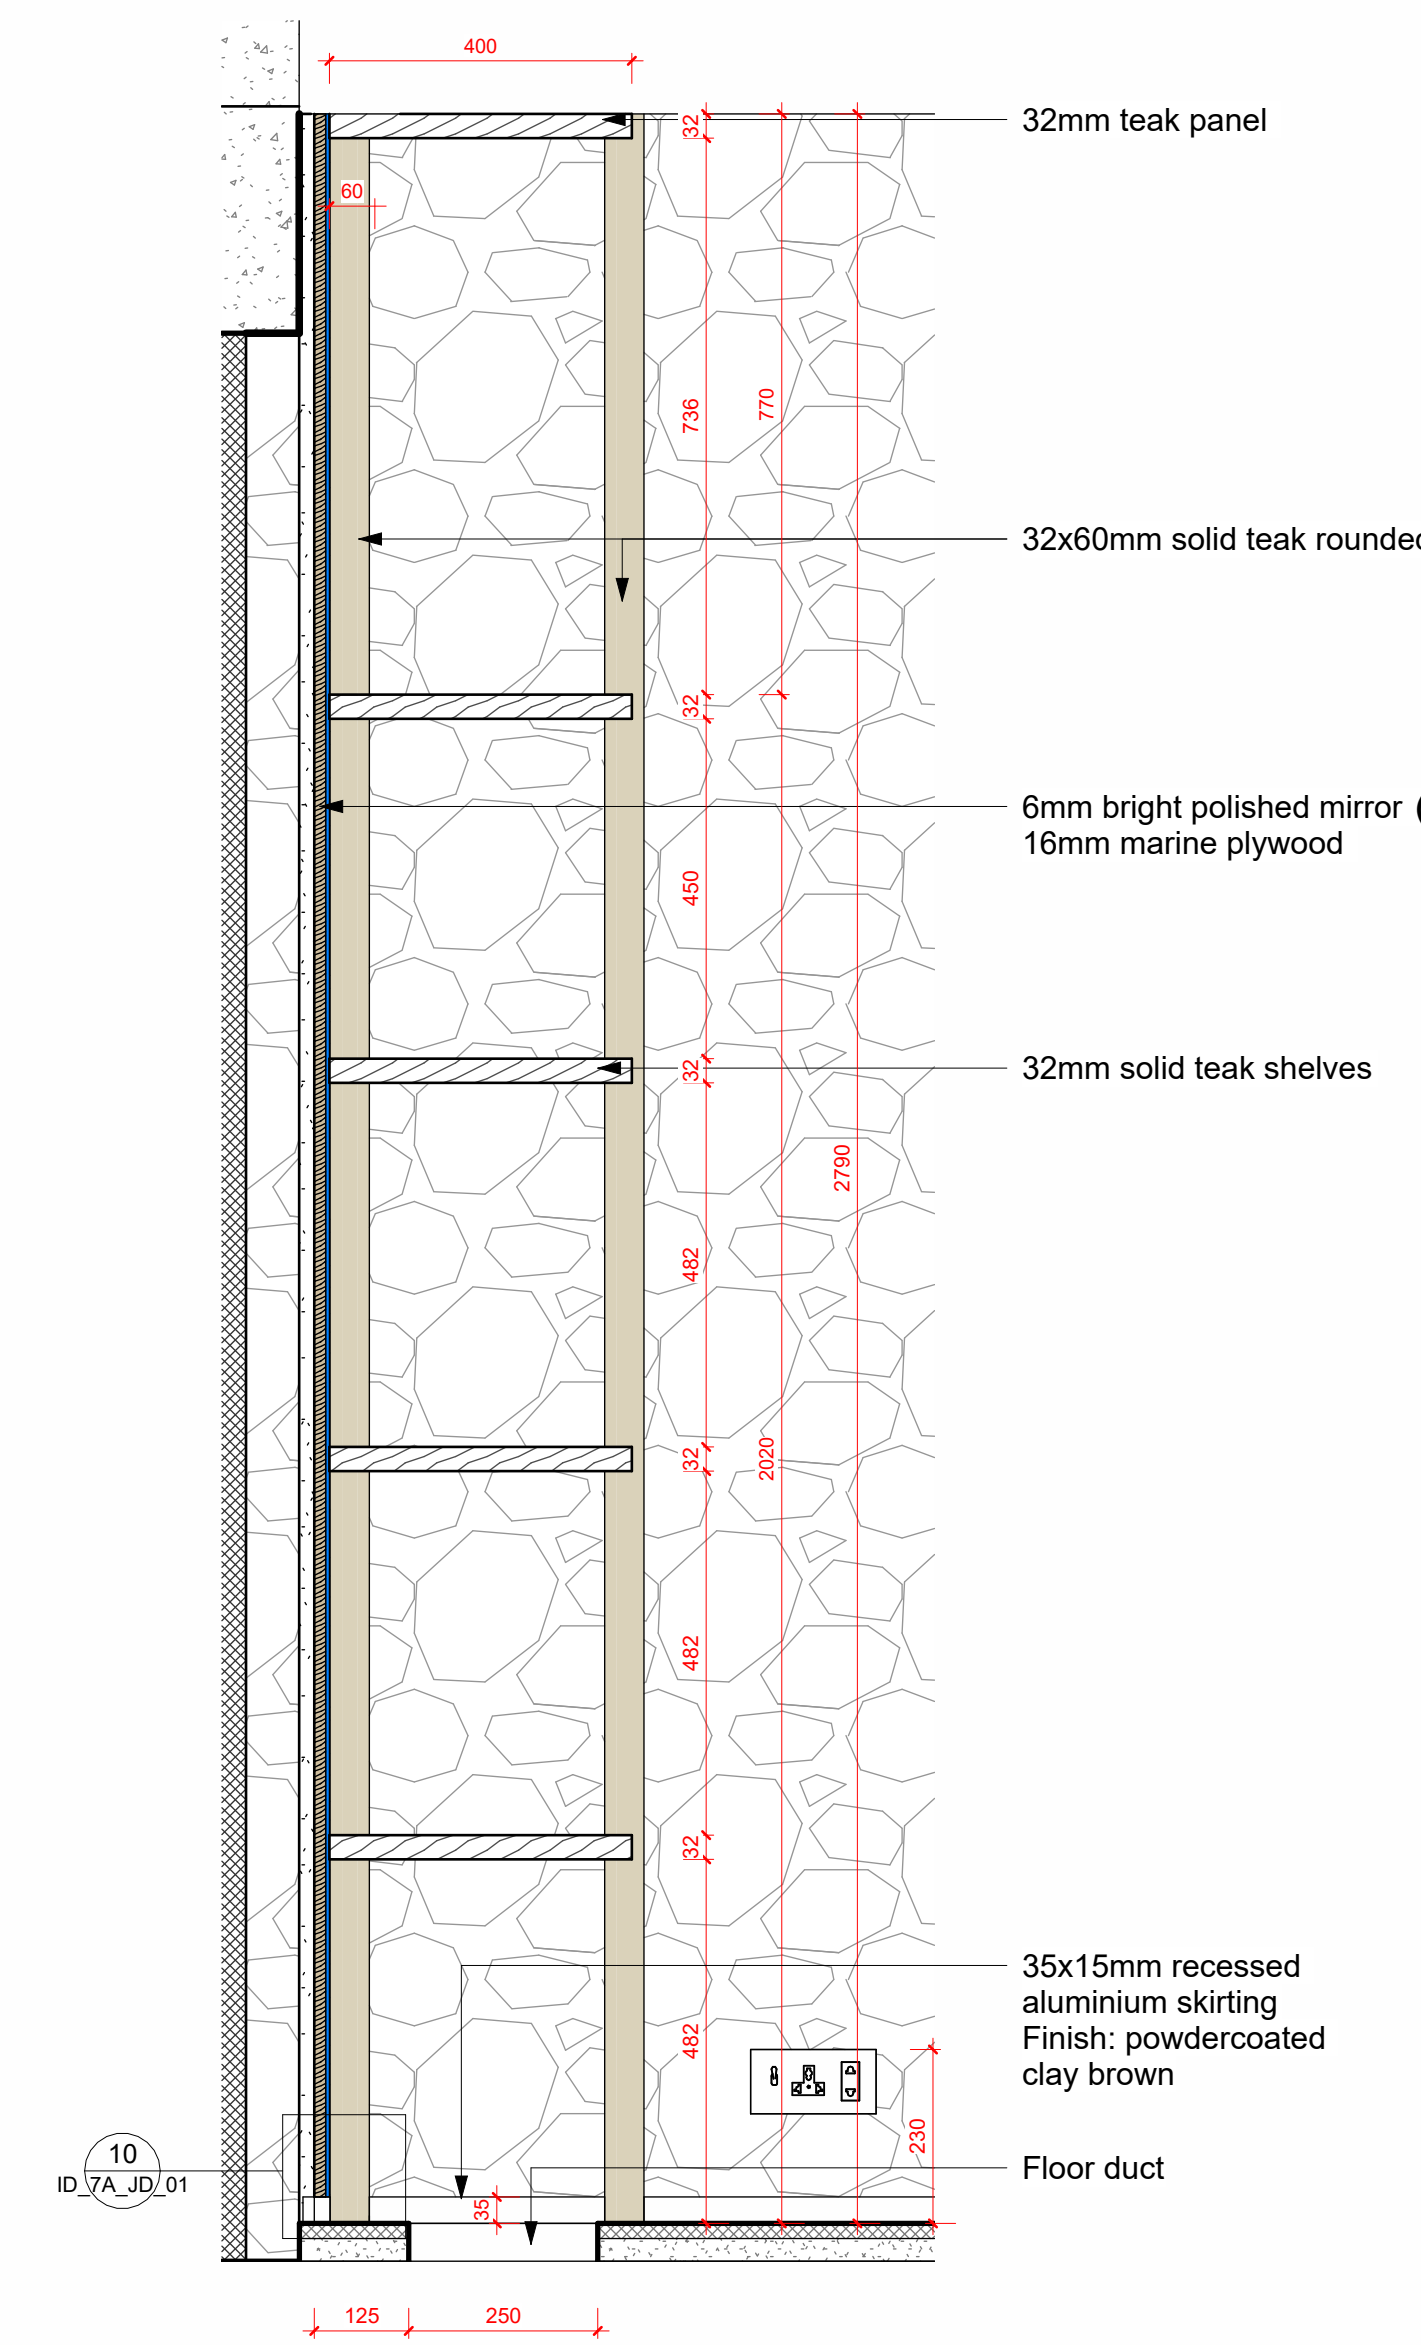


Section - Locker Shelves | 1:10

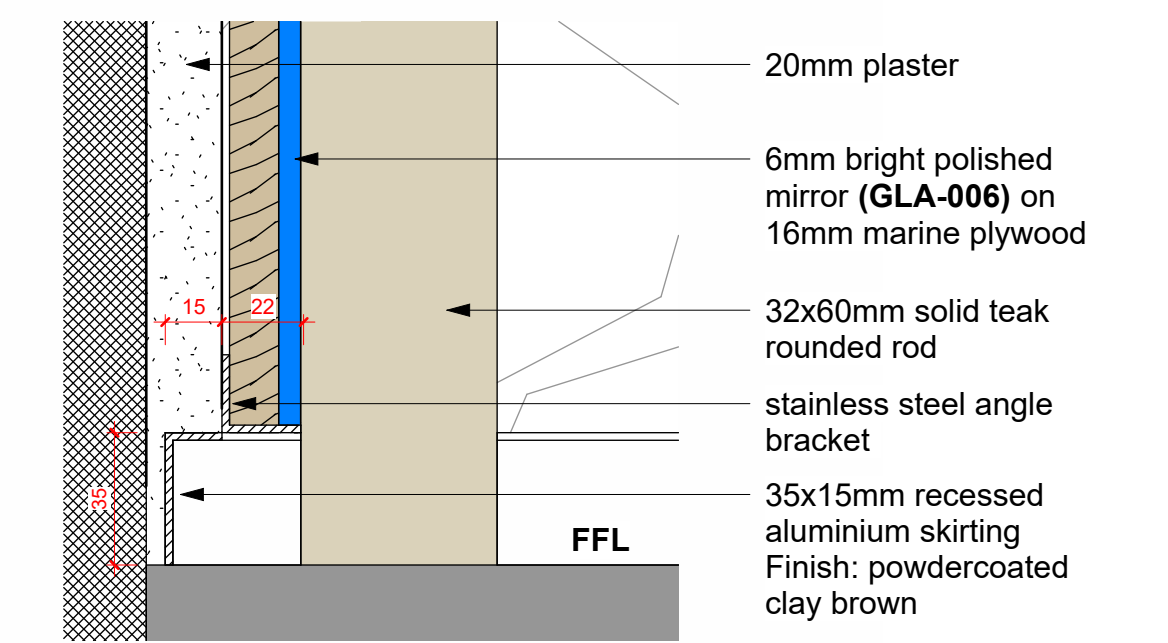


Callout - Skirting Detail | 1:2

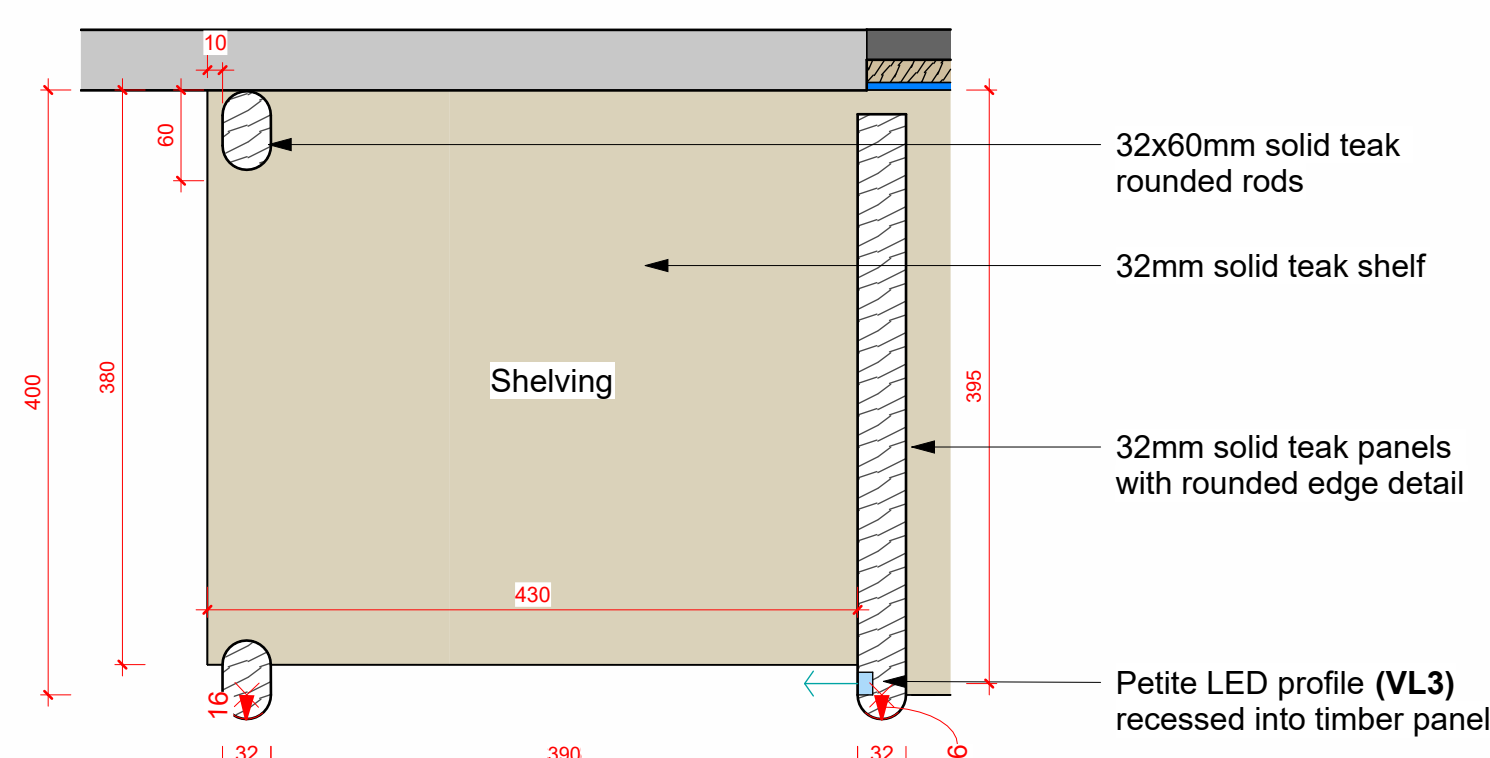


Floor Plan Callout - LED Strip Light | 1:5

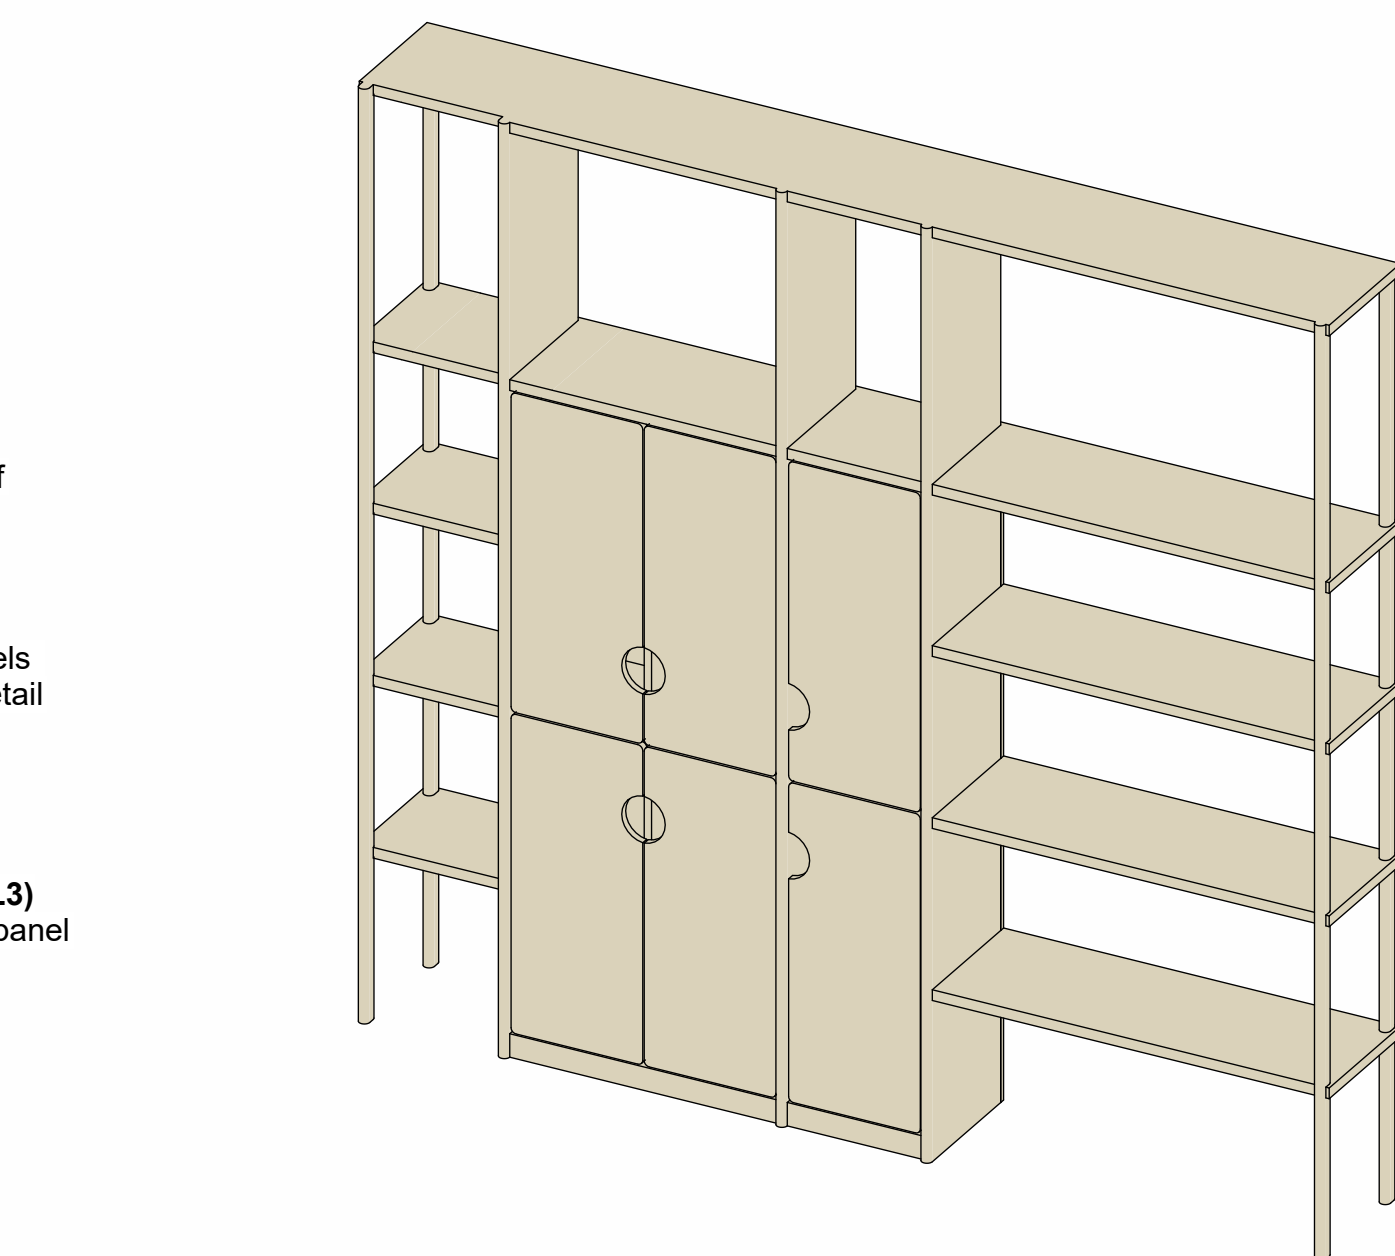

3D View - Lockers | 1:20






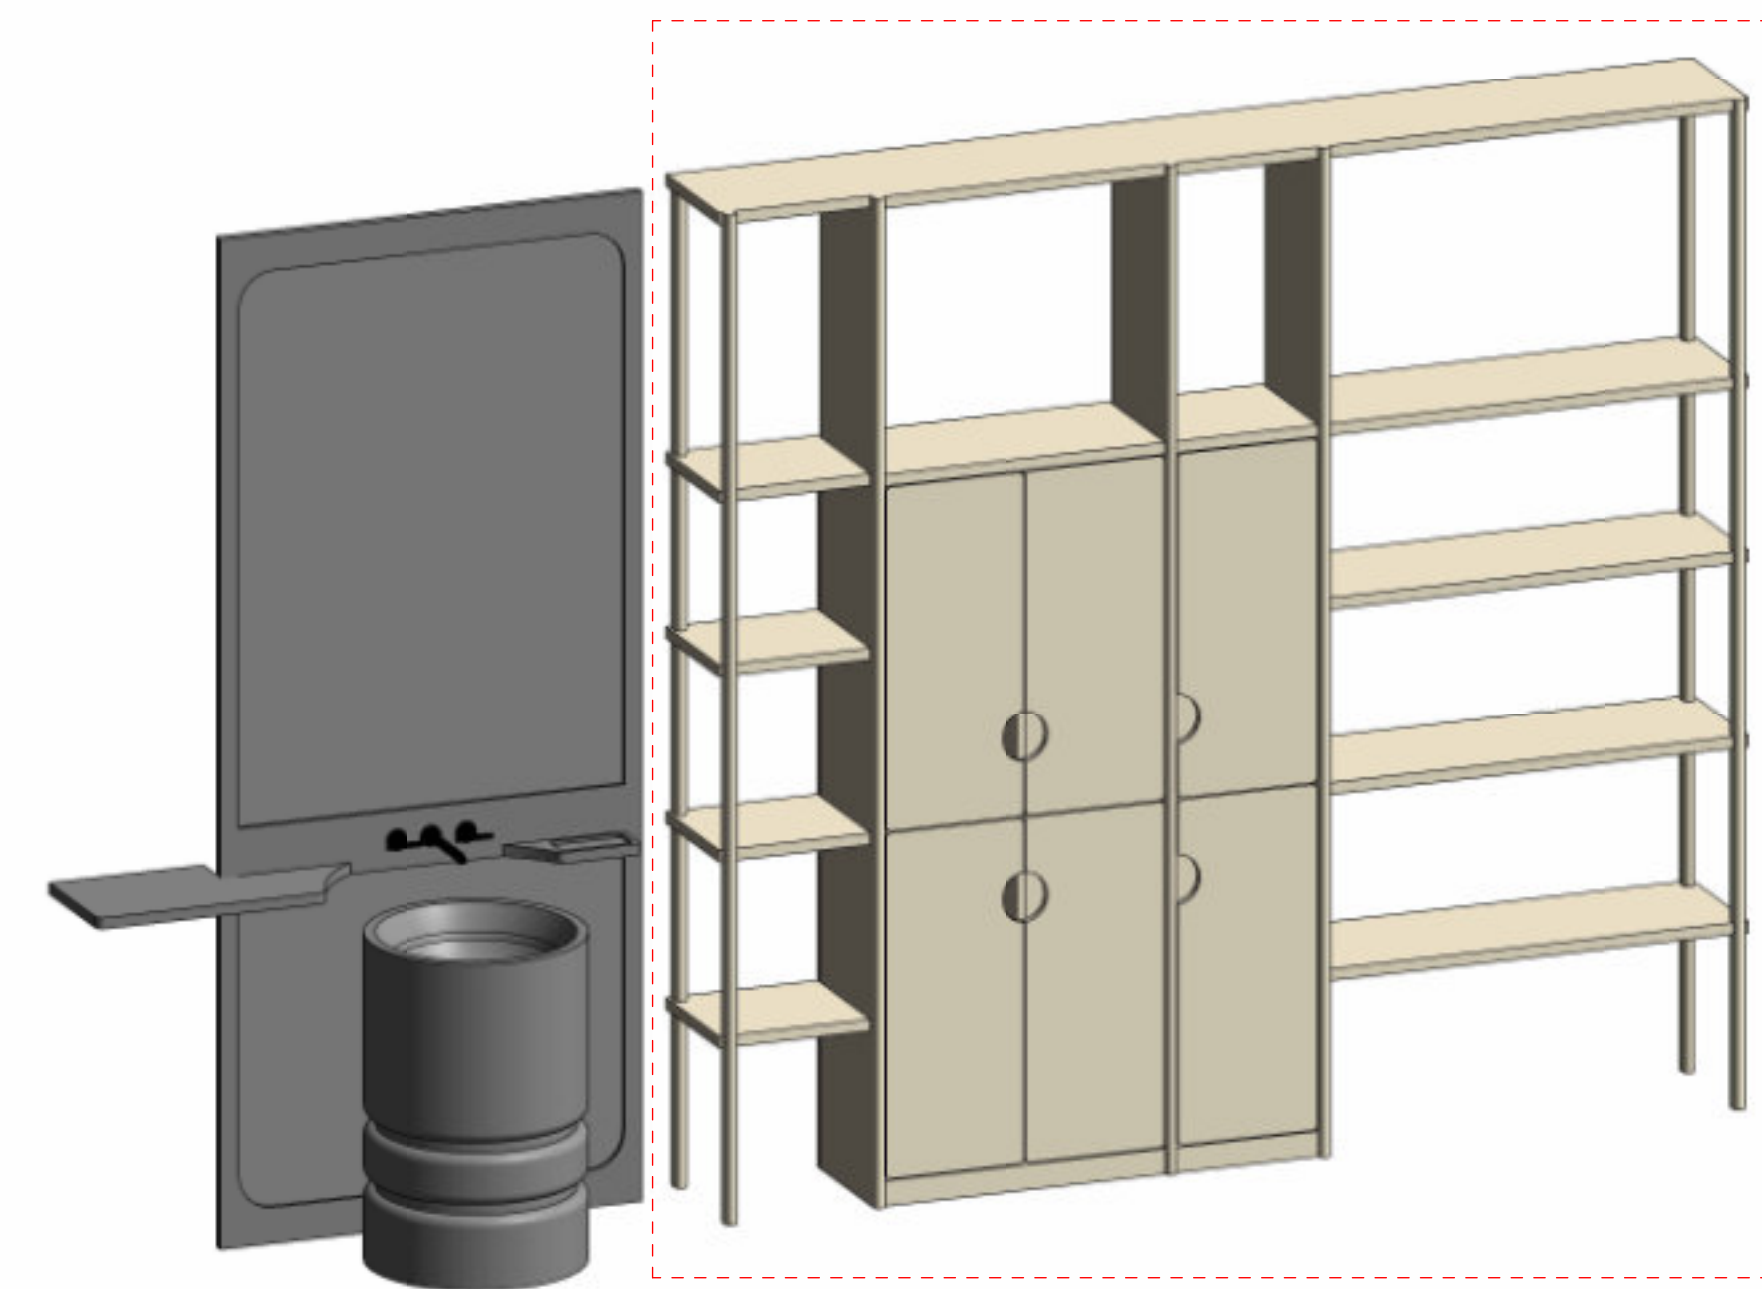


3D View - Vanity & Lockers | 1:20

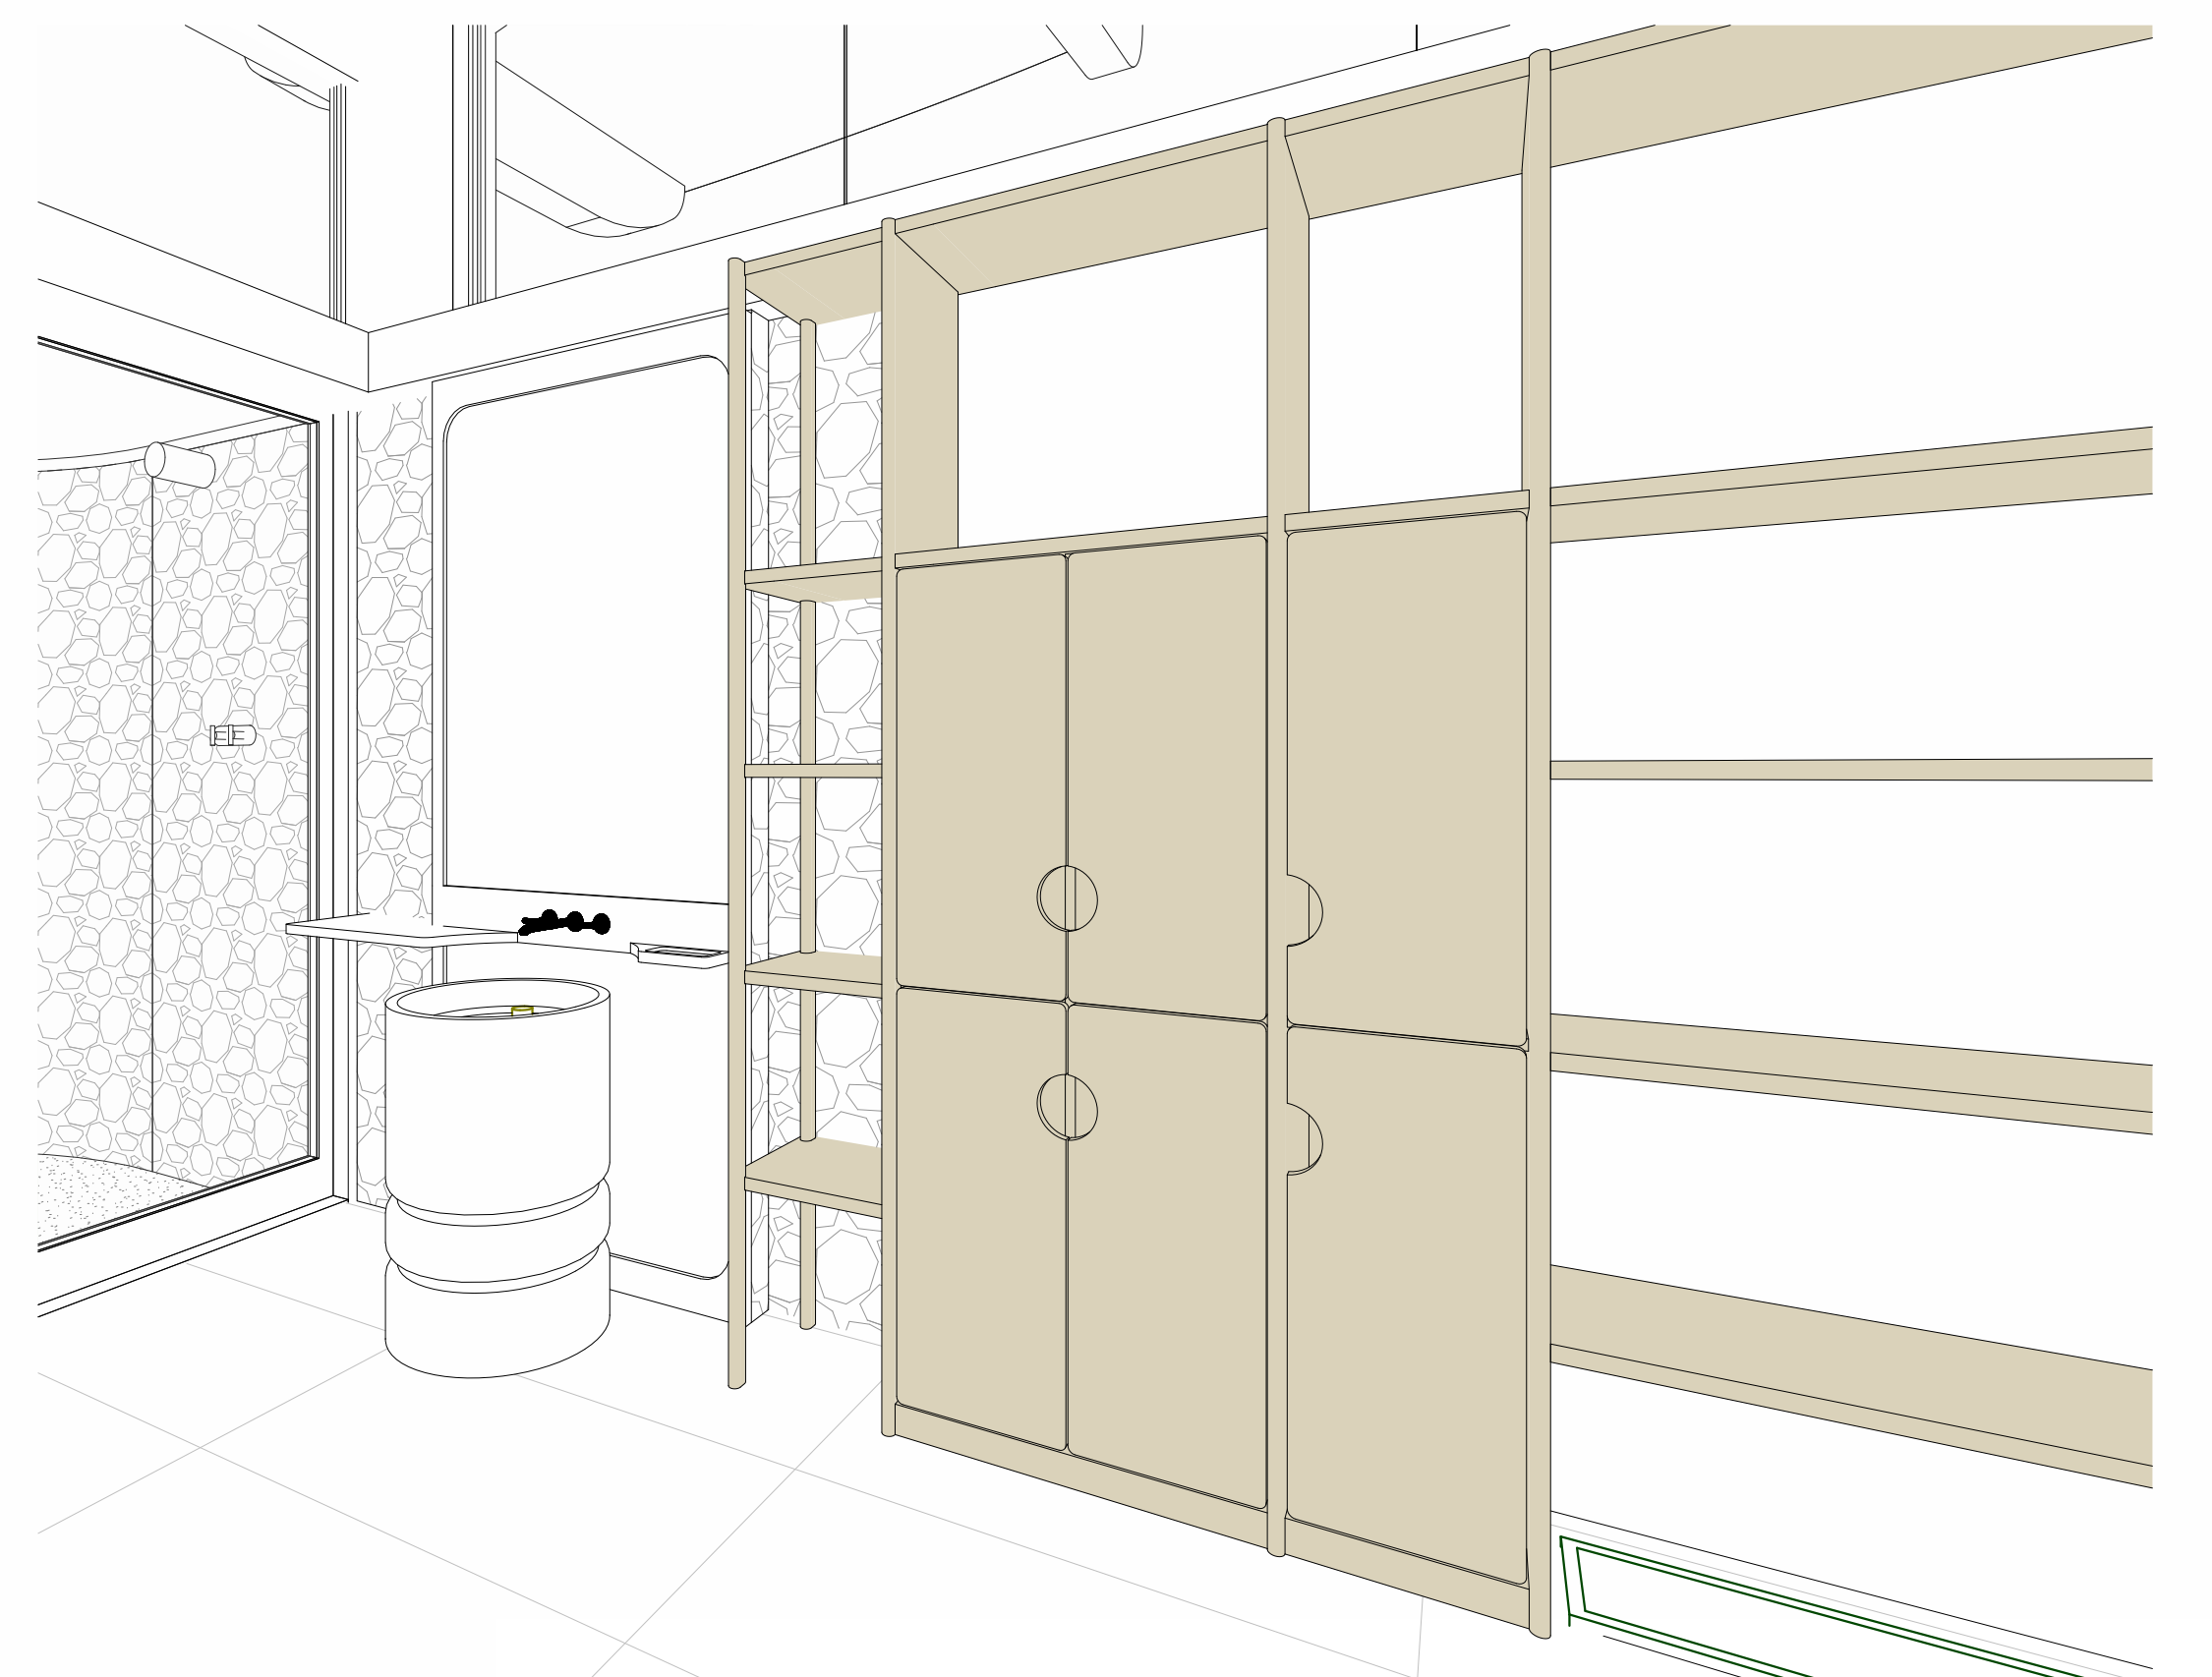


Perspective - Vanity & Lockers | N.T.S.



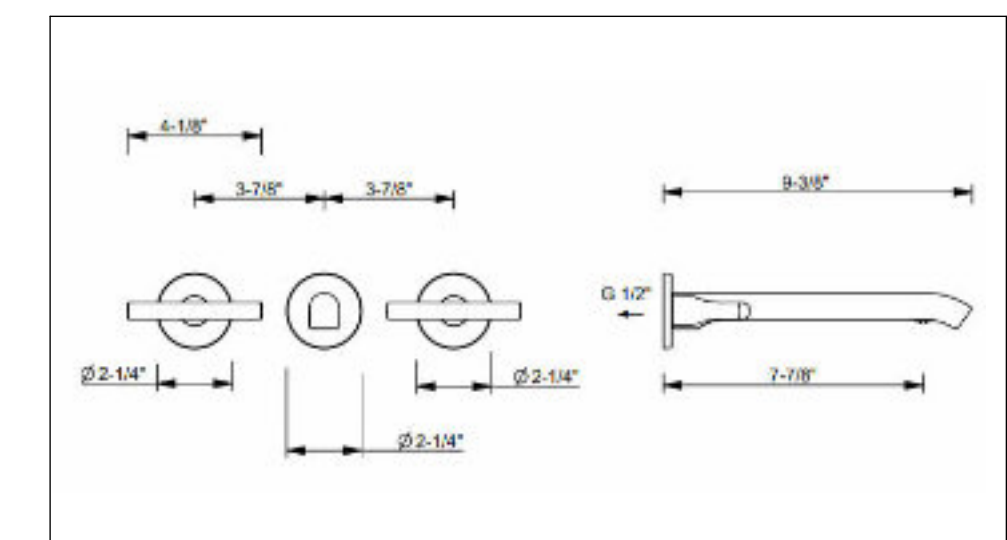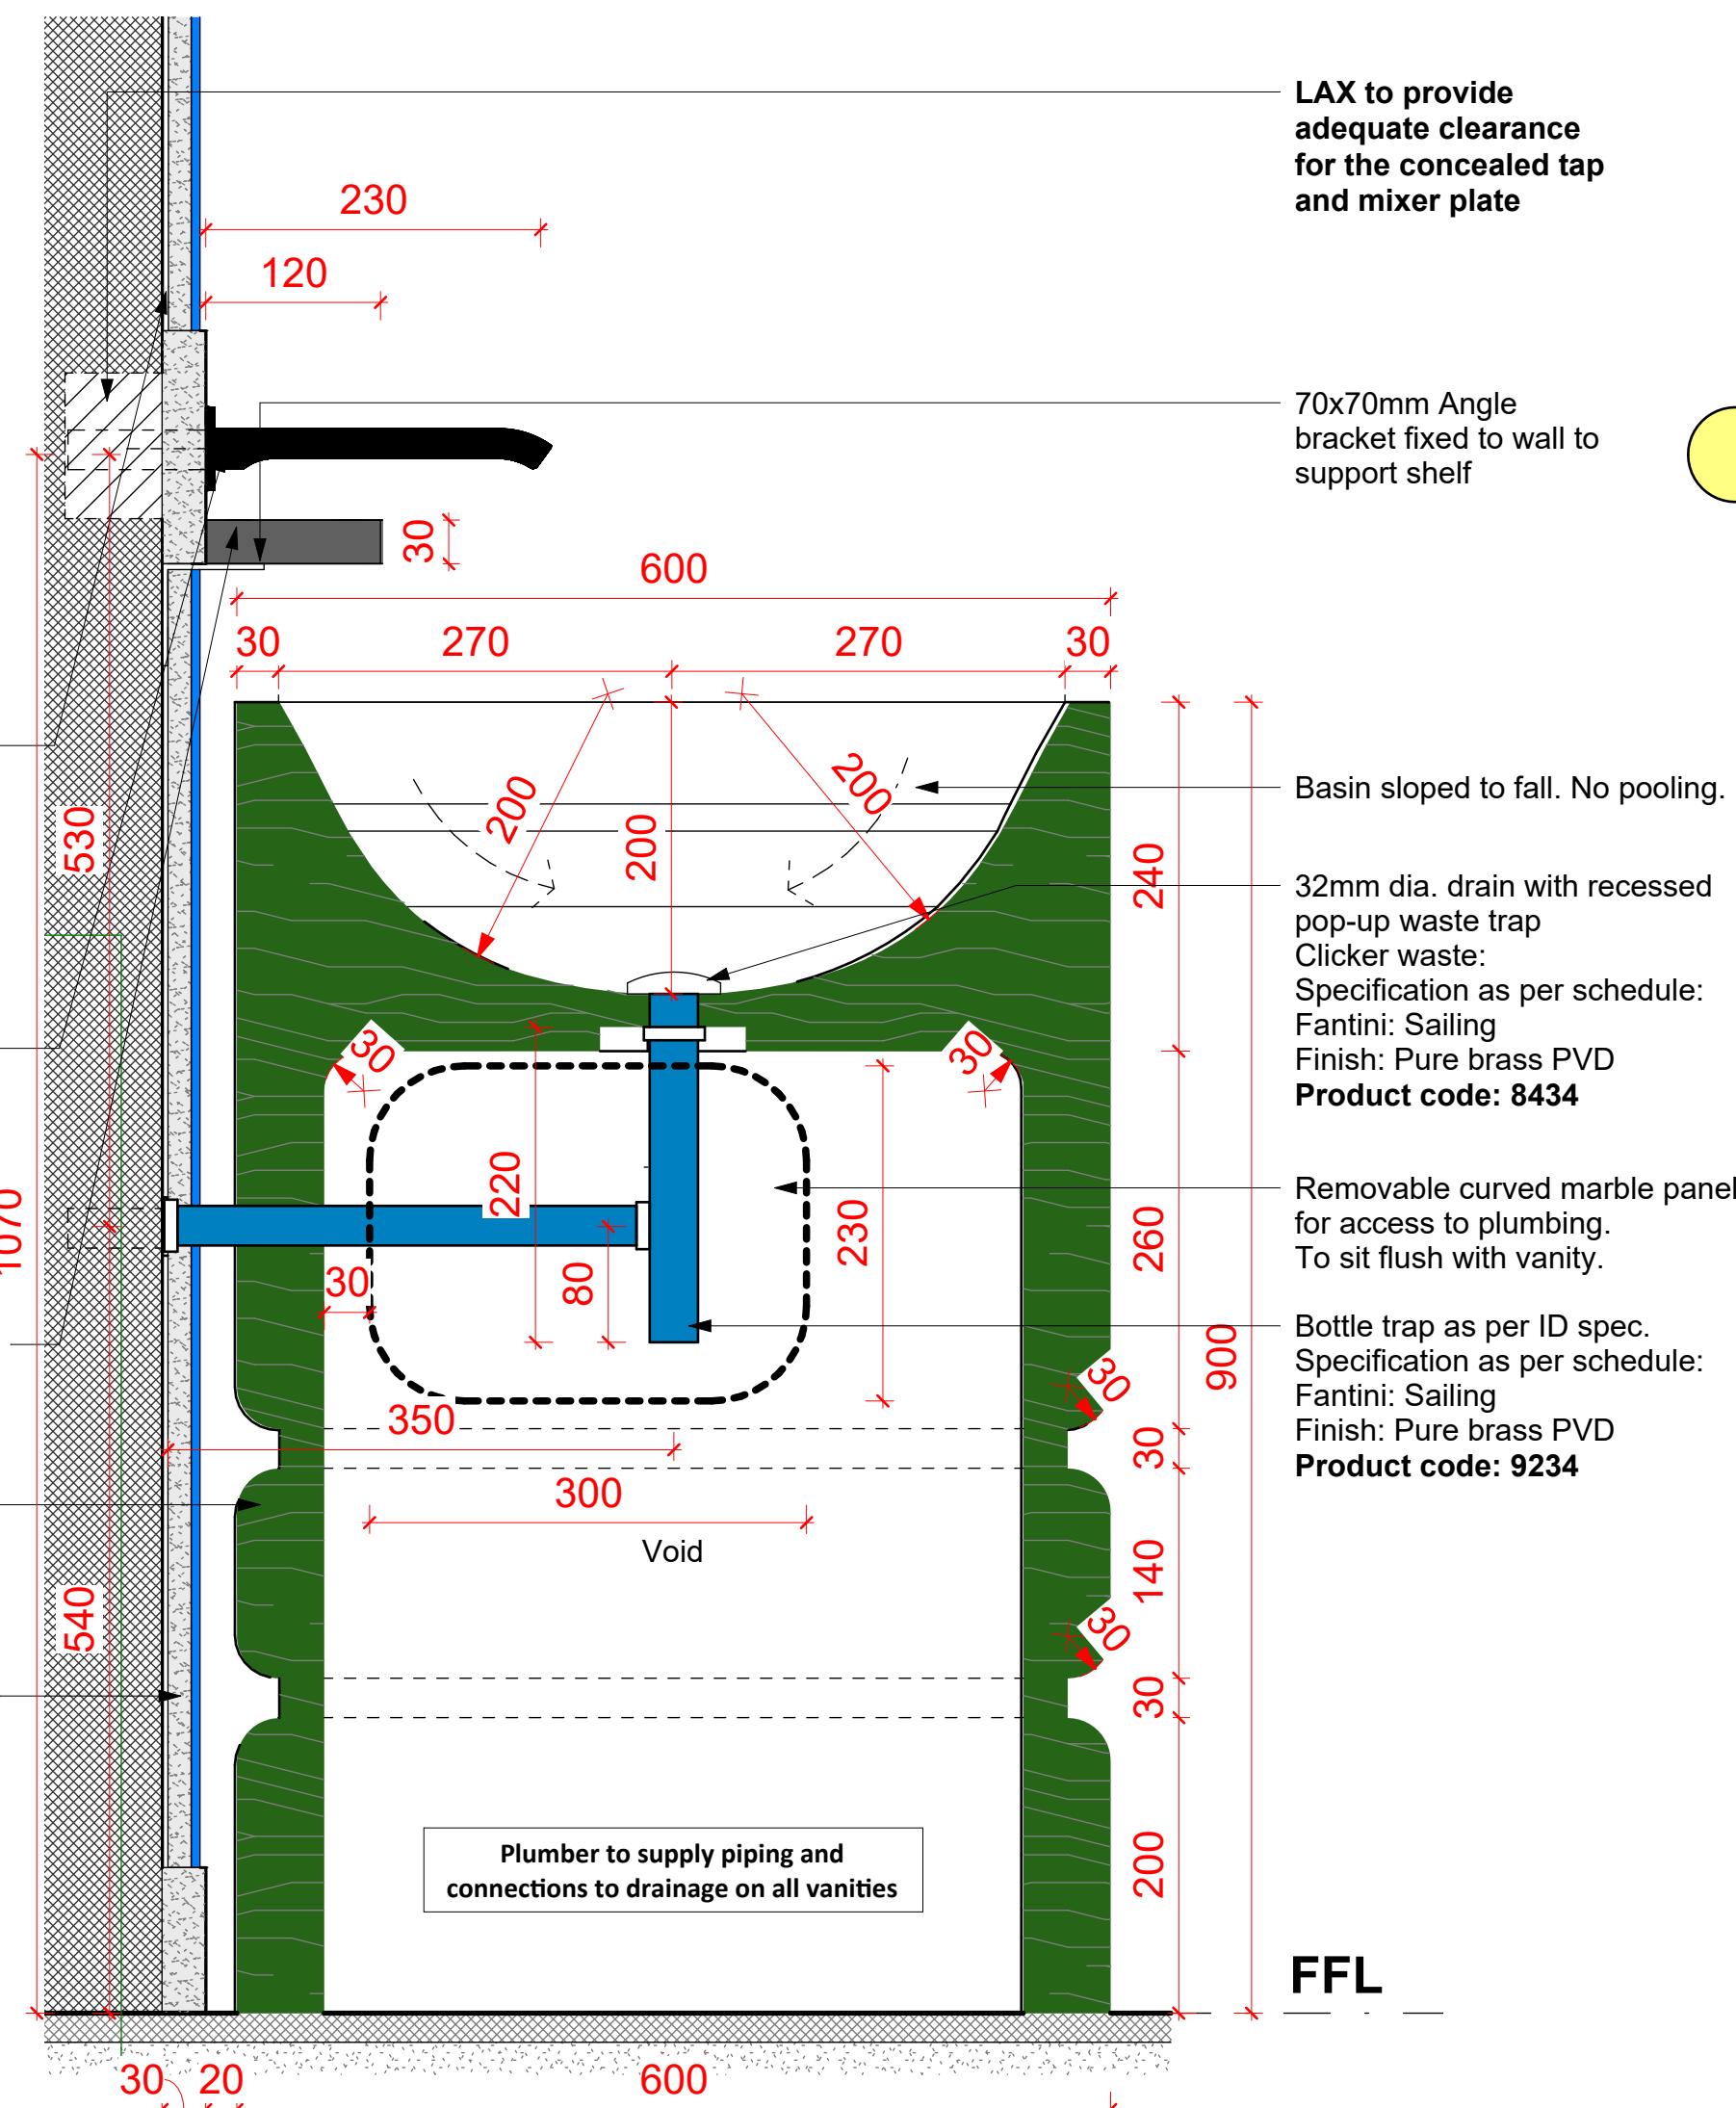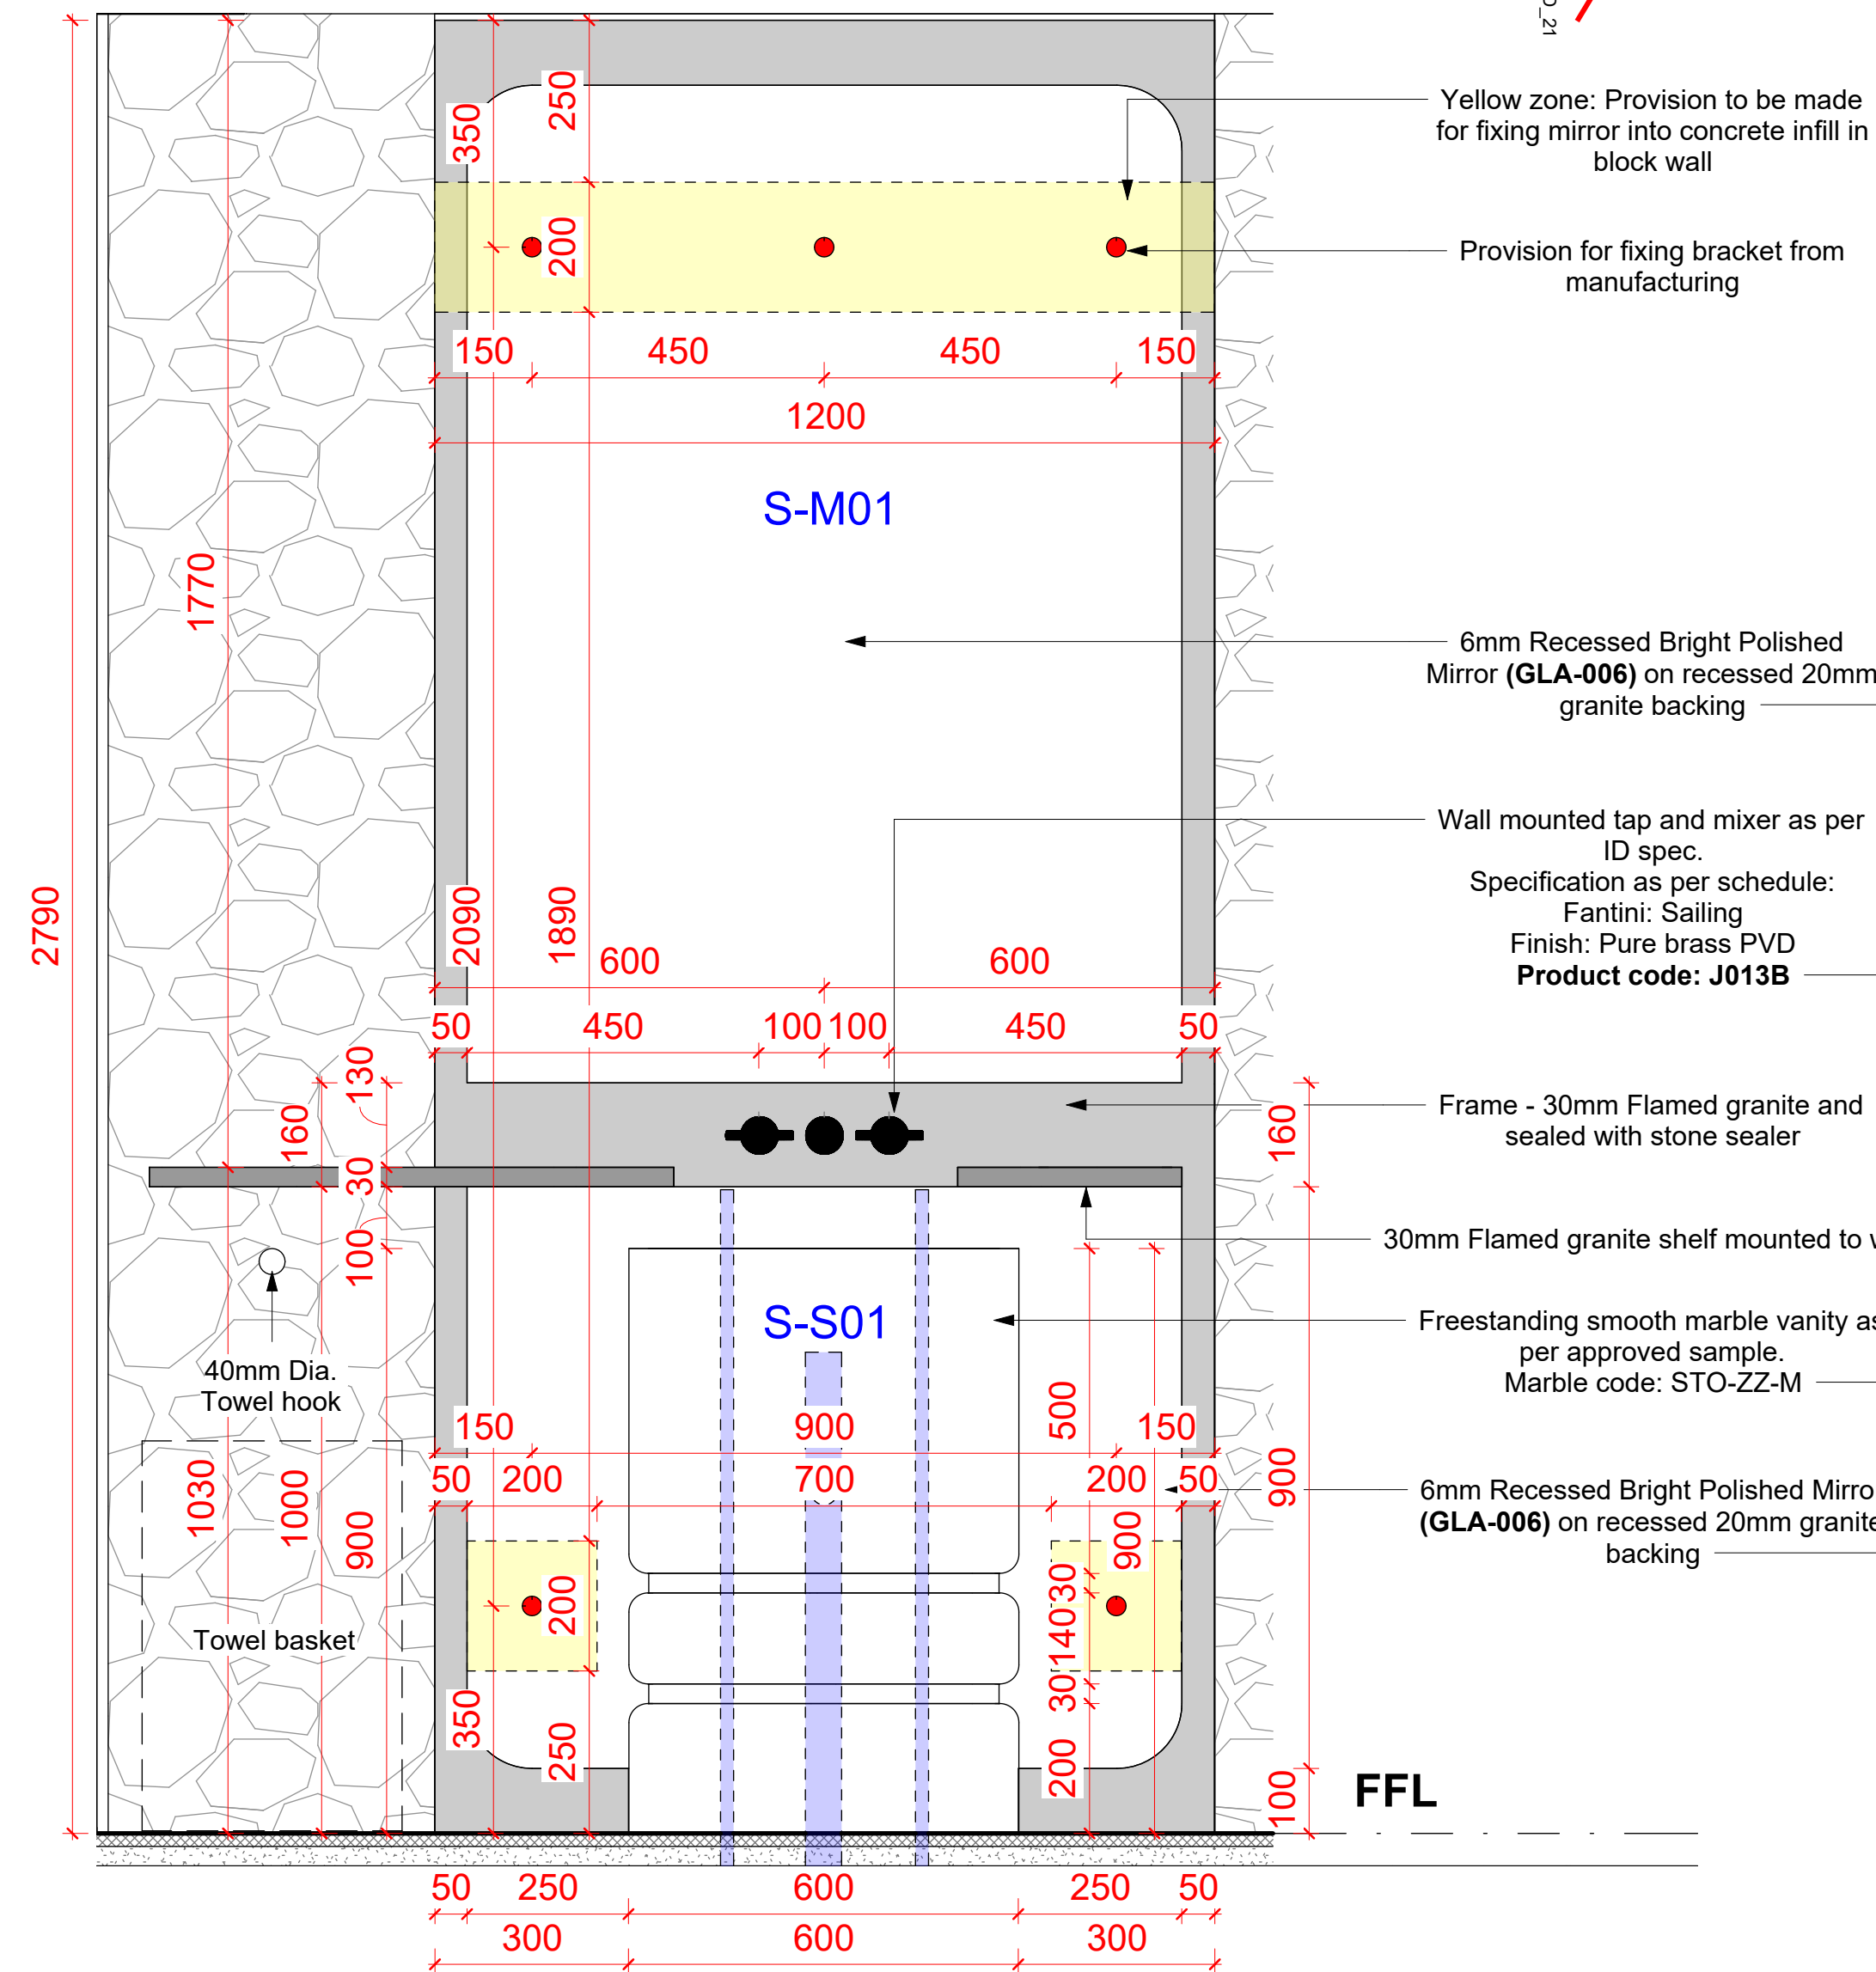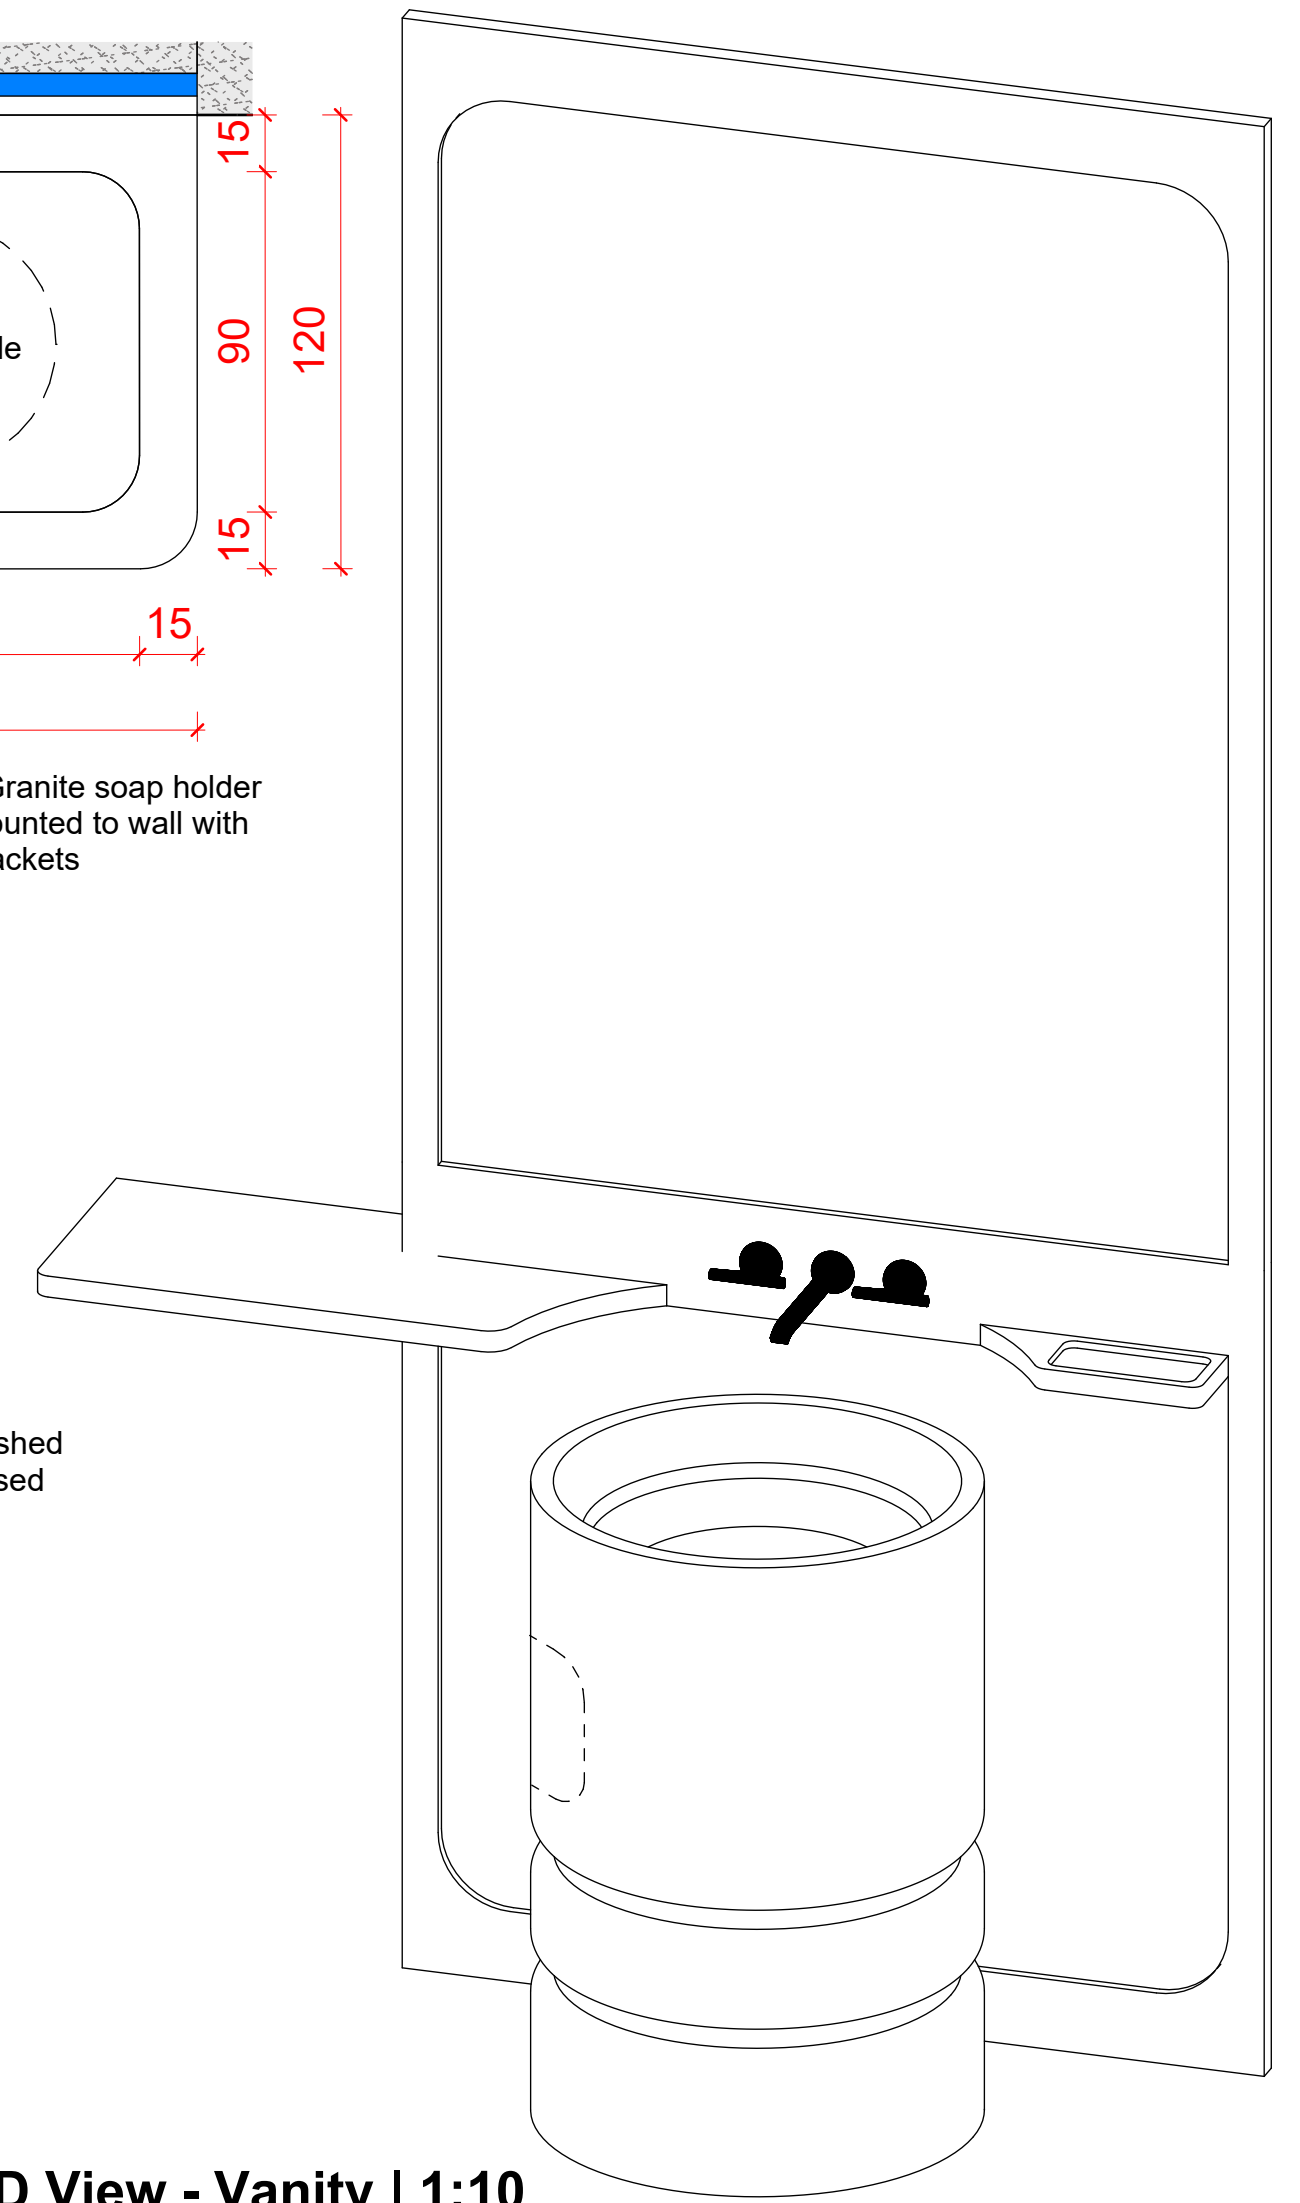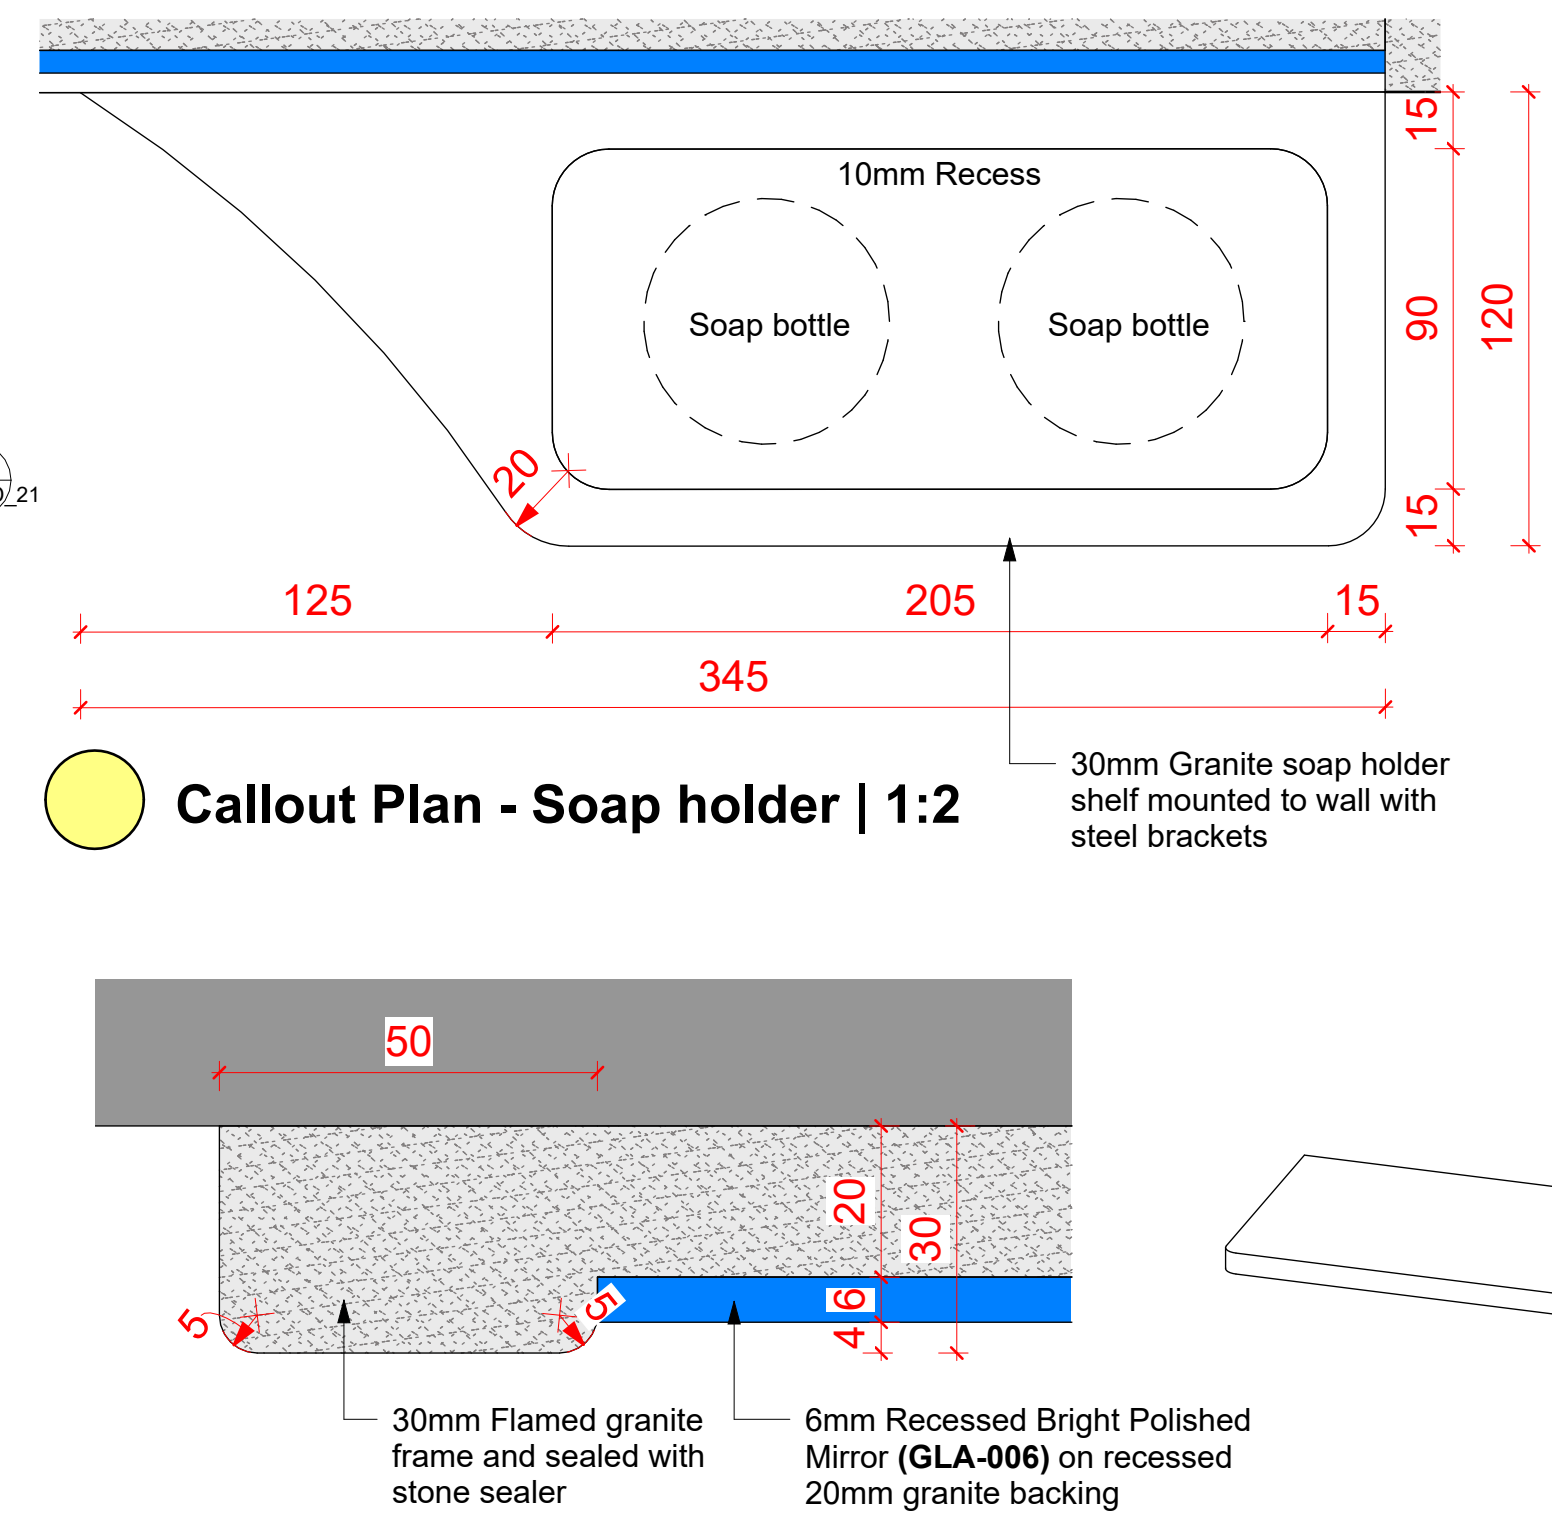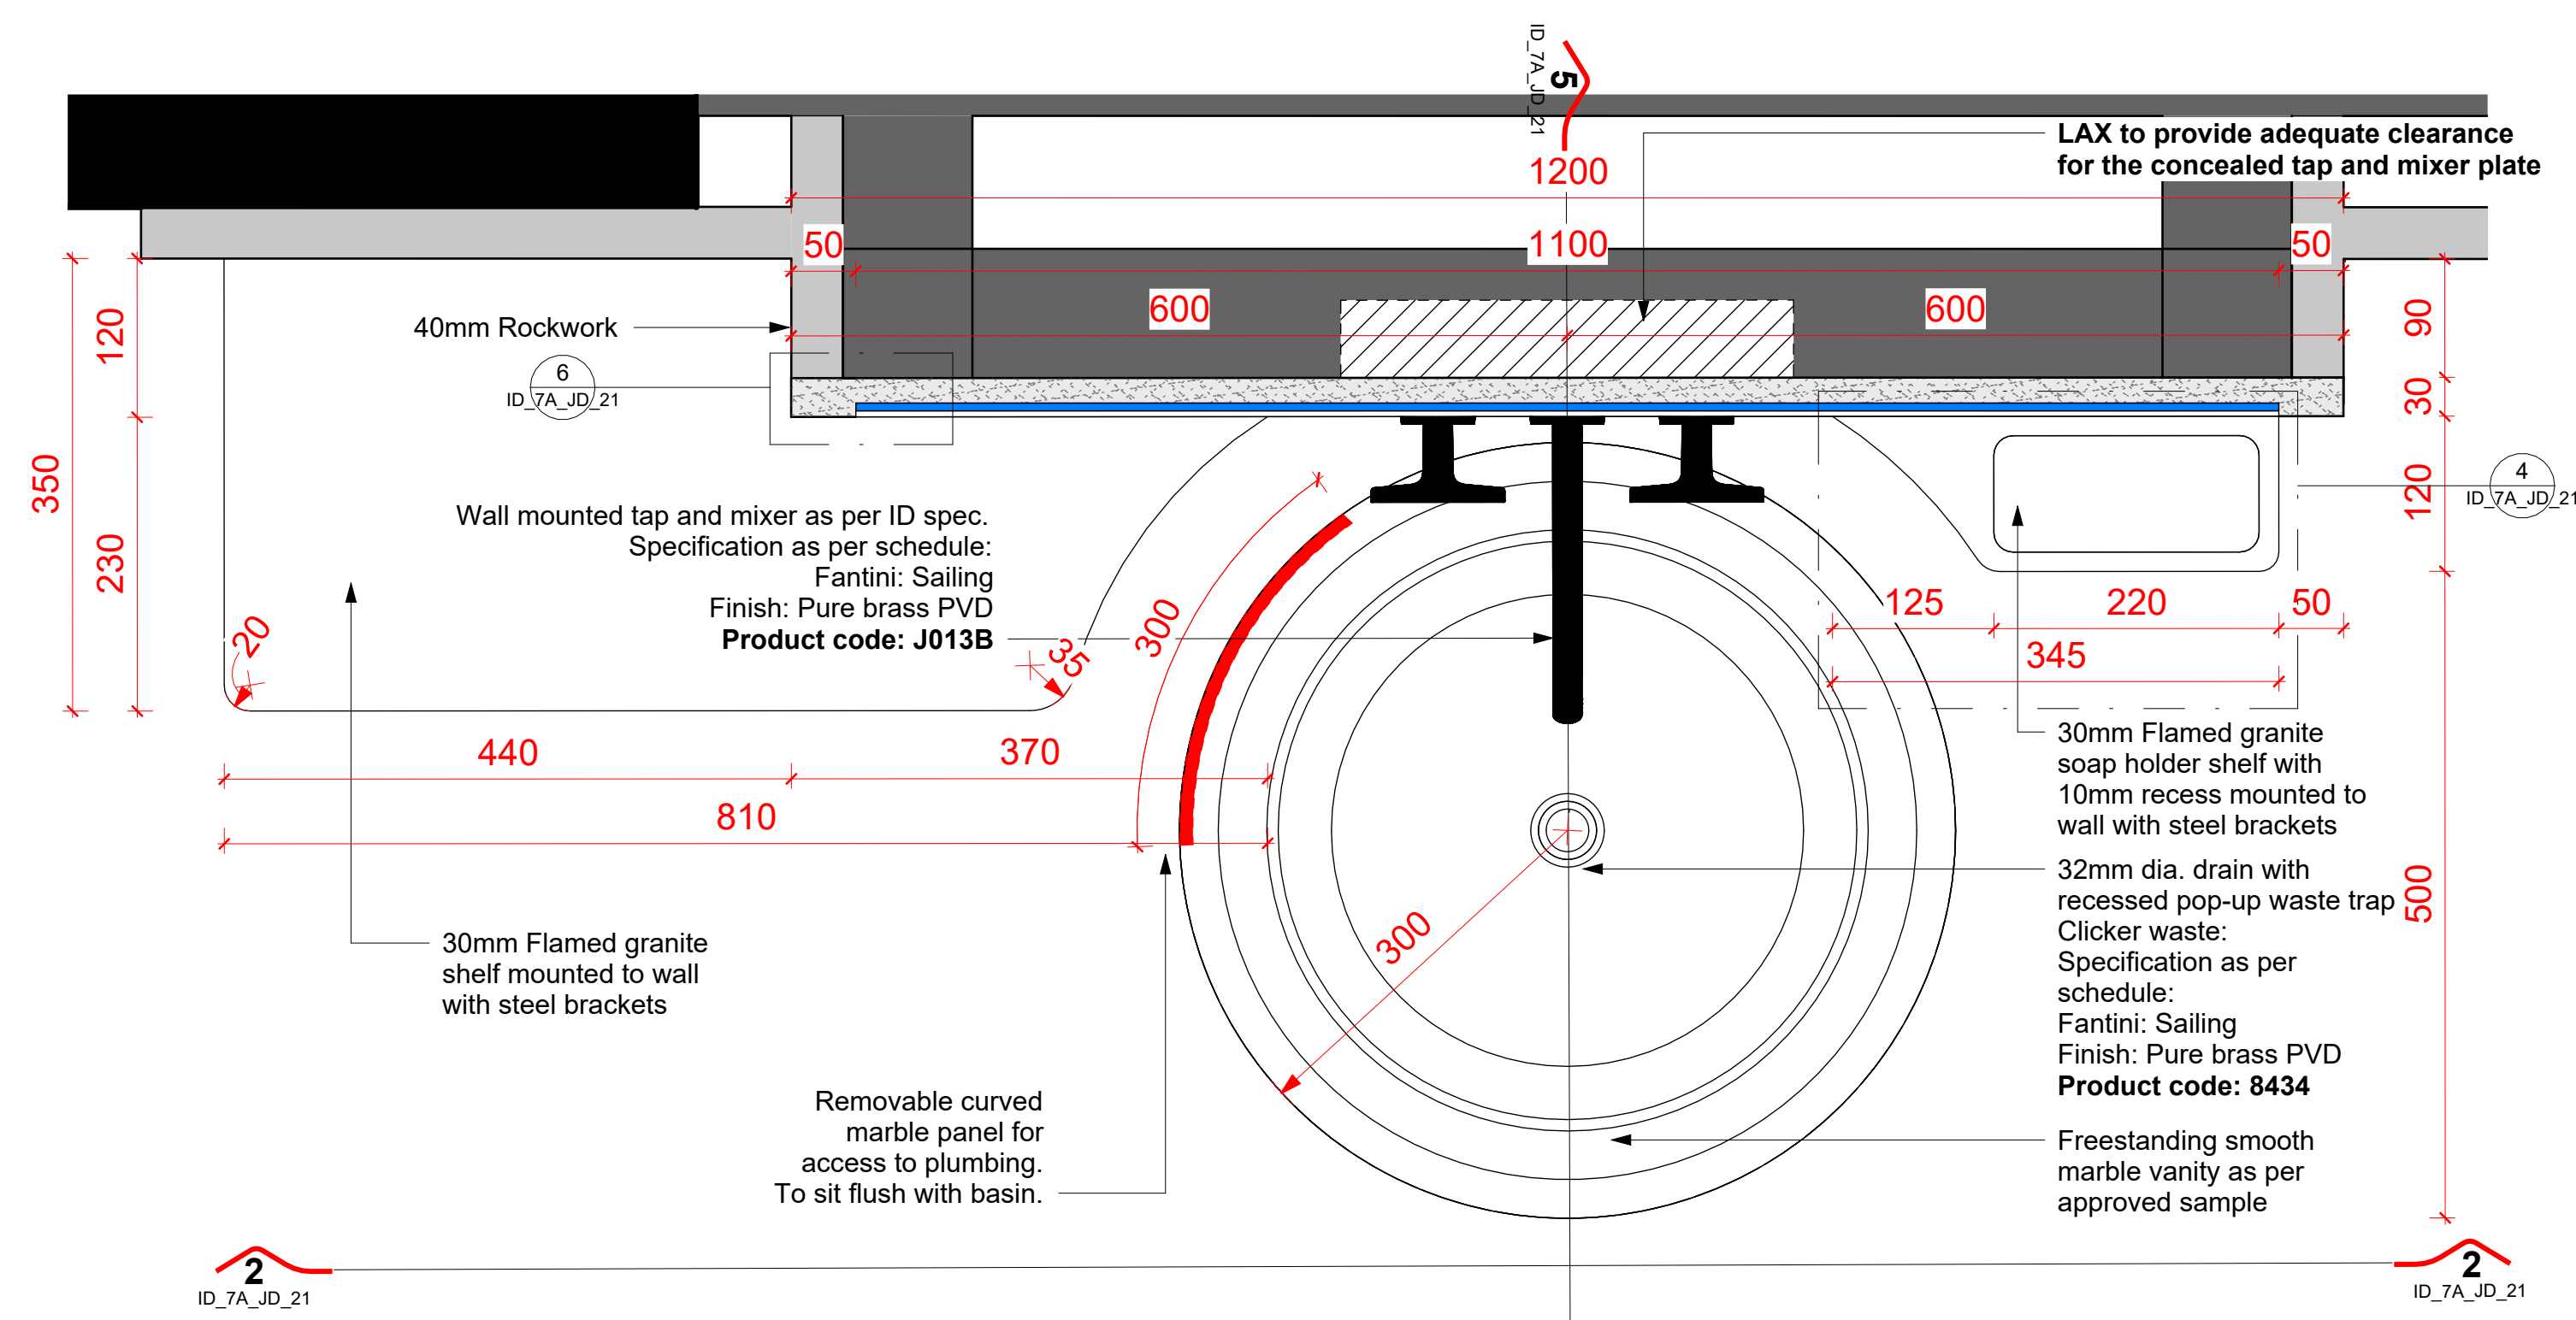


Tap & Mixer  
Fantini: Sailing

Finish: Pure brass PVD  
Product code: J013B

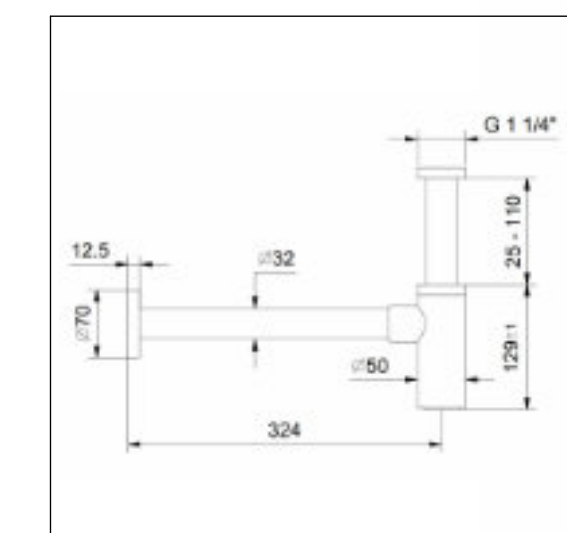

Bottle Trap  
Fantini: Sailing  
Finish: Pure brass PVD  
Product code: 9234

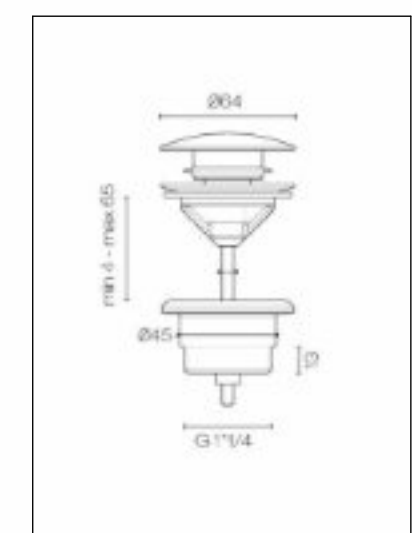

Clicker Waste  
Fantini: Sailing  
Finish: Pure brass PVD  
Product code: 8434

## gym freestanding basin