




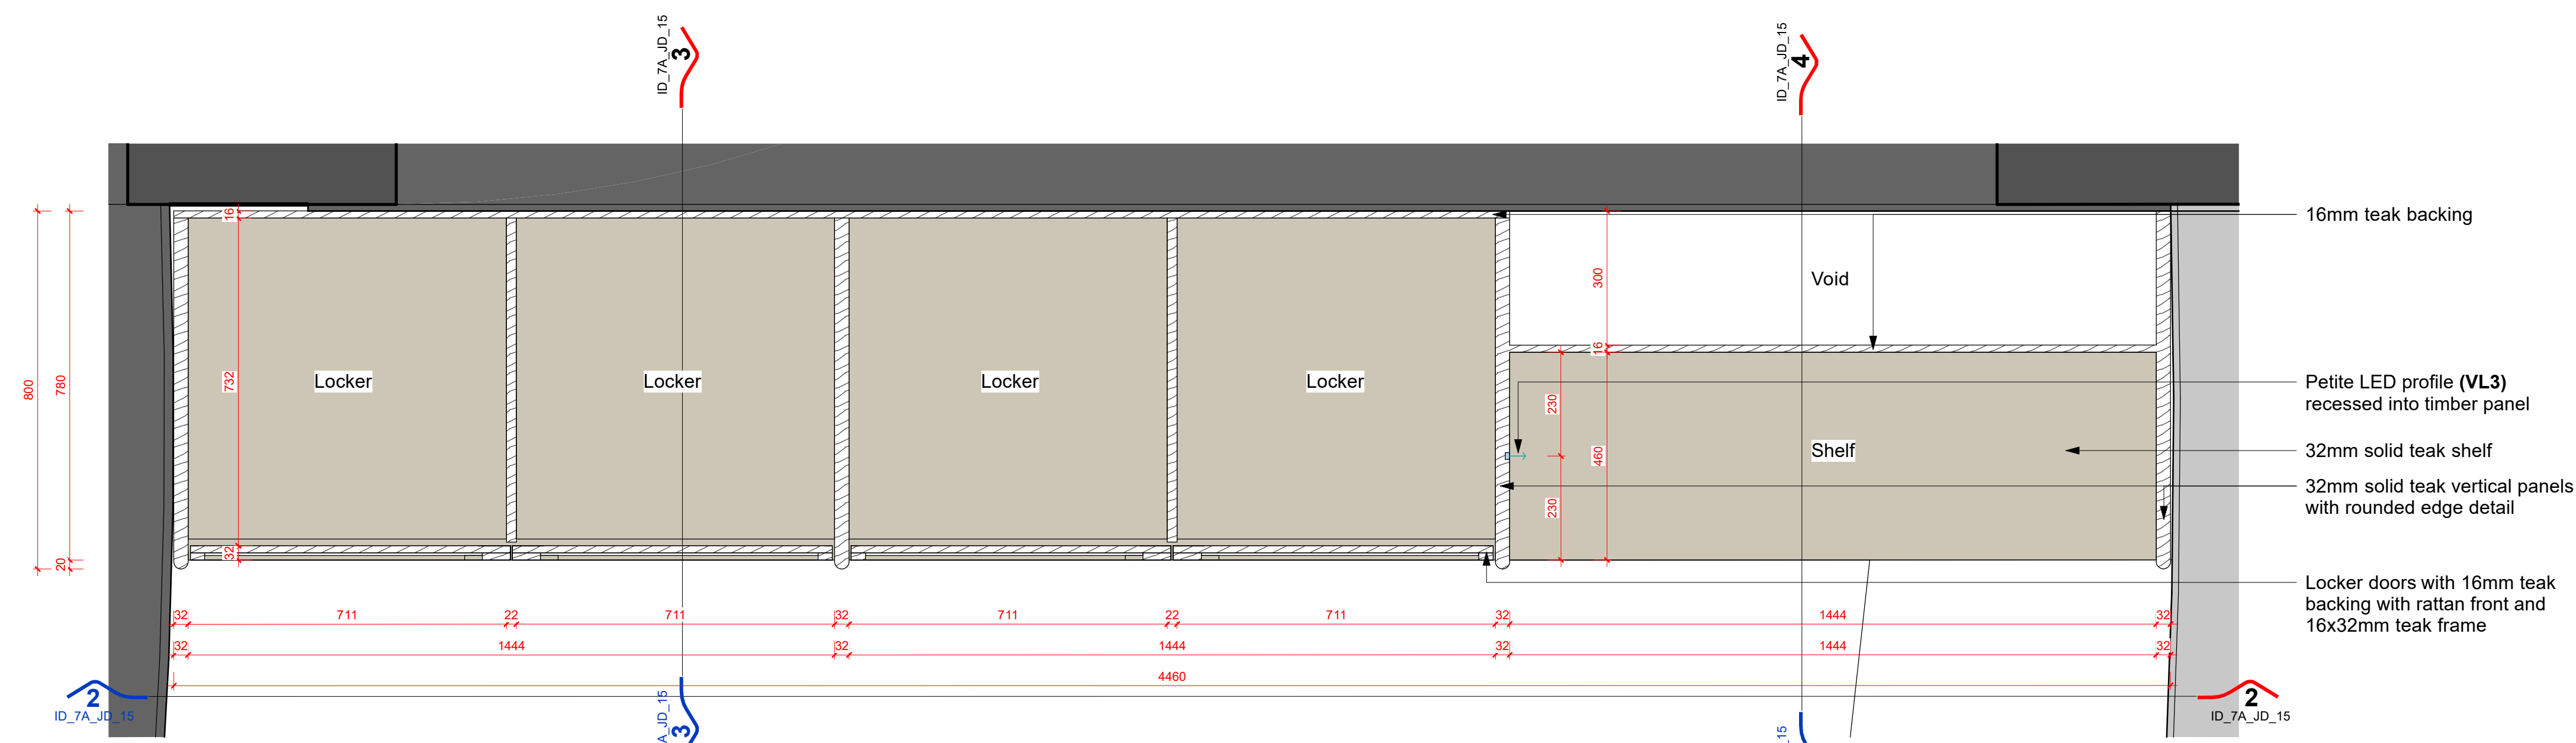


Floor Plan Upper Level - Lockers & Shelf | 1:10

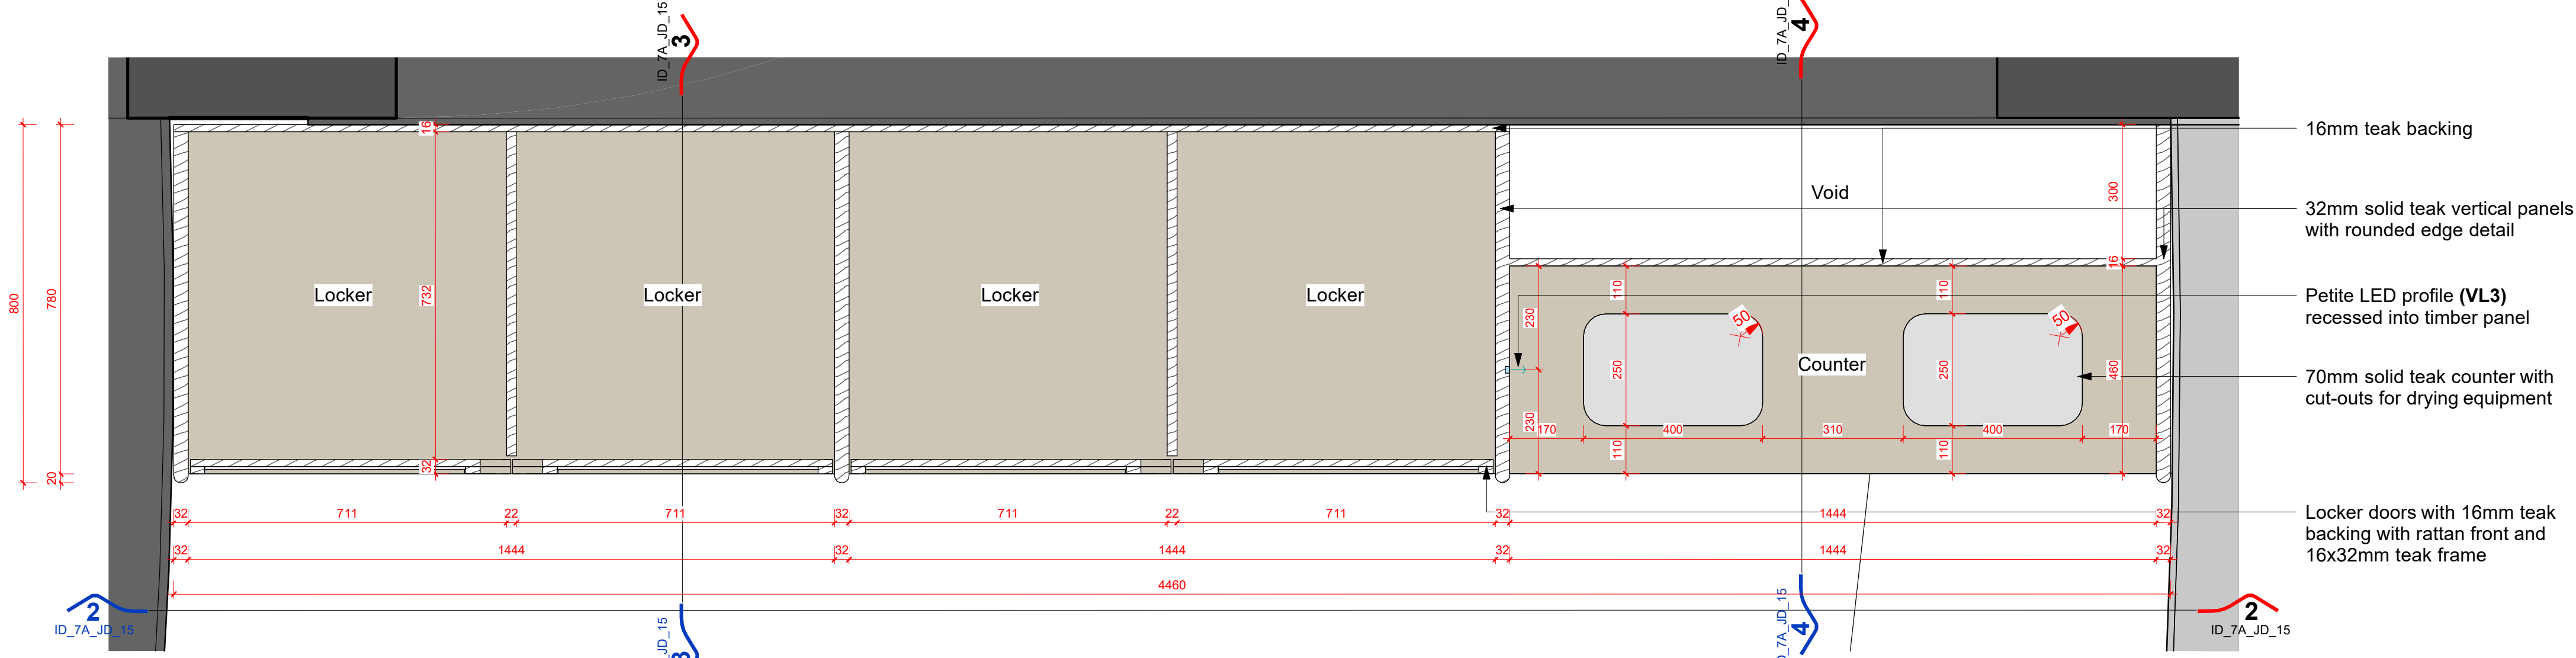


Floor Plan Lower Level - Lockers & Shelf | 1:10

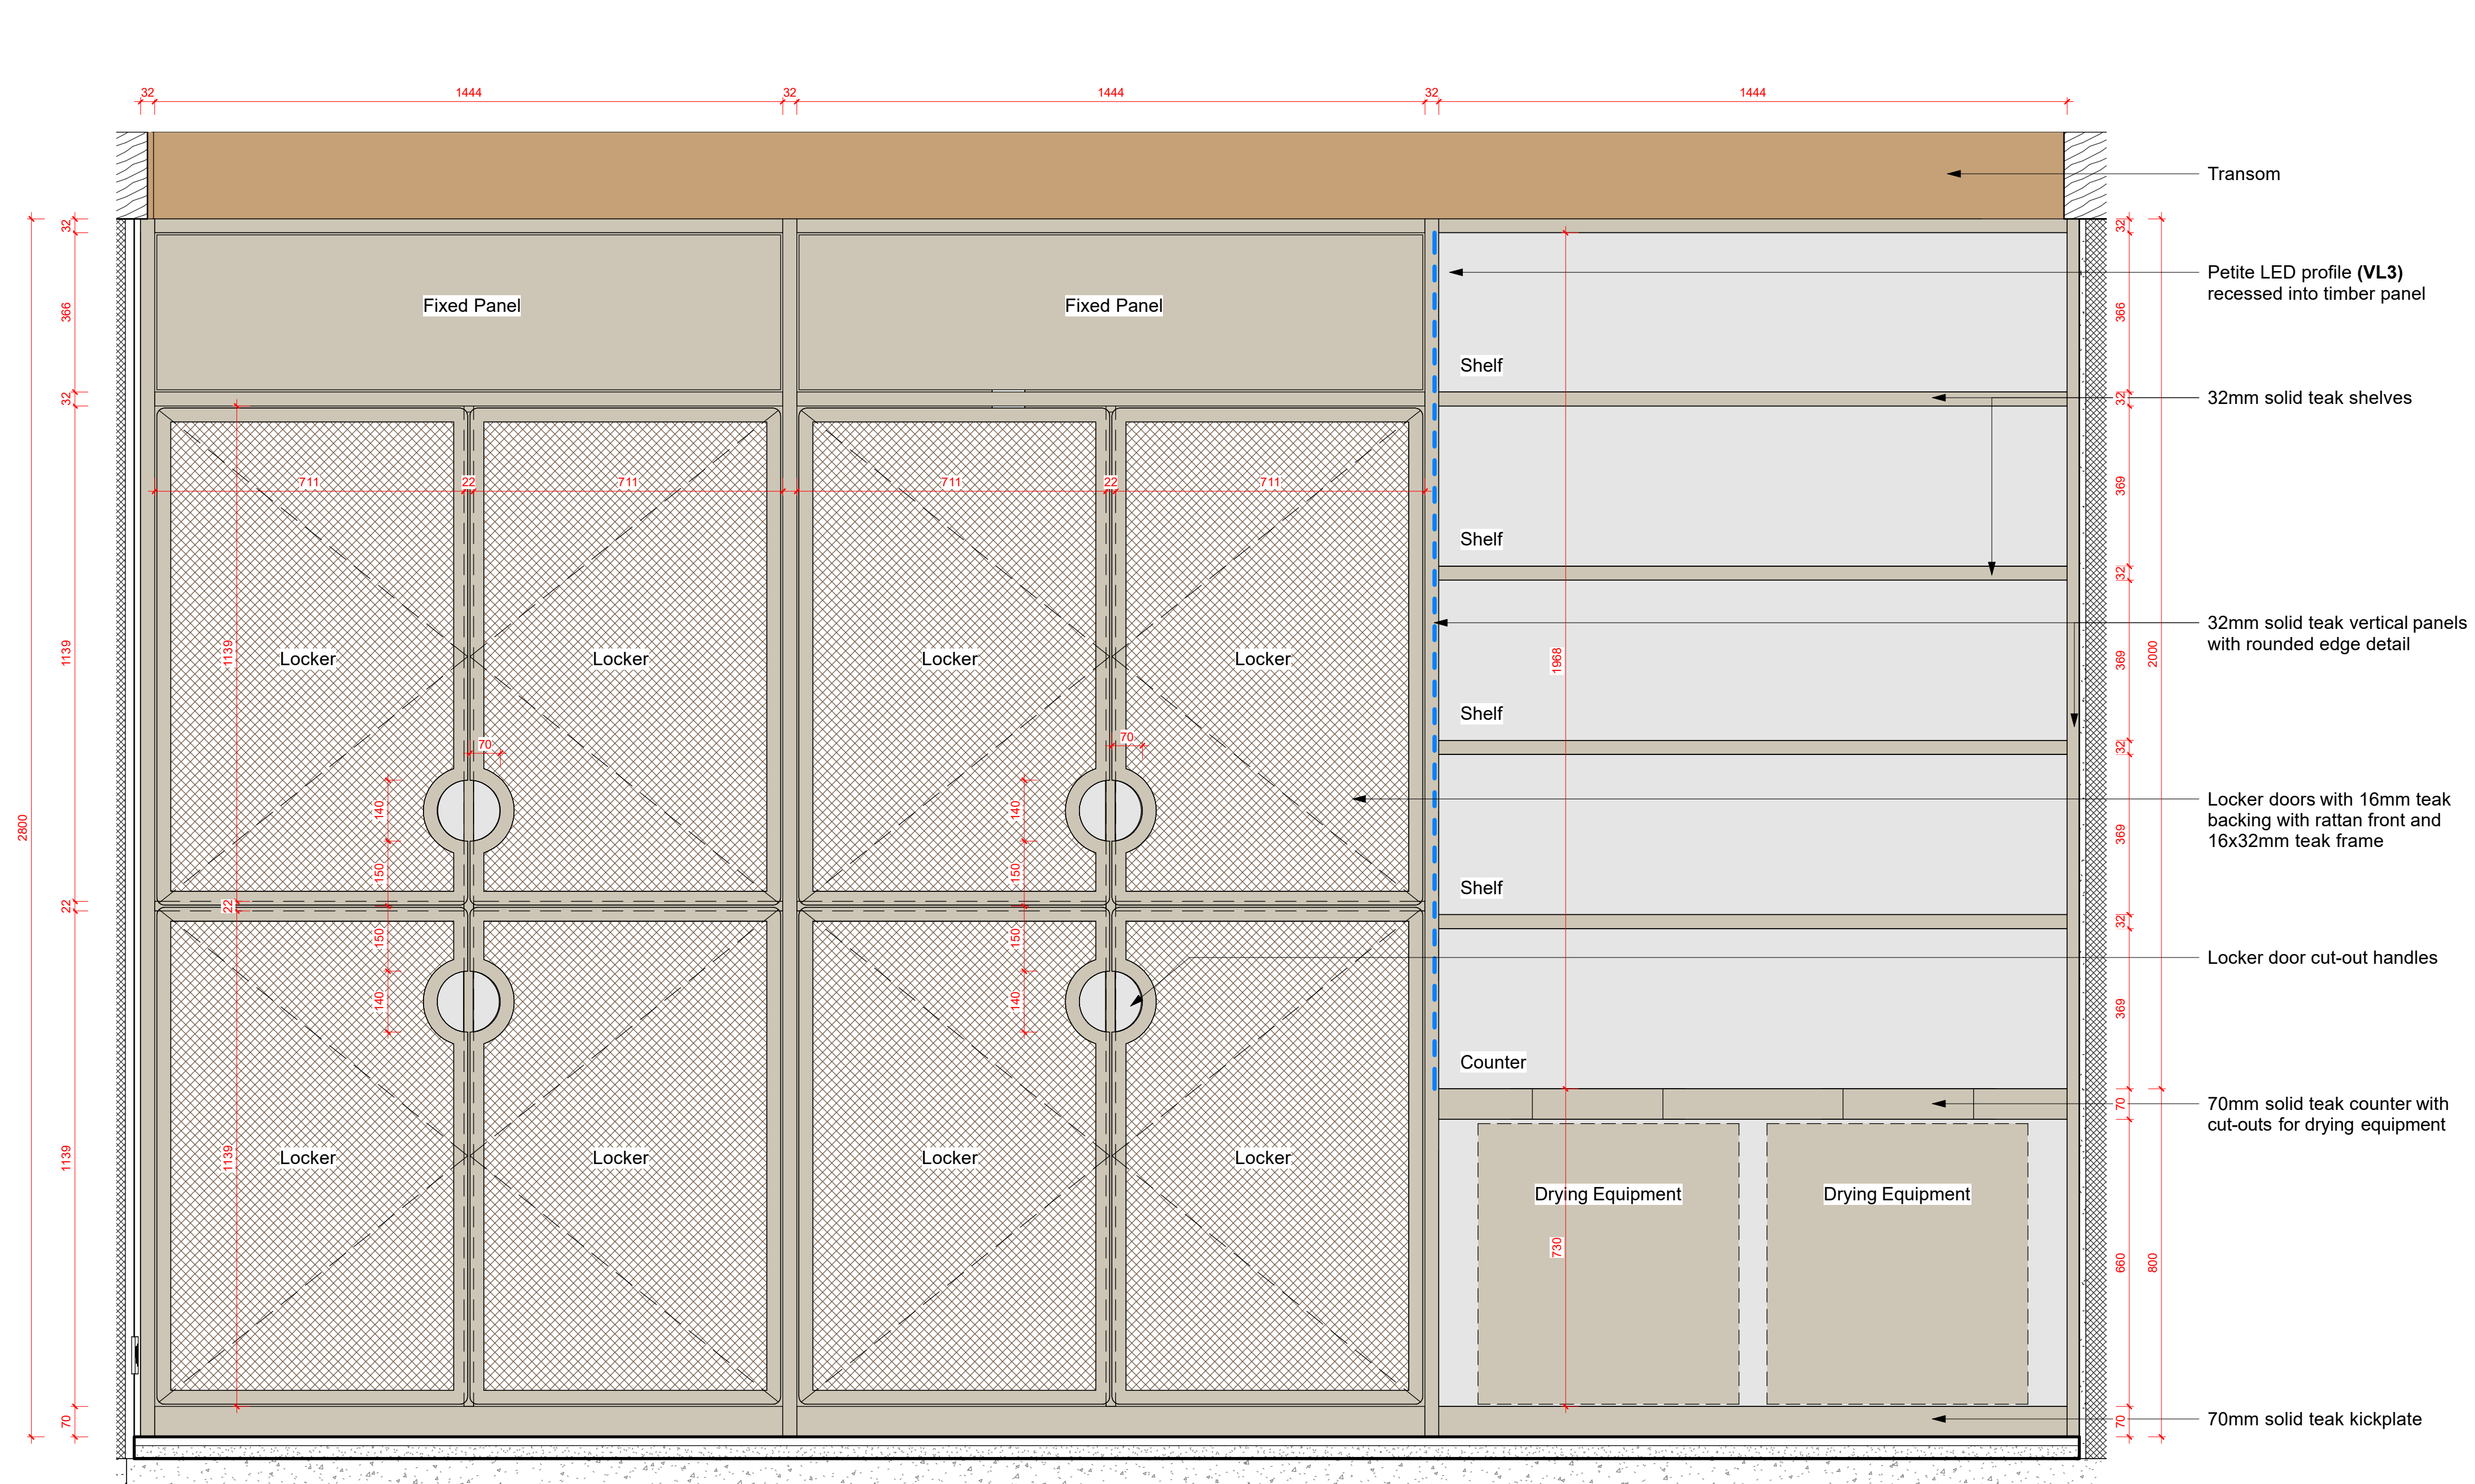


Front Elevation - Lockers & Shelf | 1:10

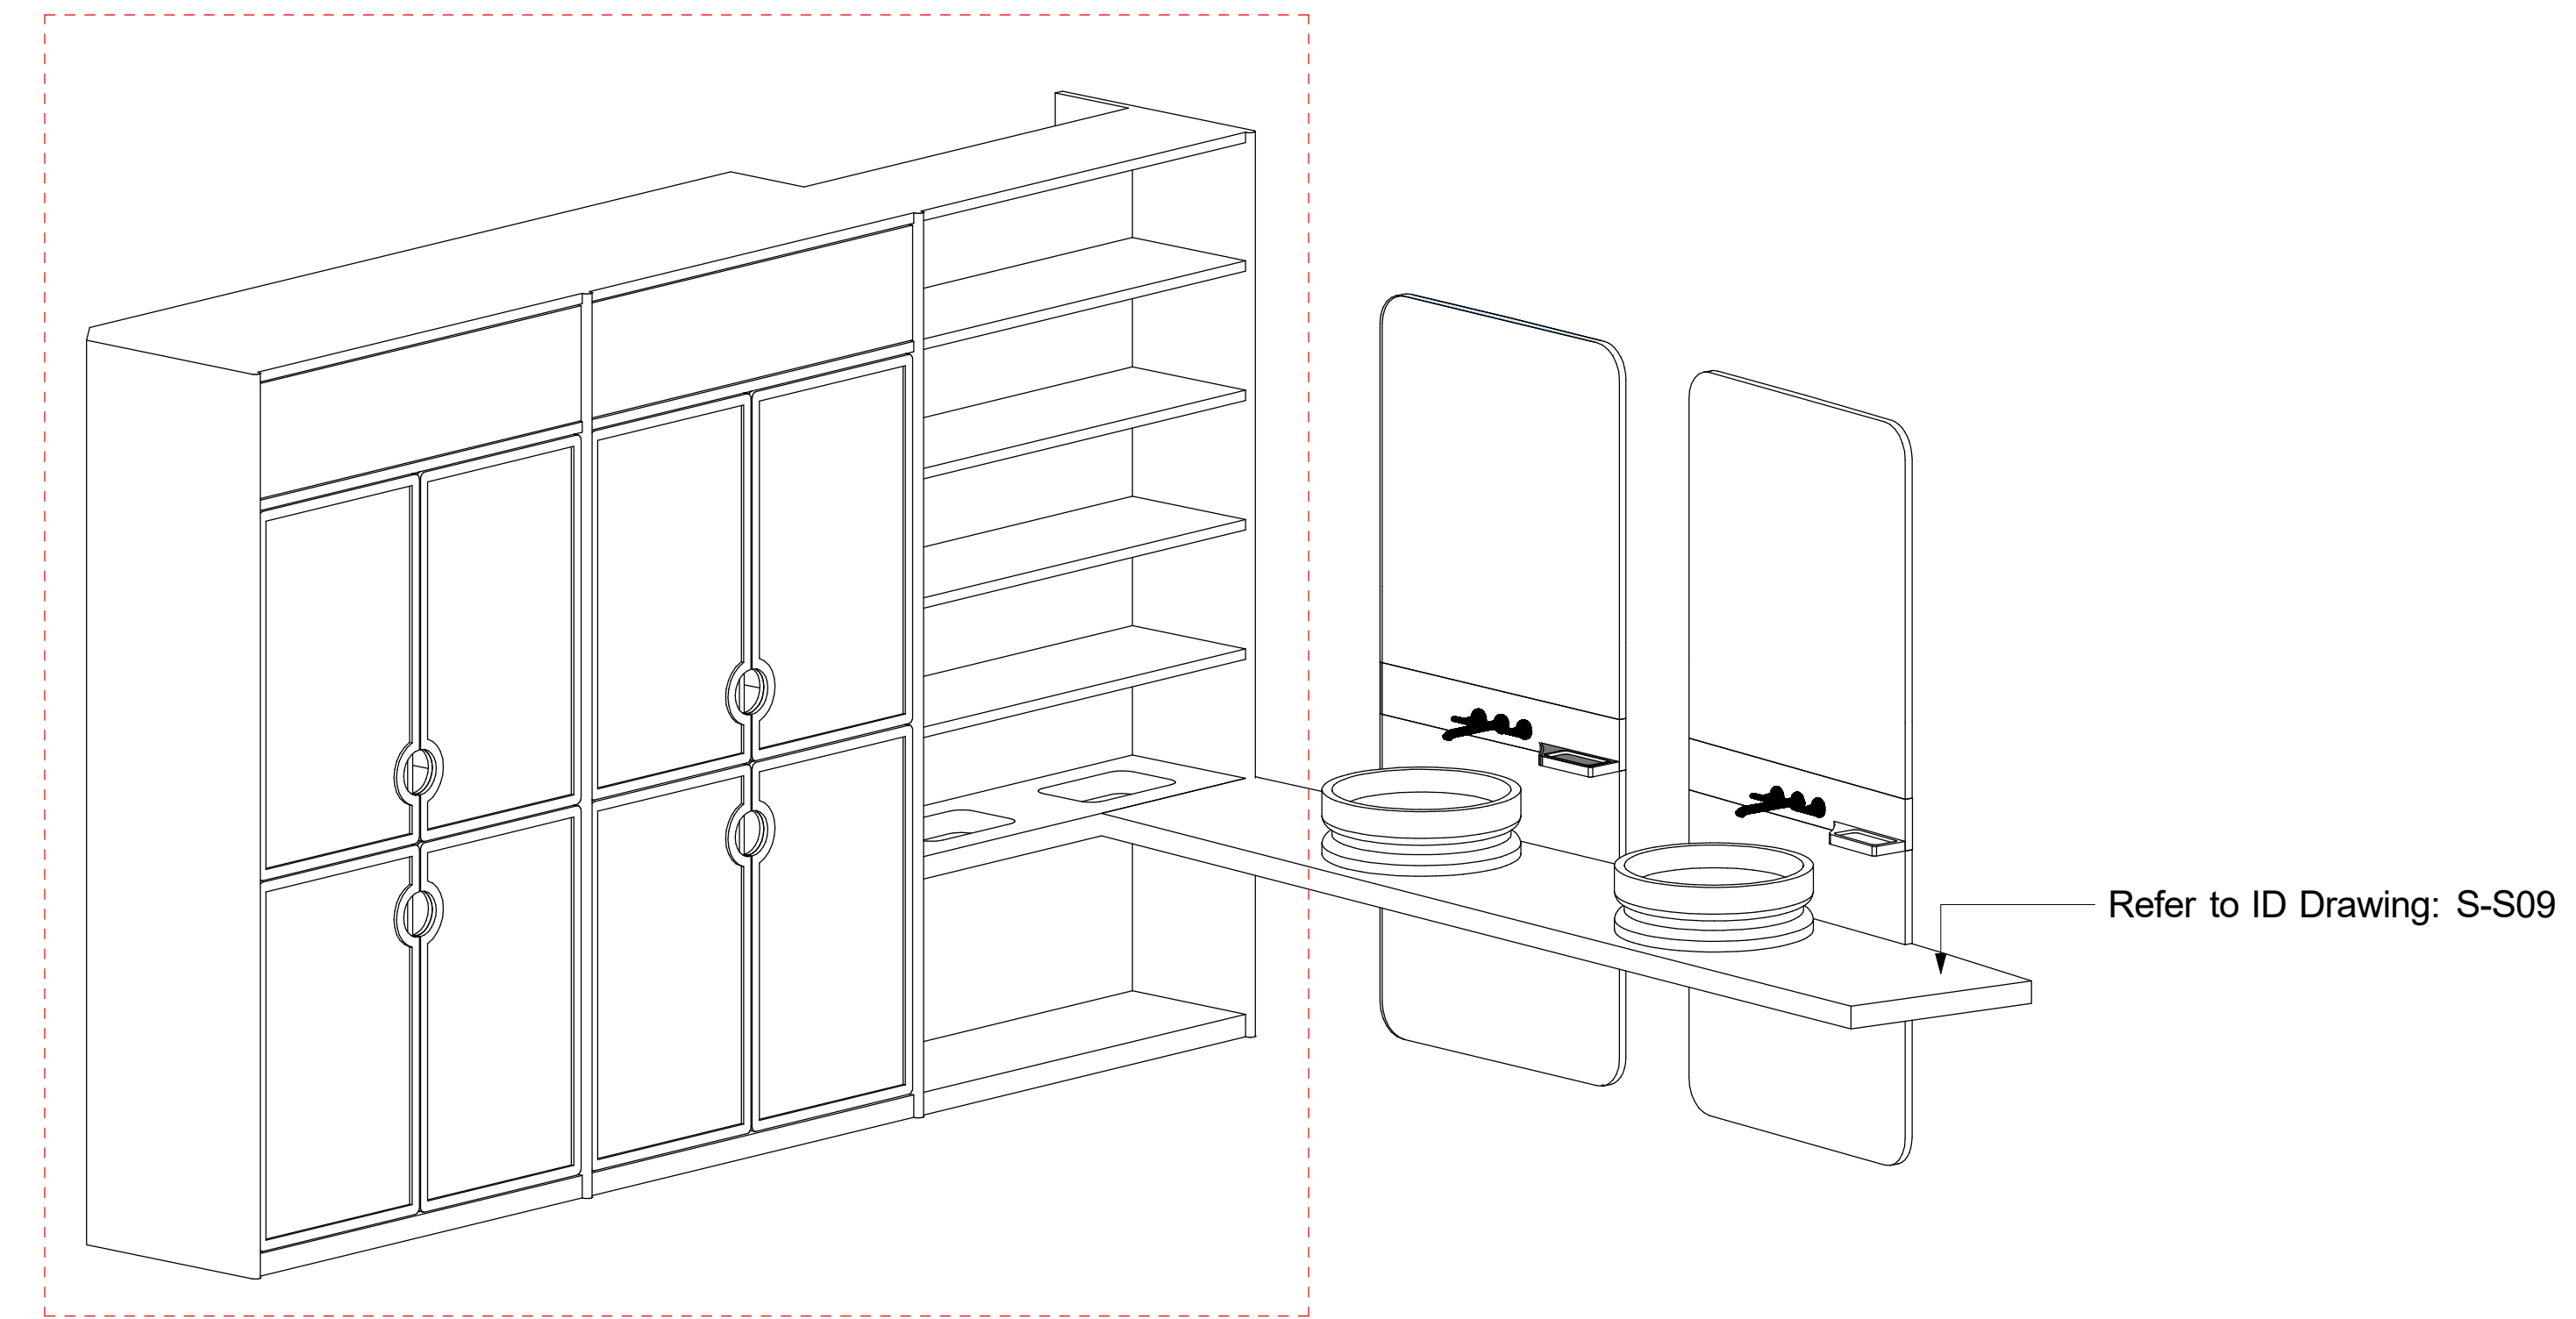

3D View - Vanity, Lockers & Shelf | 1:20

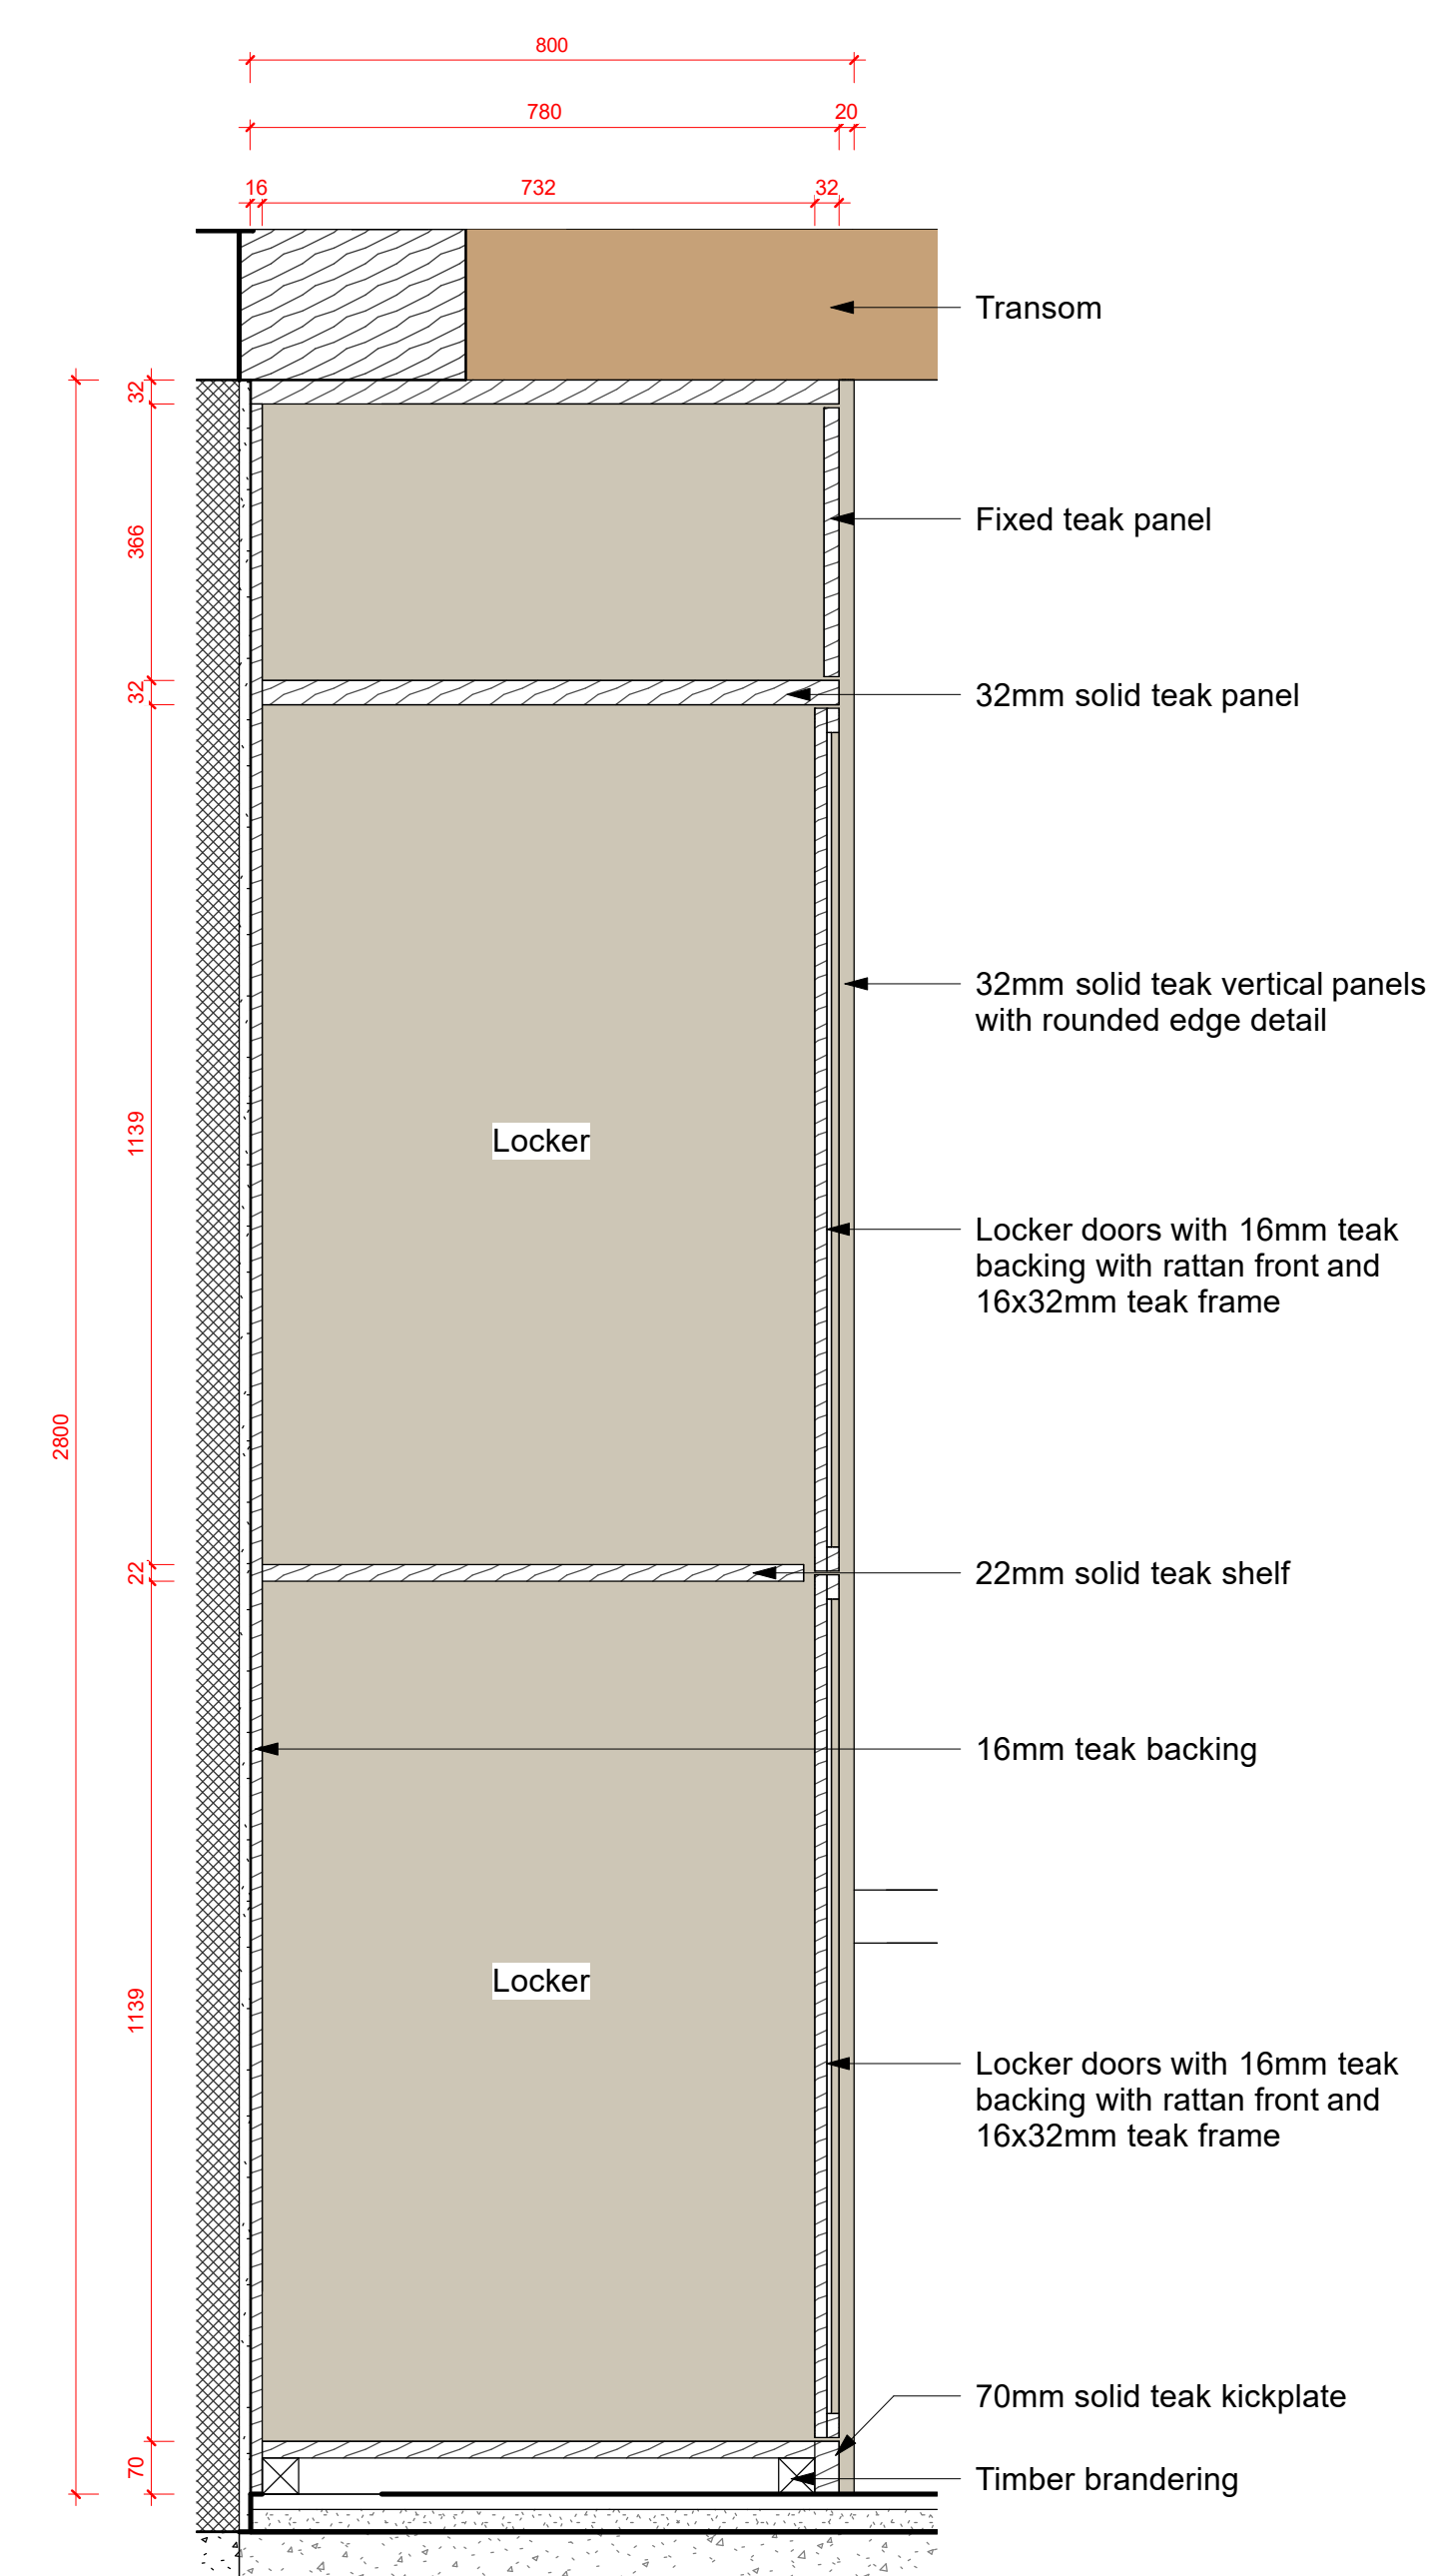

Section - Lockers | 1:10

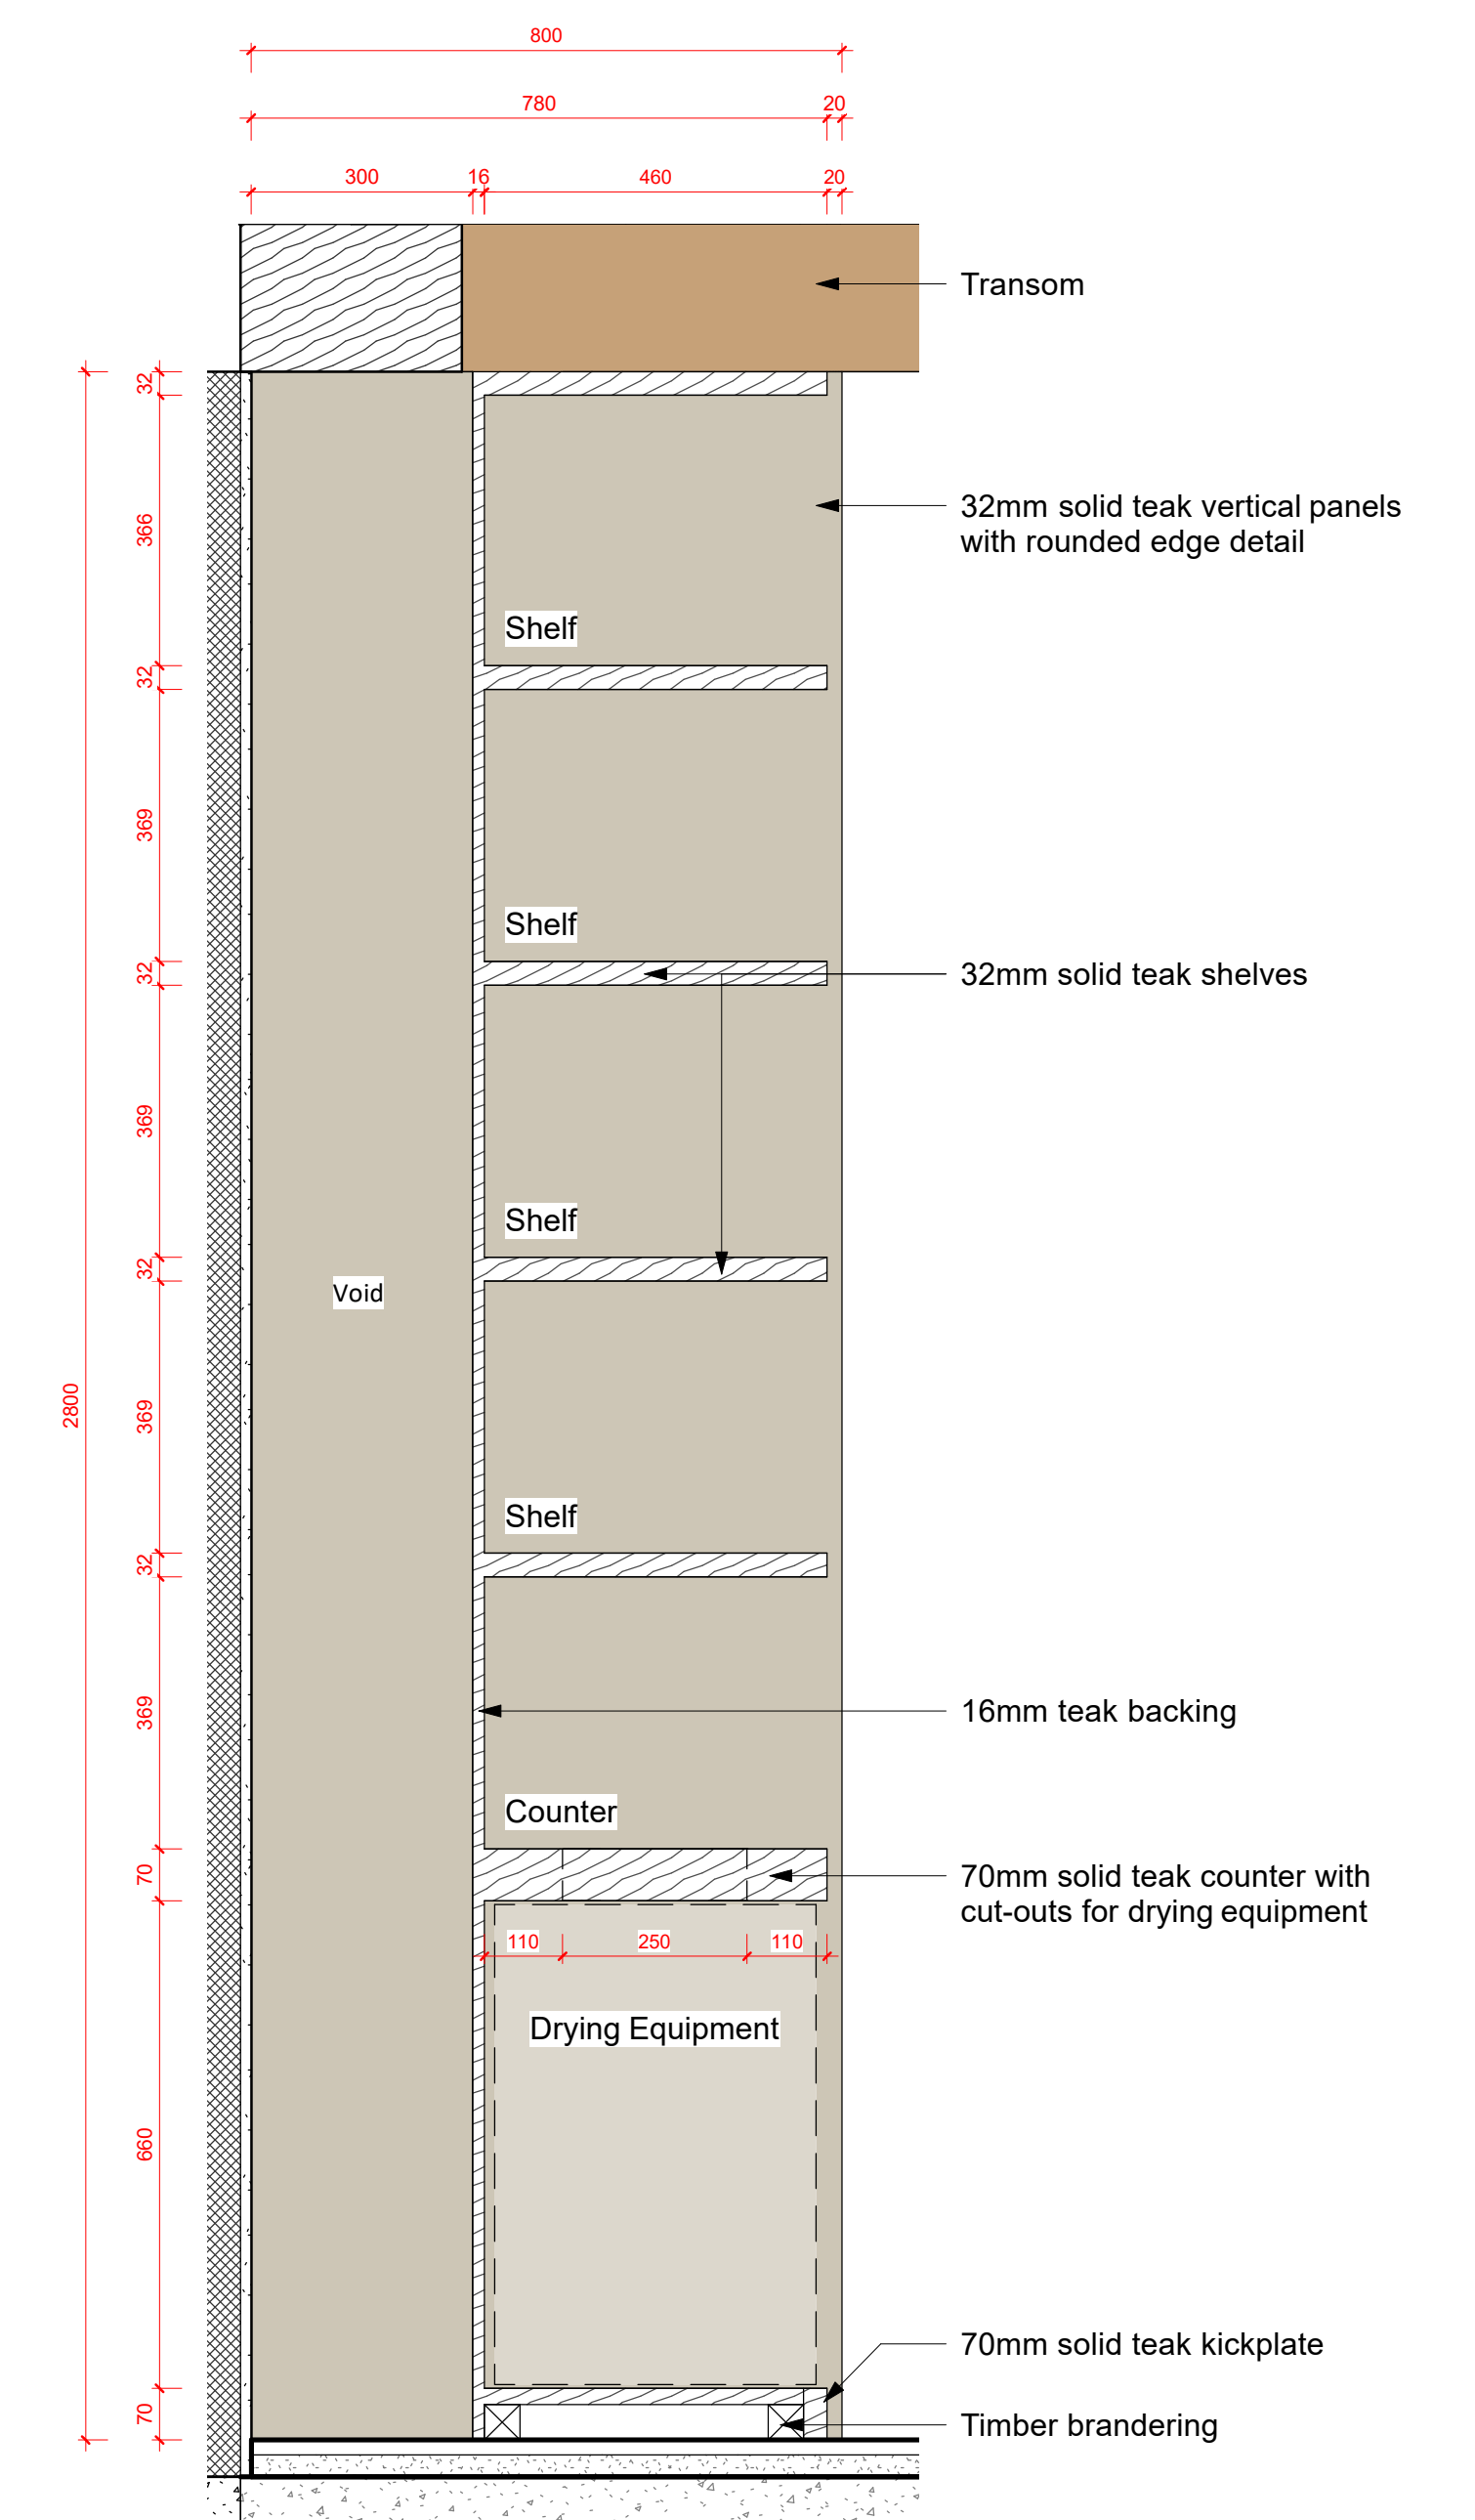

Section - Shelves | 1:10

relaxation area lockers