




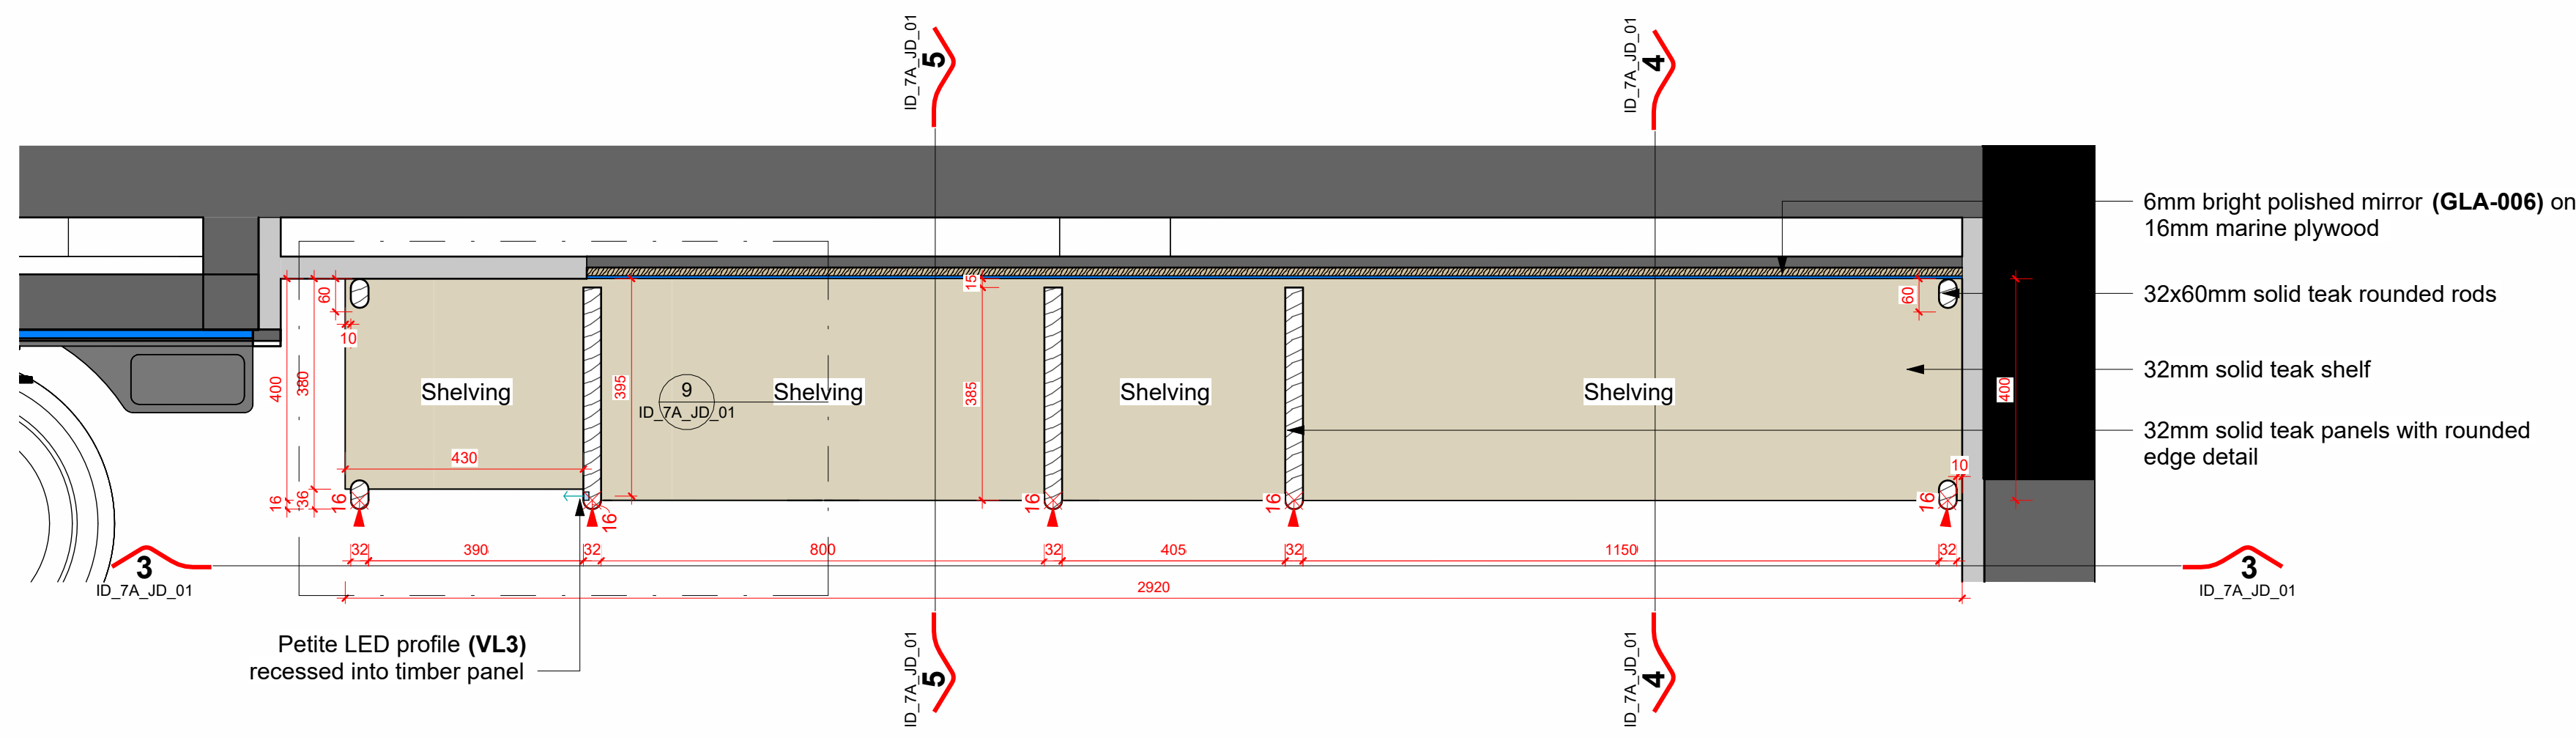


Floor Plan Upper View - Lockers | 1:10

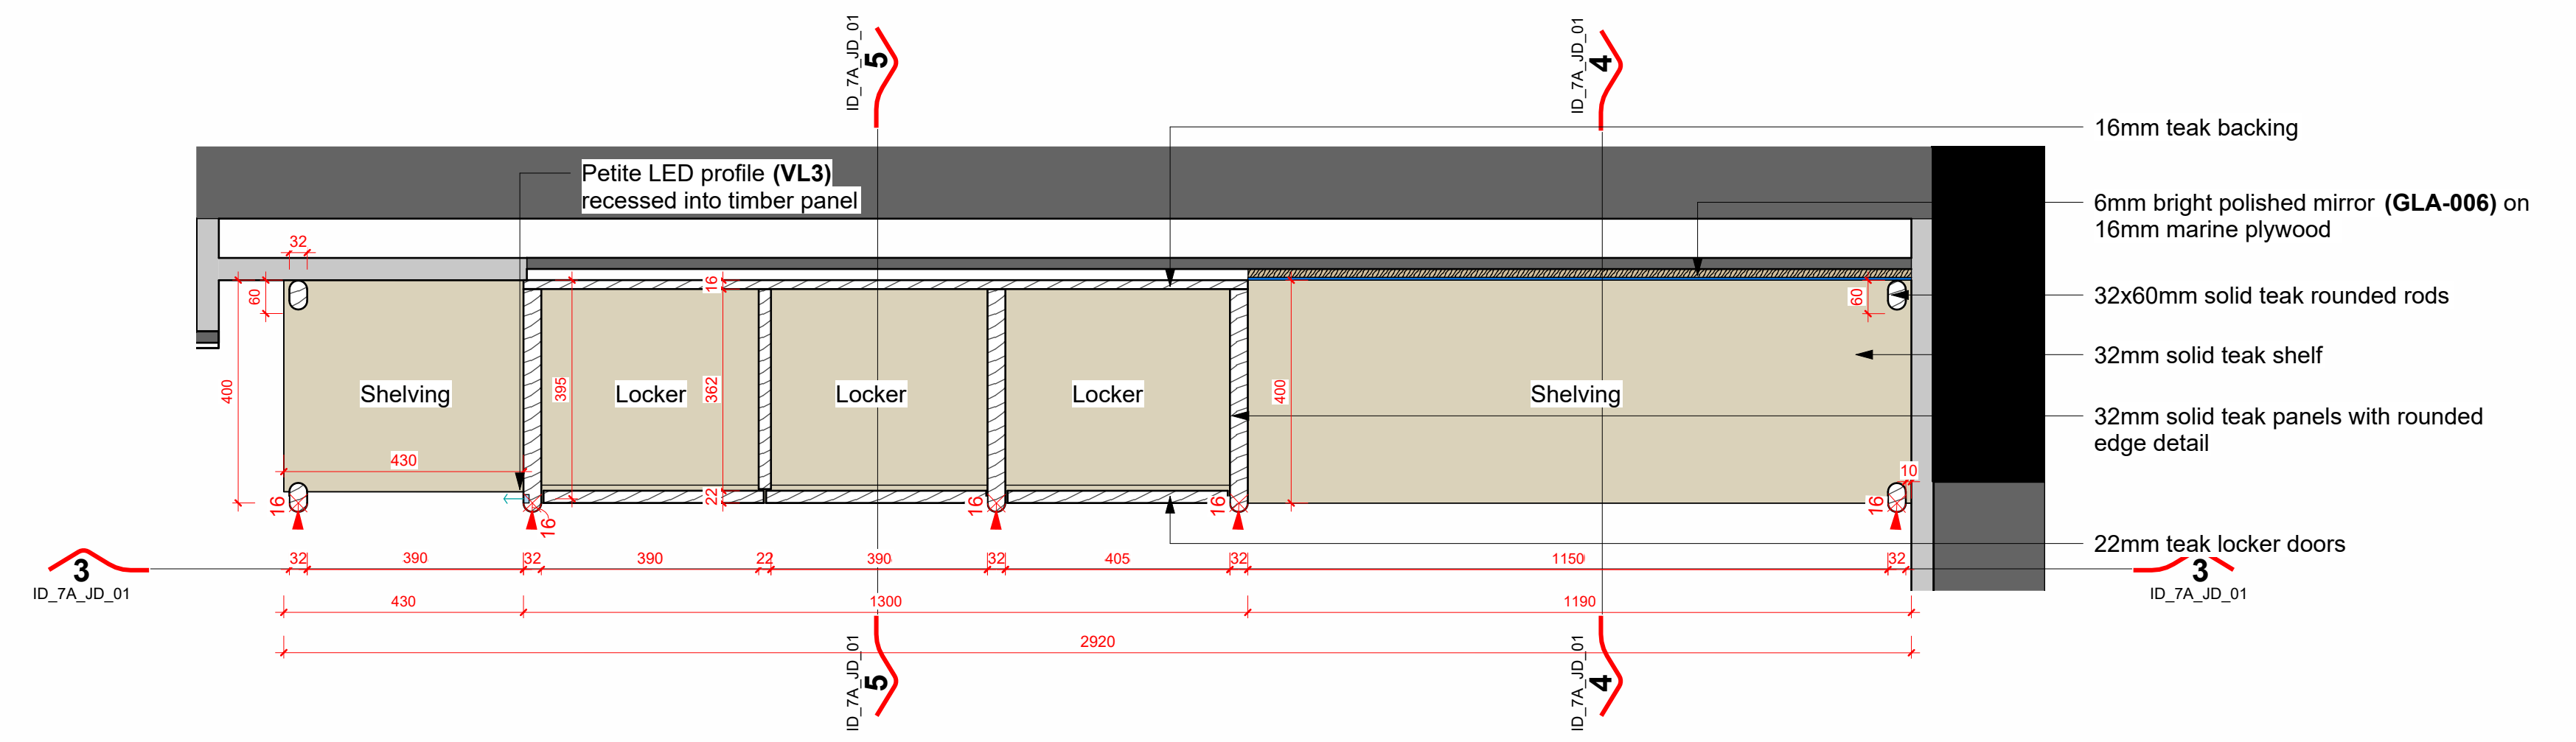


Floor Plan Lower View - Lockers | 1:10

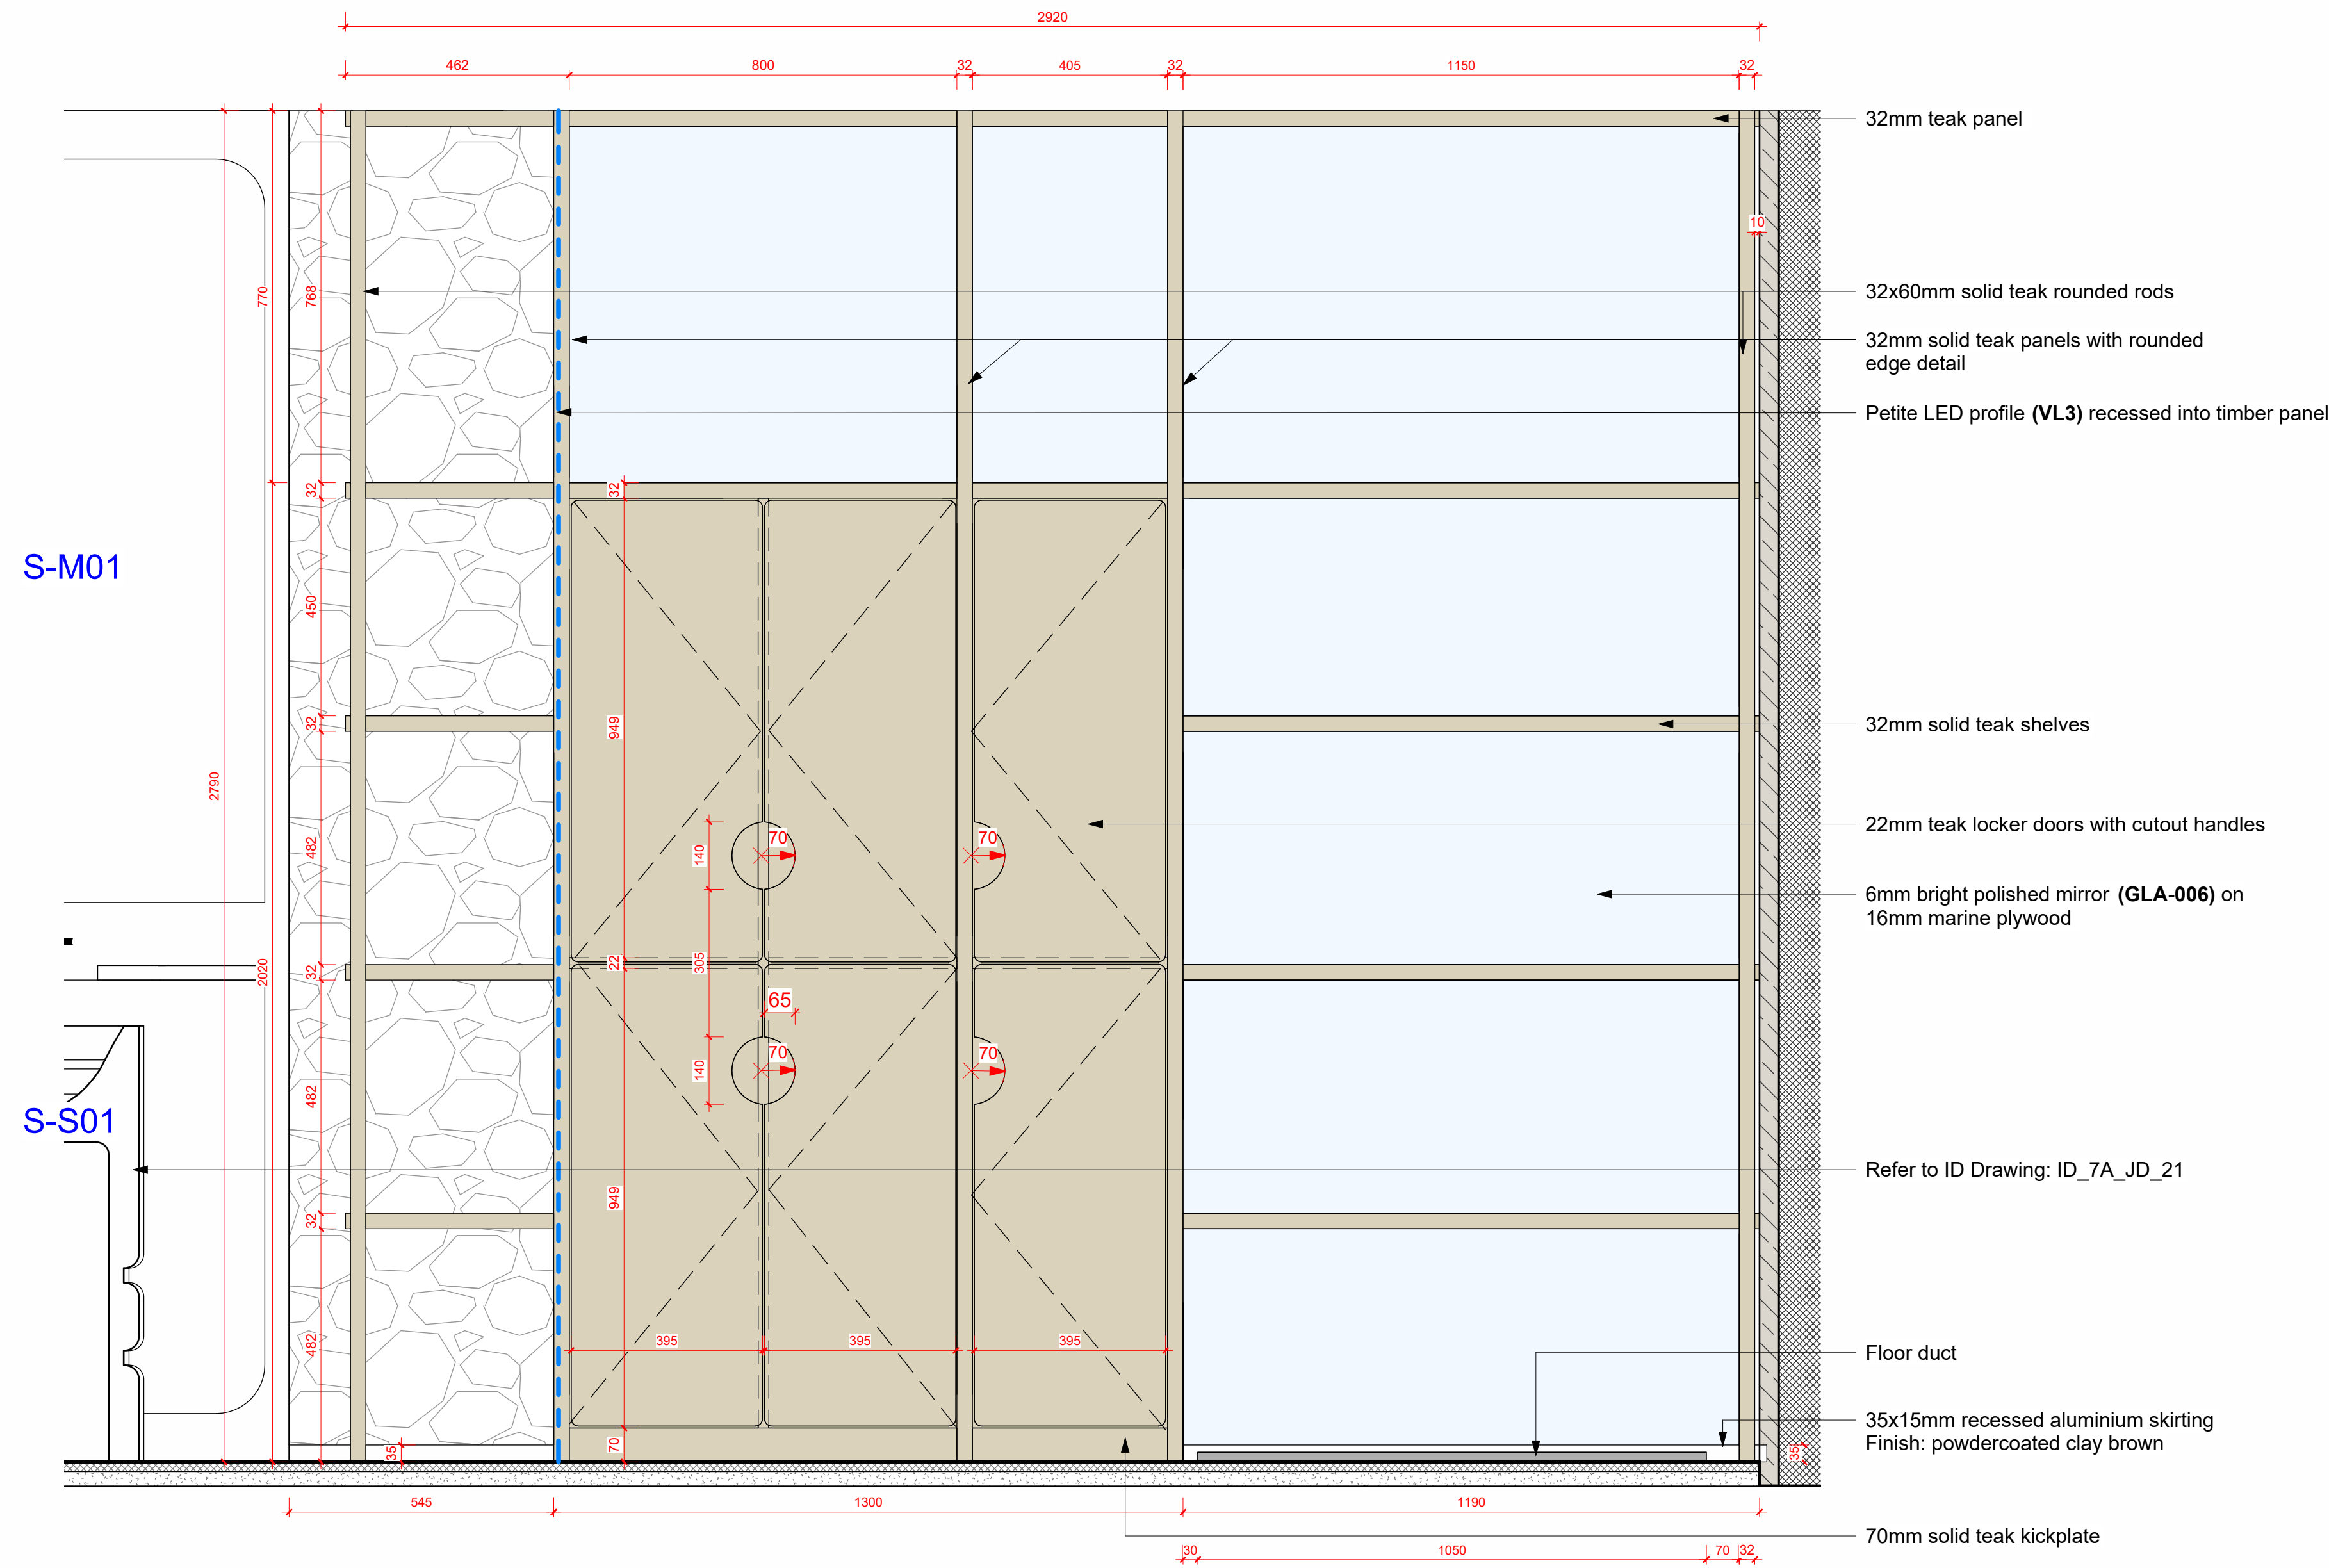


Front Elevation - Lockers | 1:10

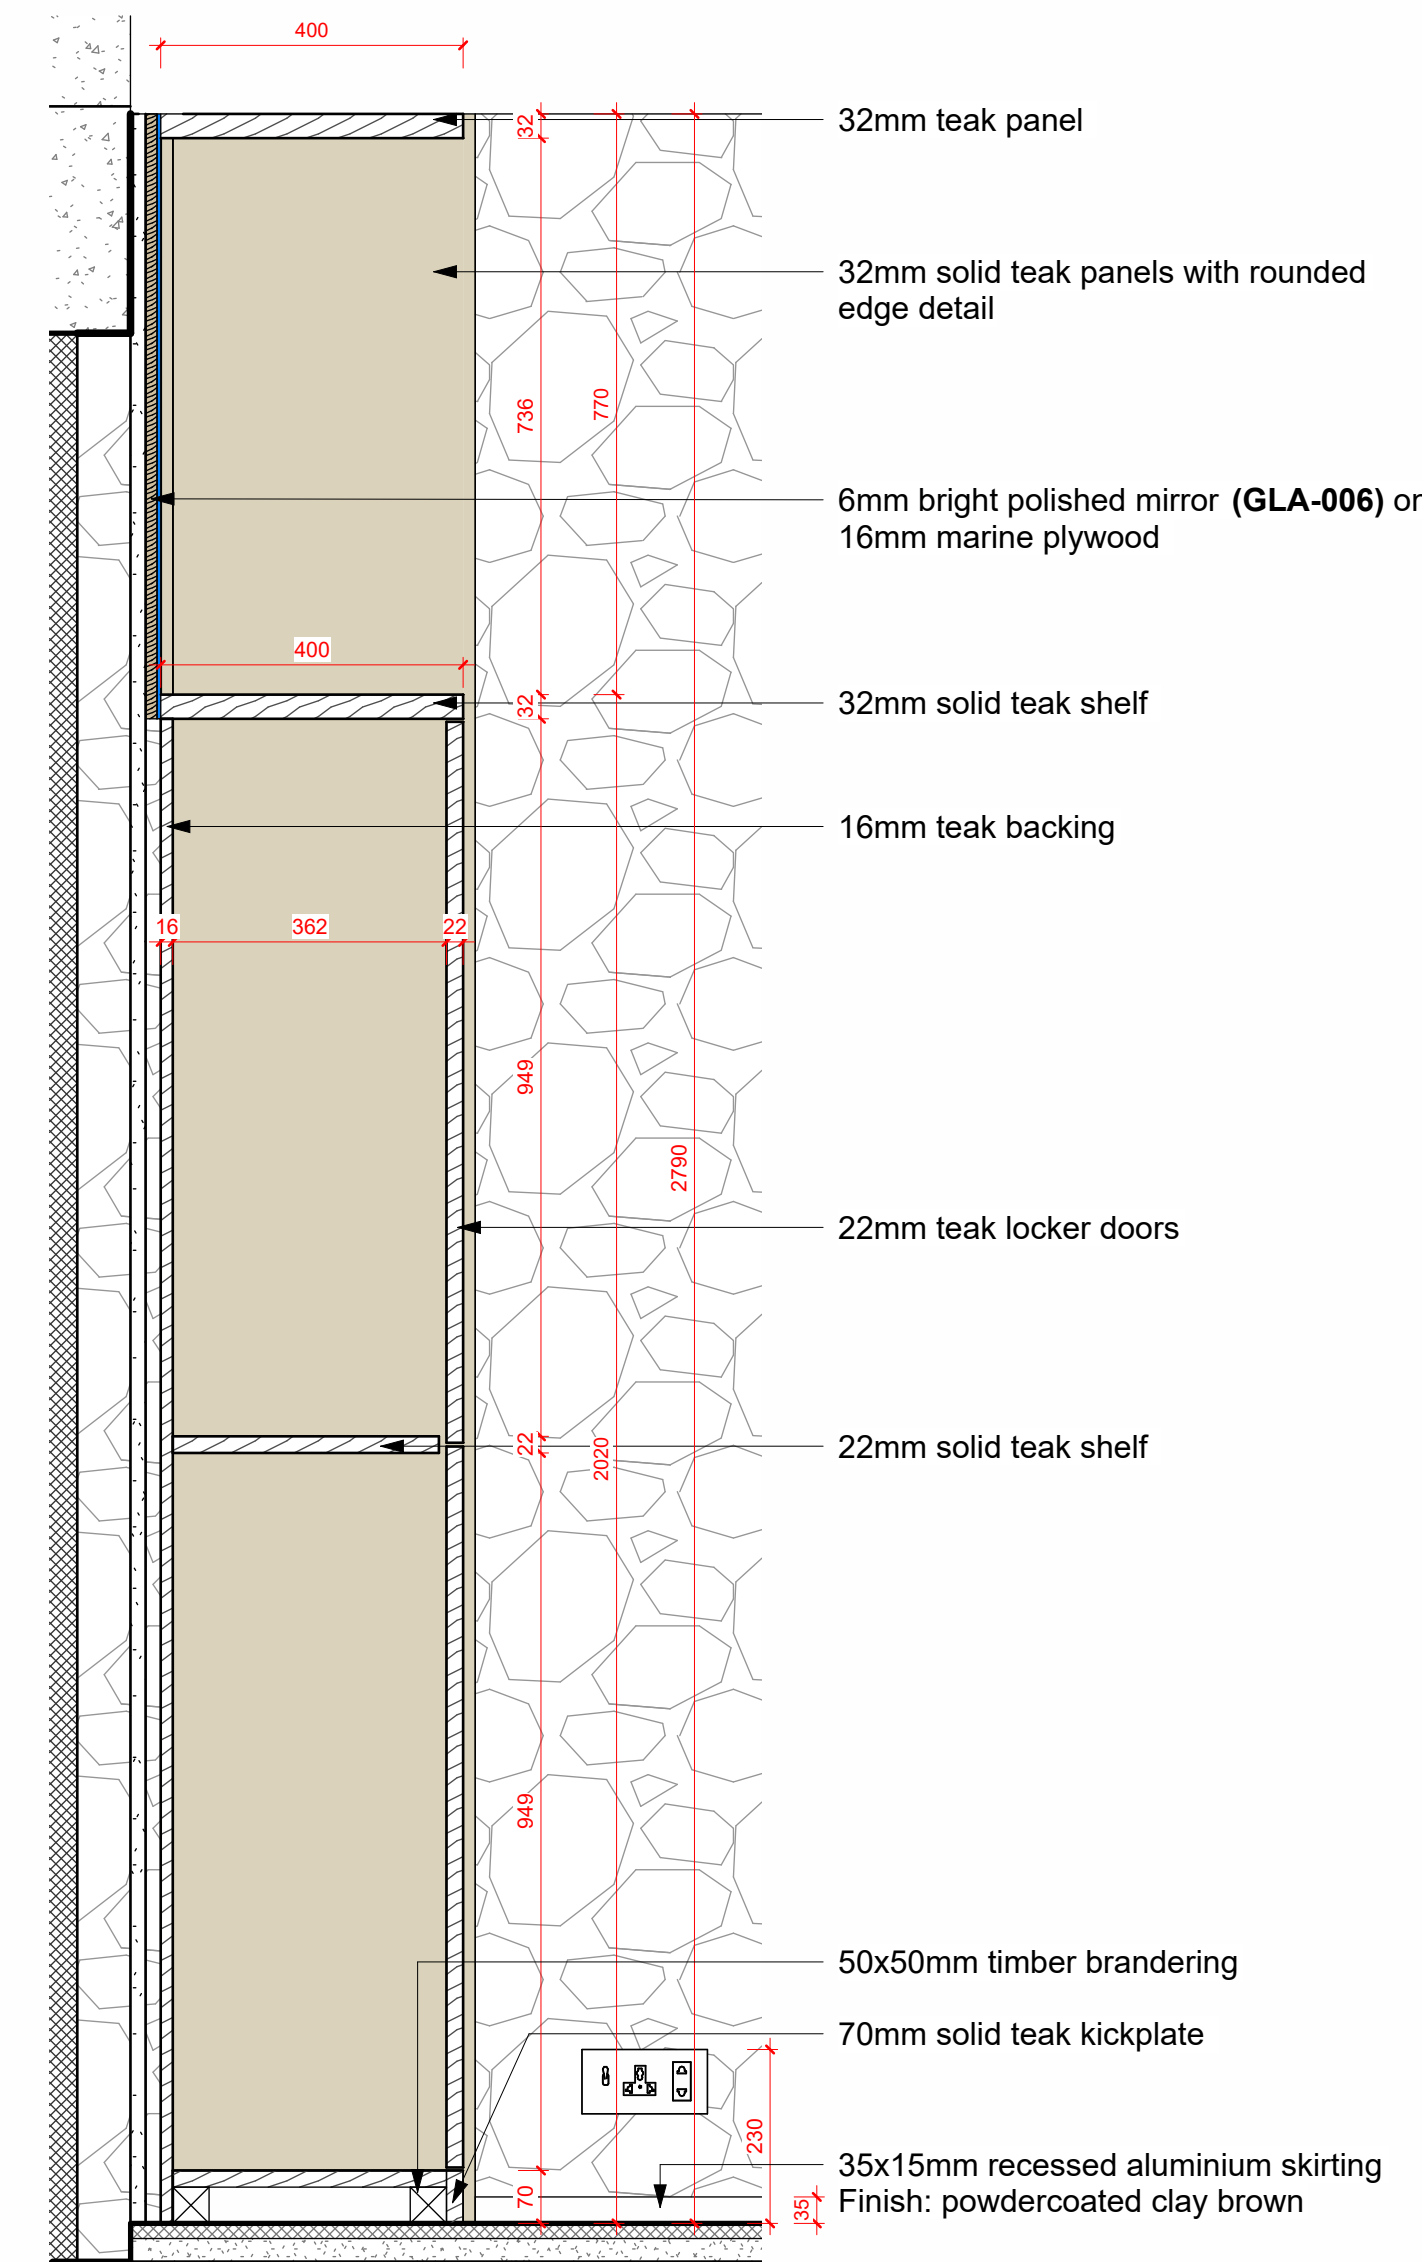


Section - Locker Cupboards | 1:10

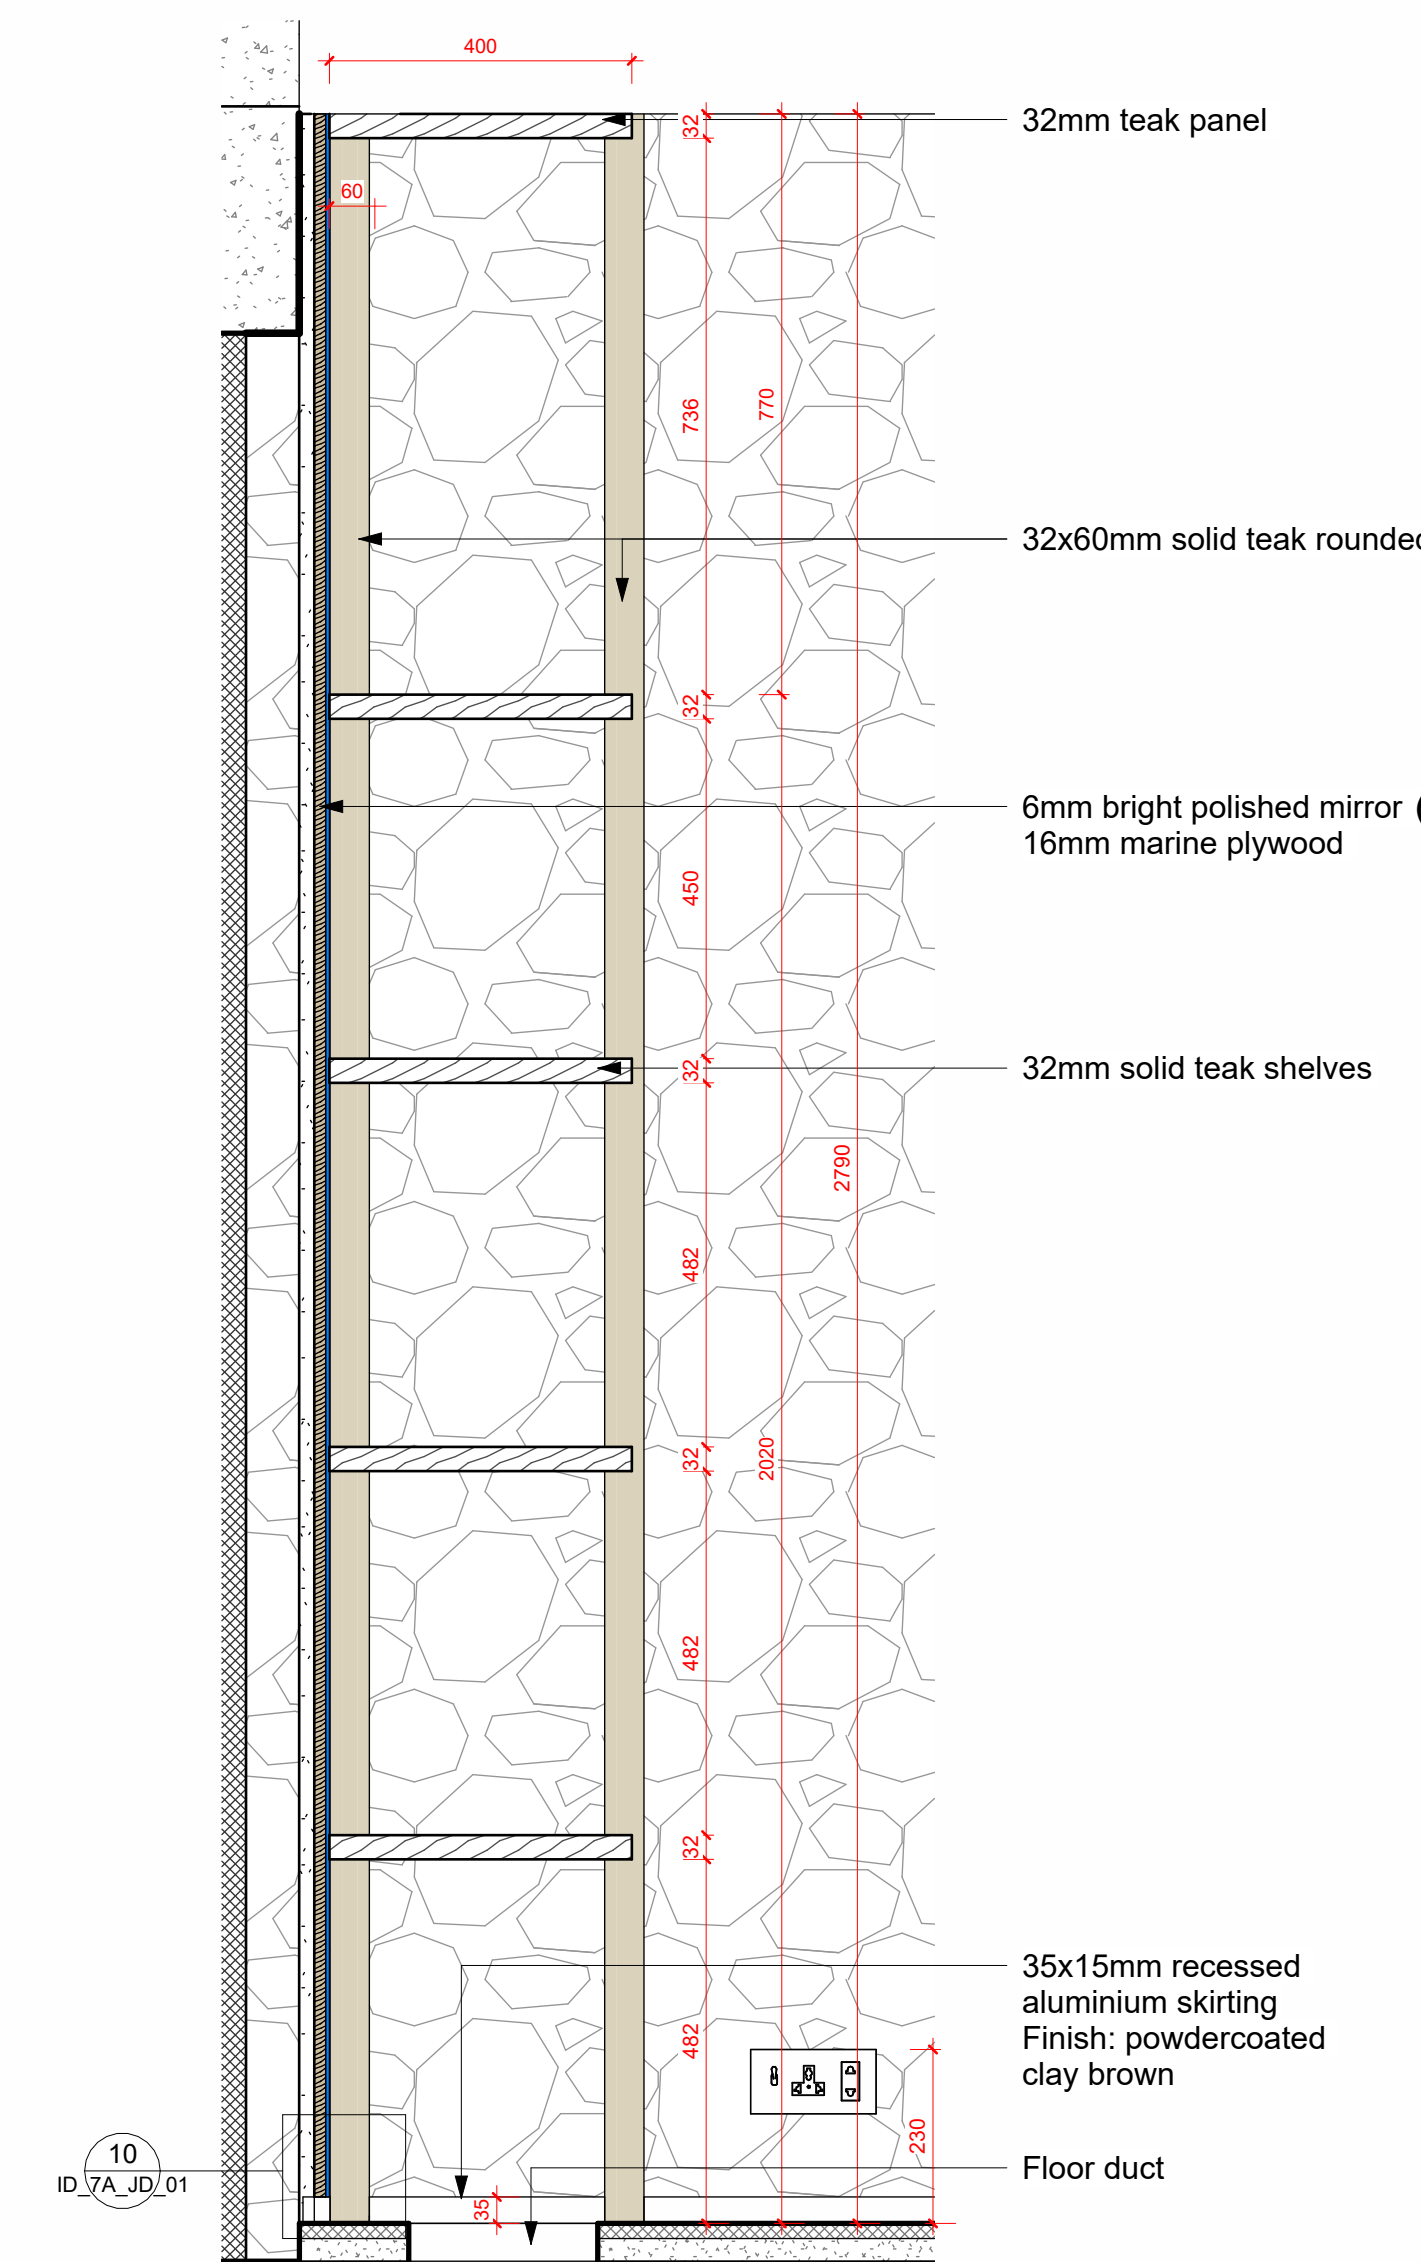


Section - Locker Shelves | 1:10

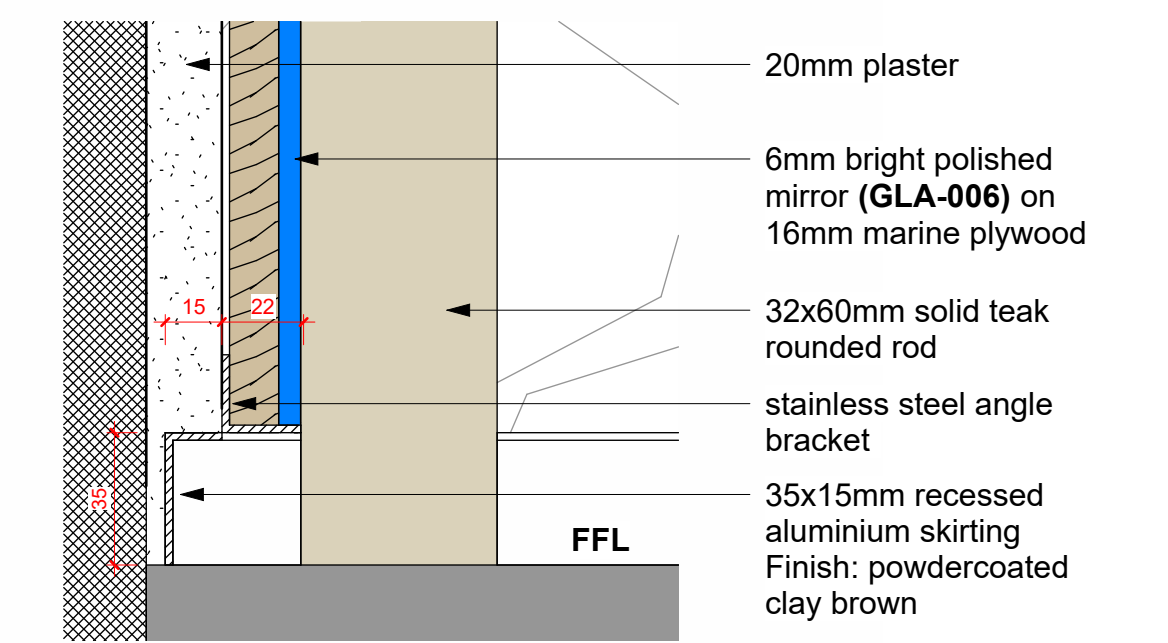


Callout - Skirting Detail | 1:2

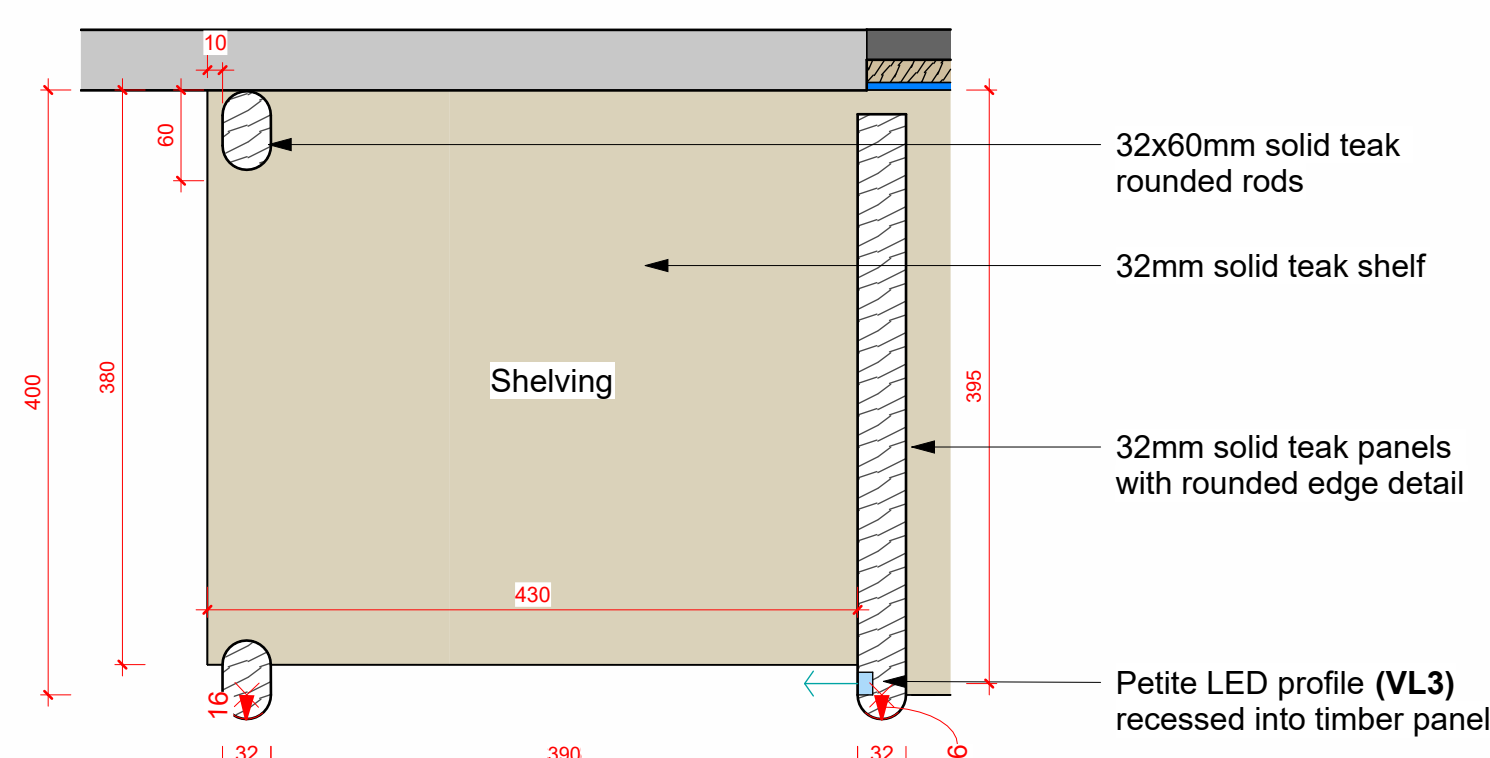


Floor Plan Callout - LED Strip Light | 1:5

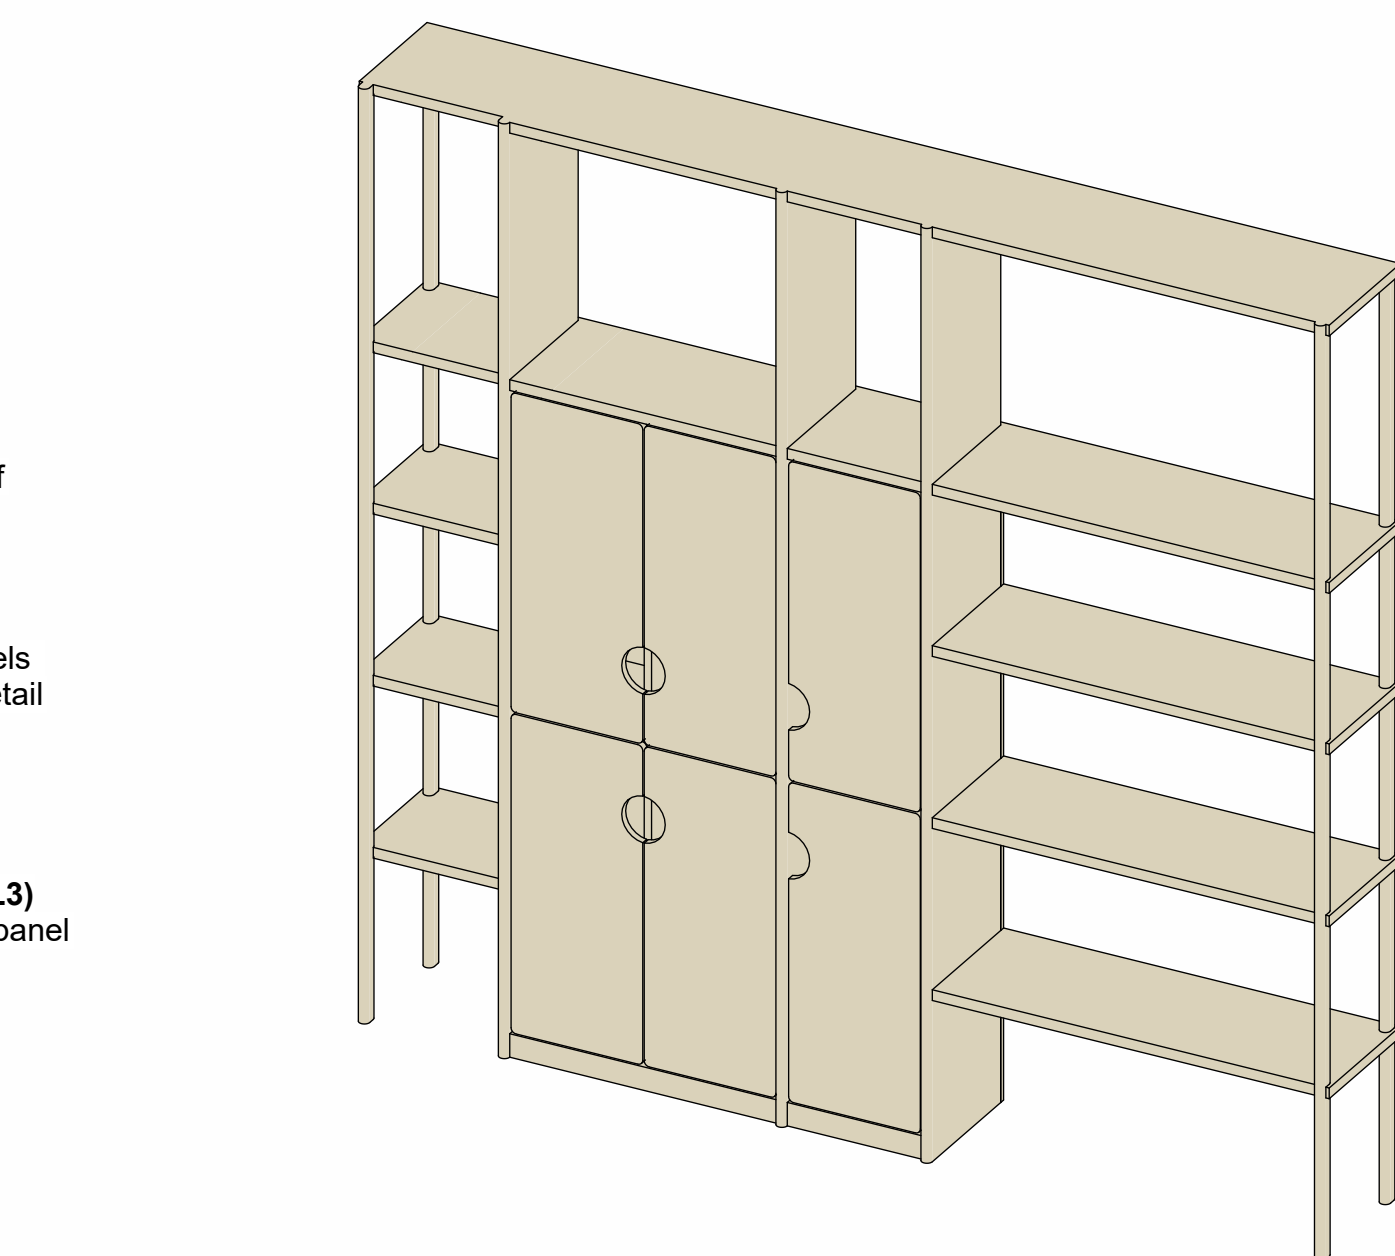



3D View - Lockers | 1:20

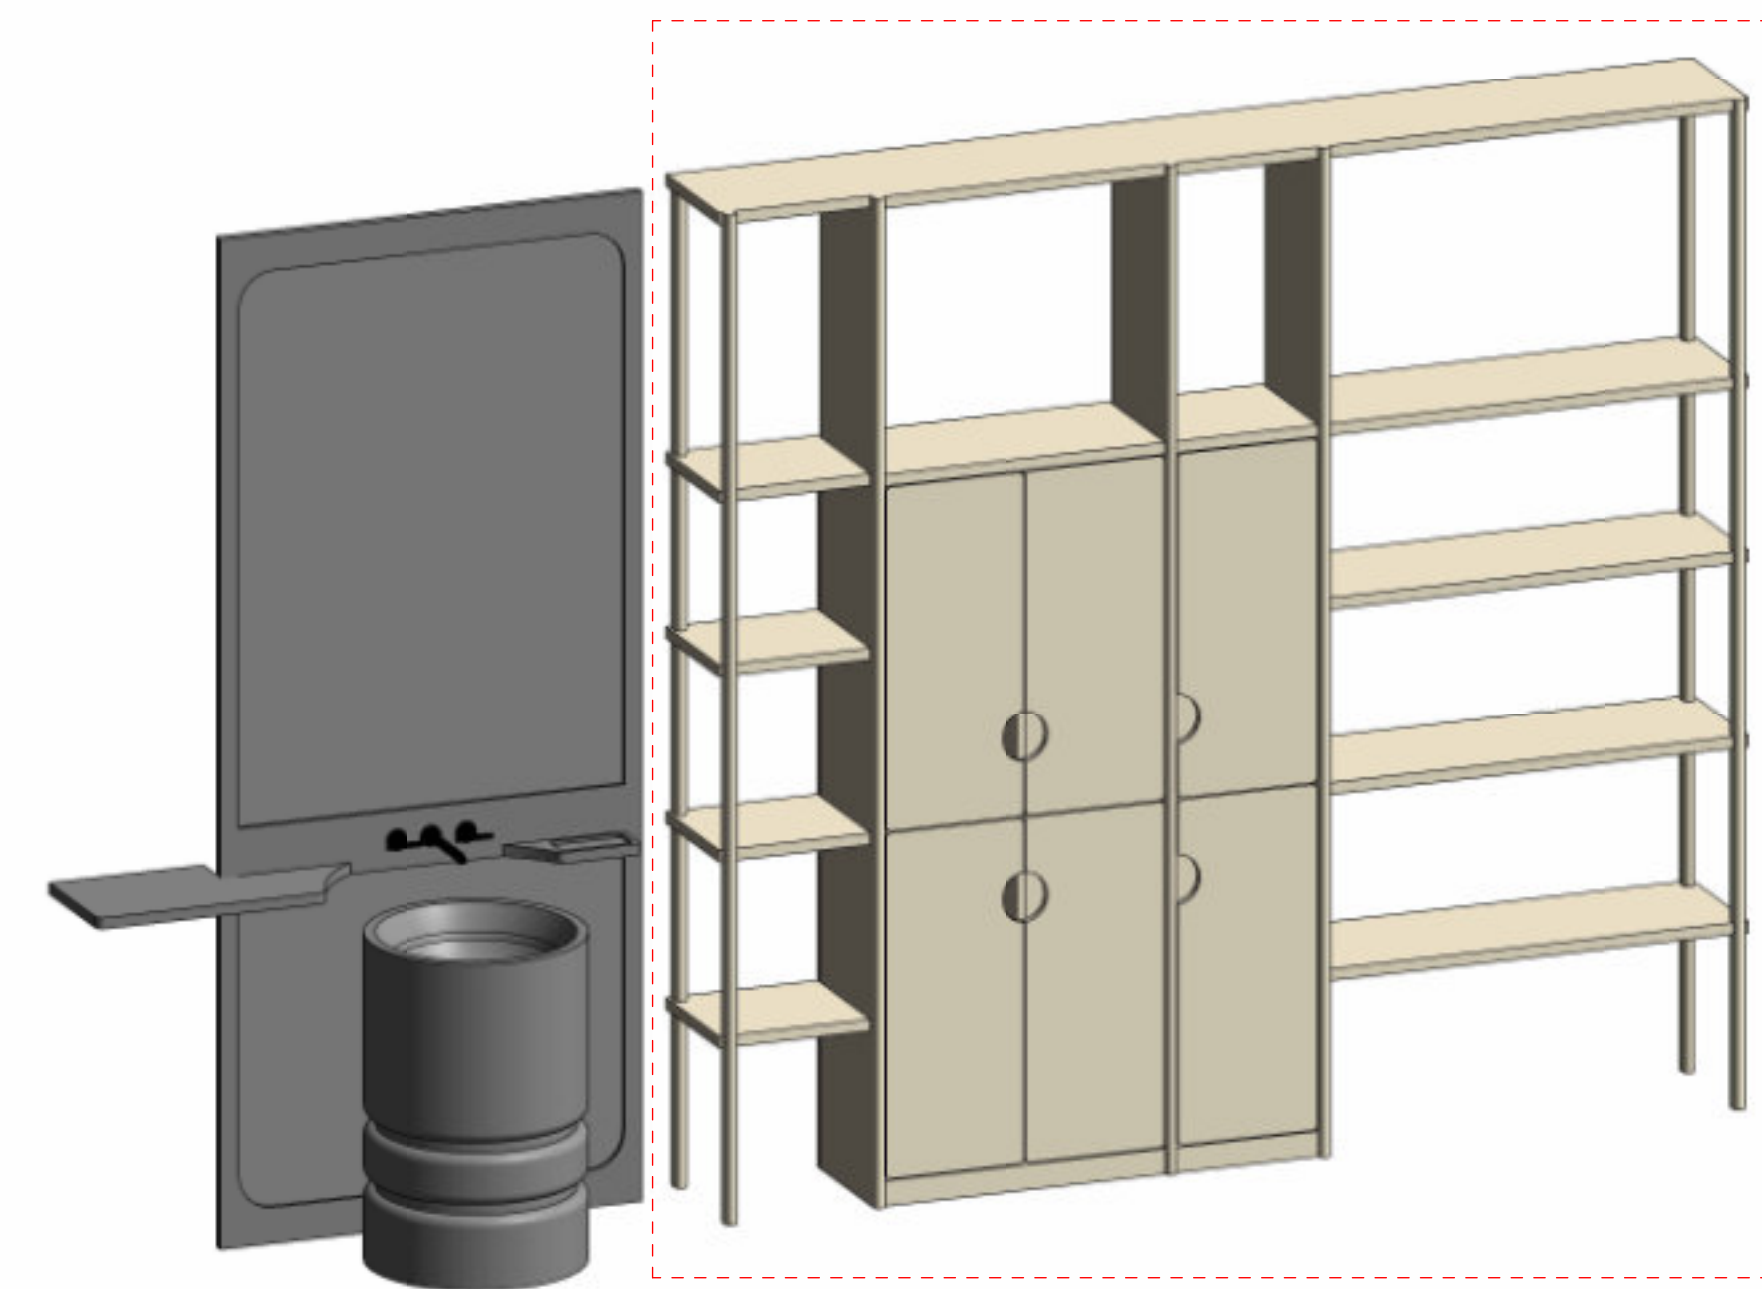



3D View - Vanity & Lockers | 1:20

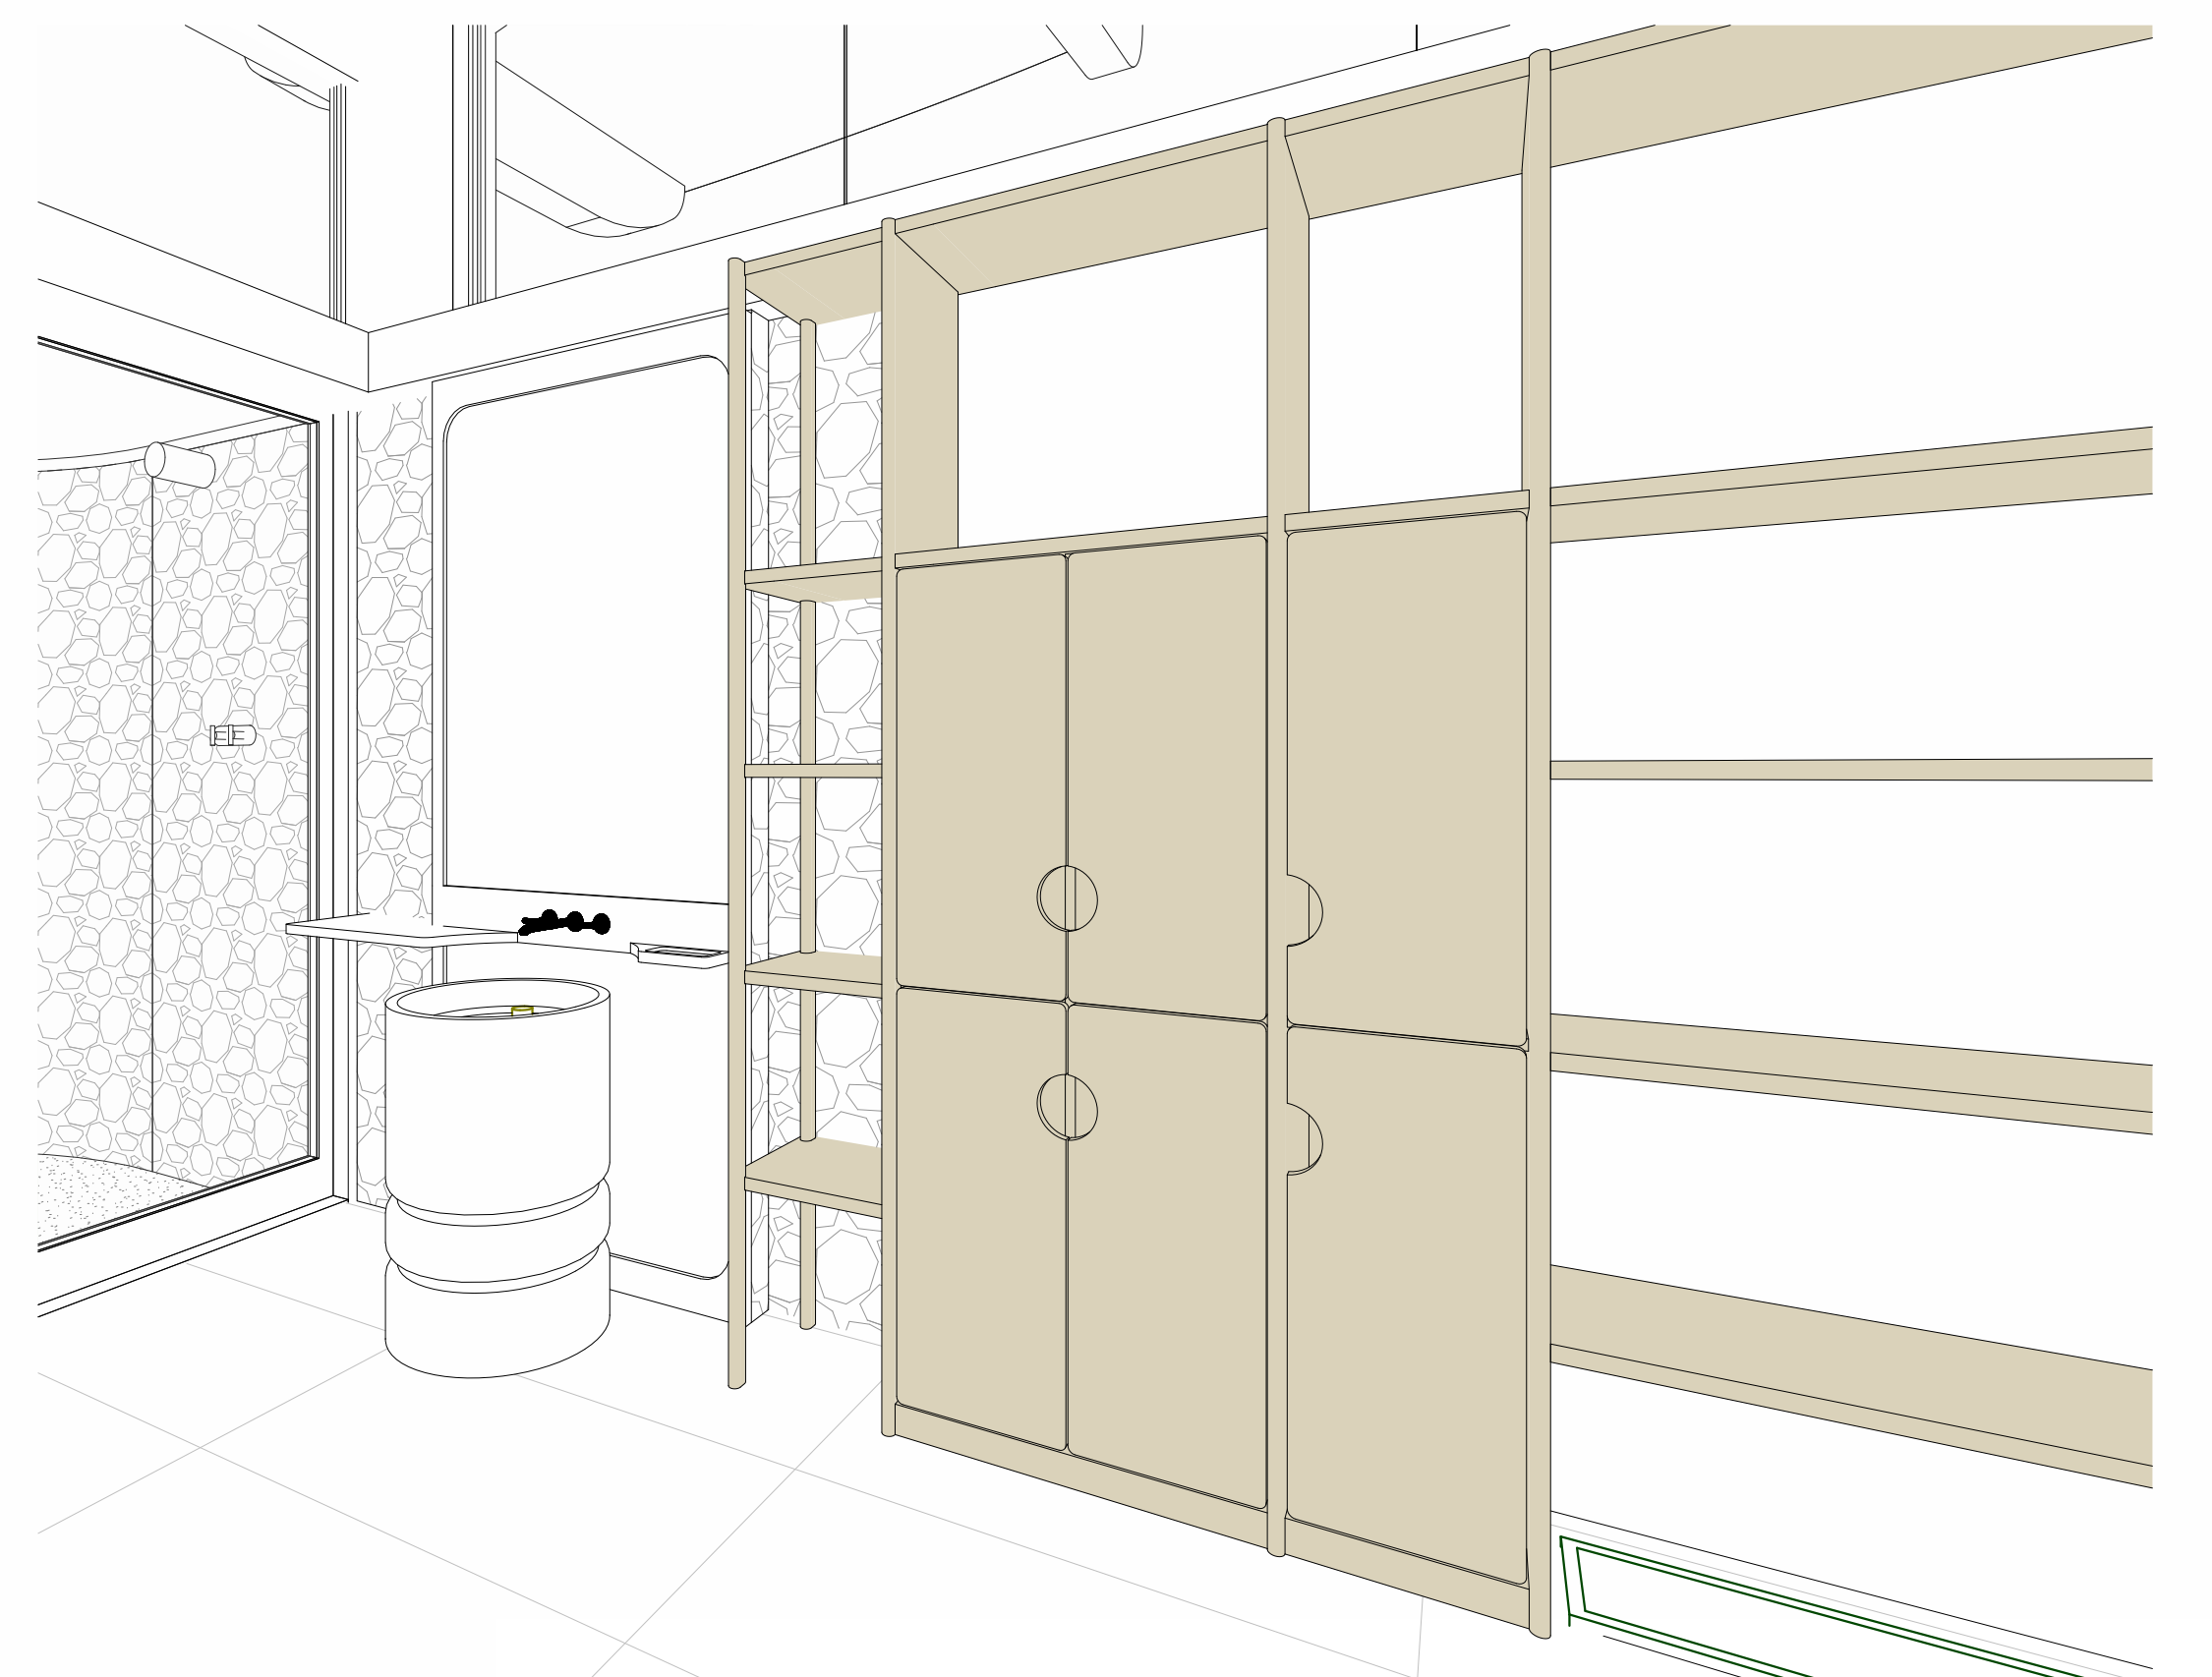

Perspective - Vanity & Lockers | N.T.S.

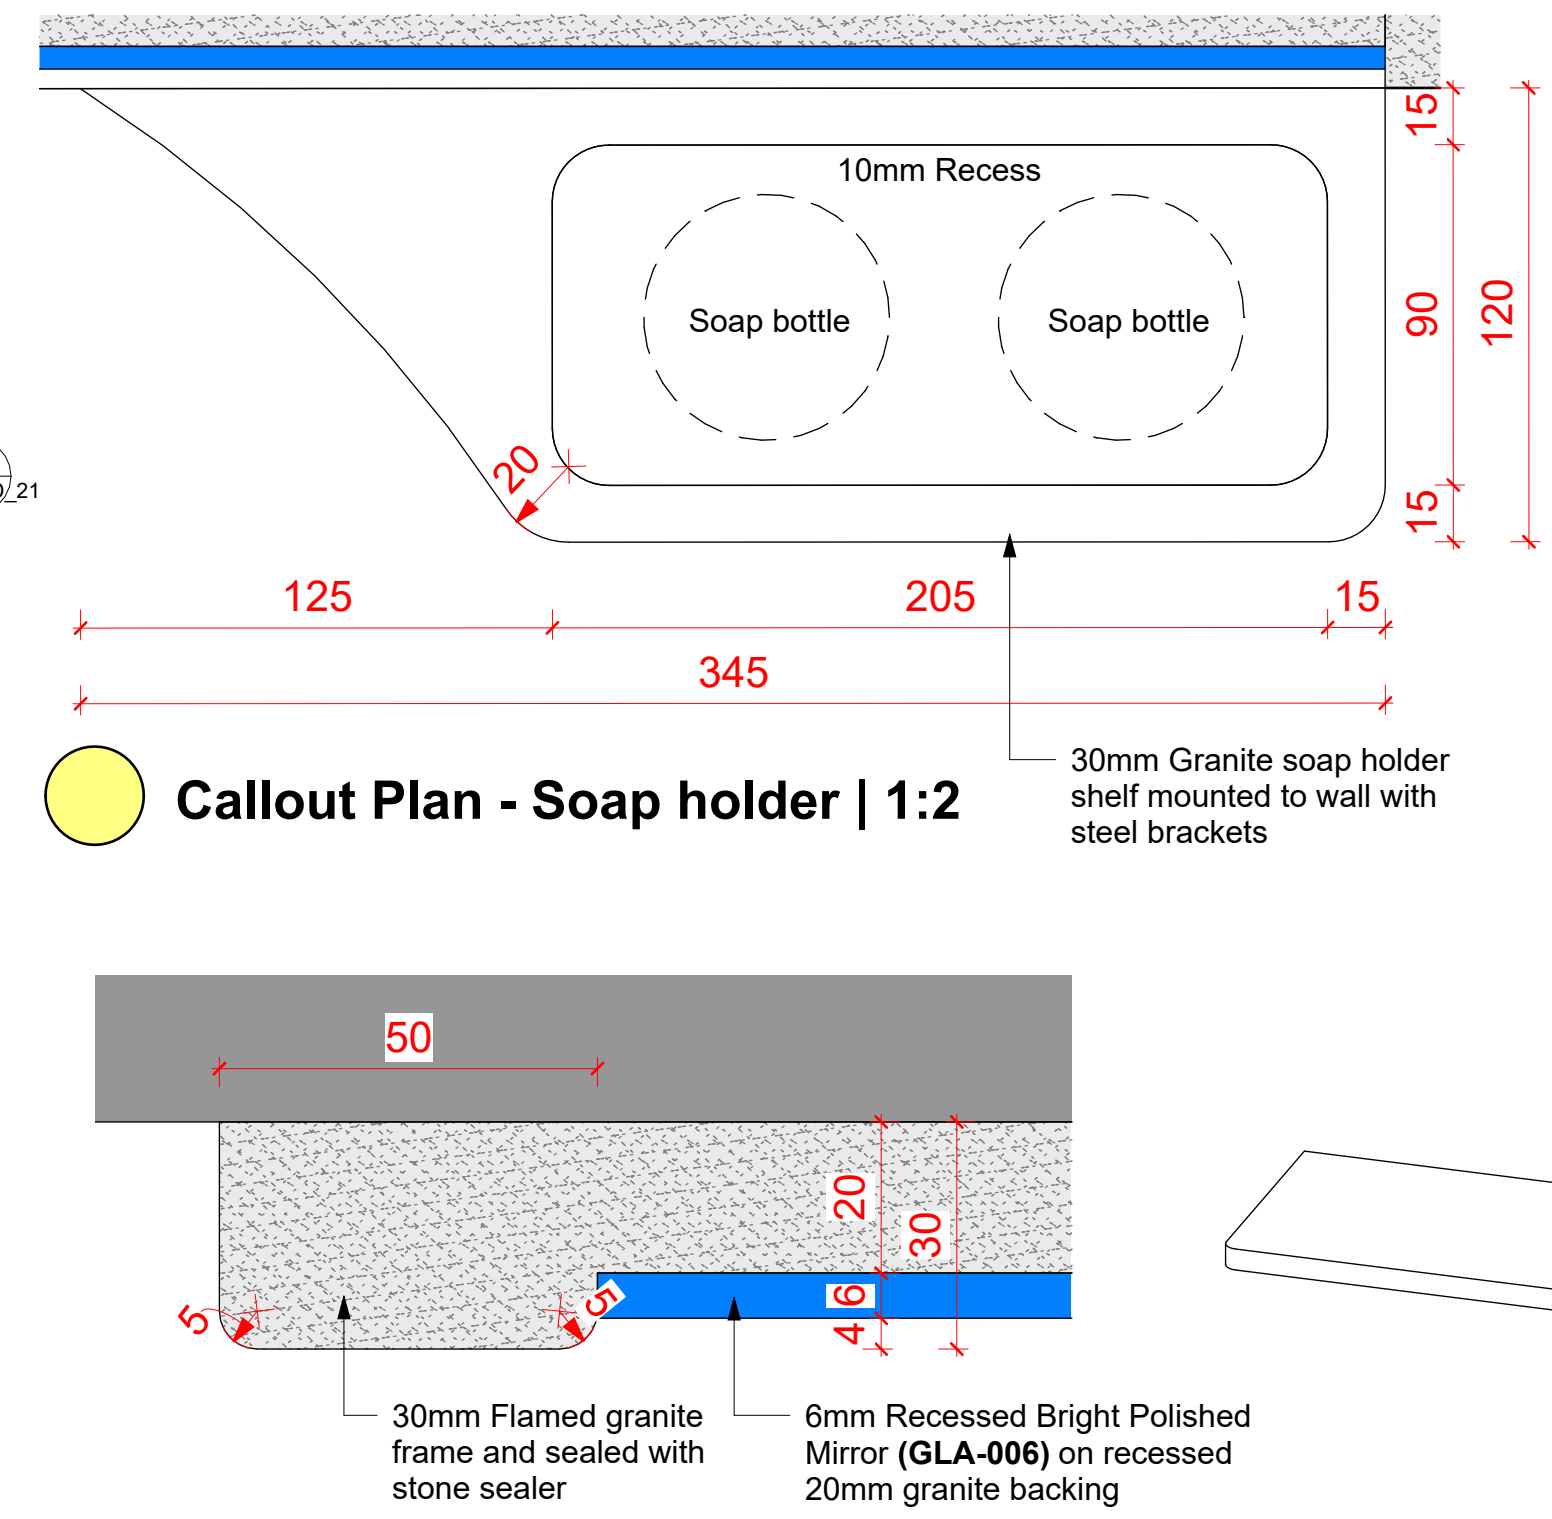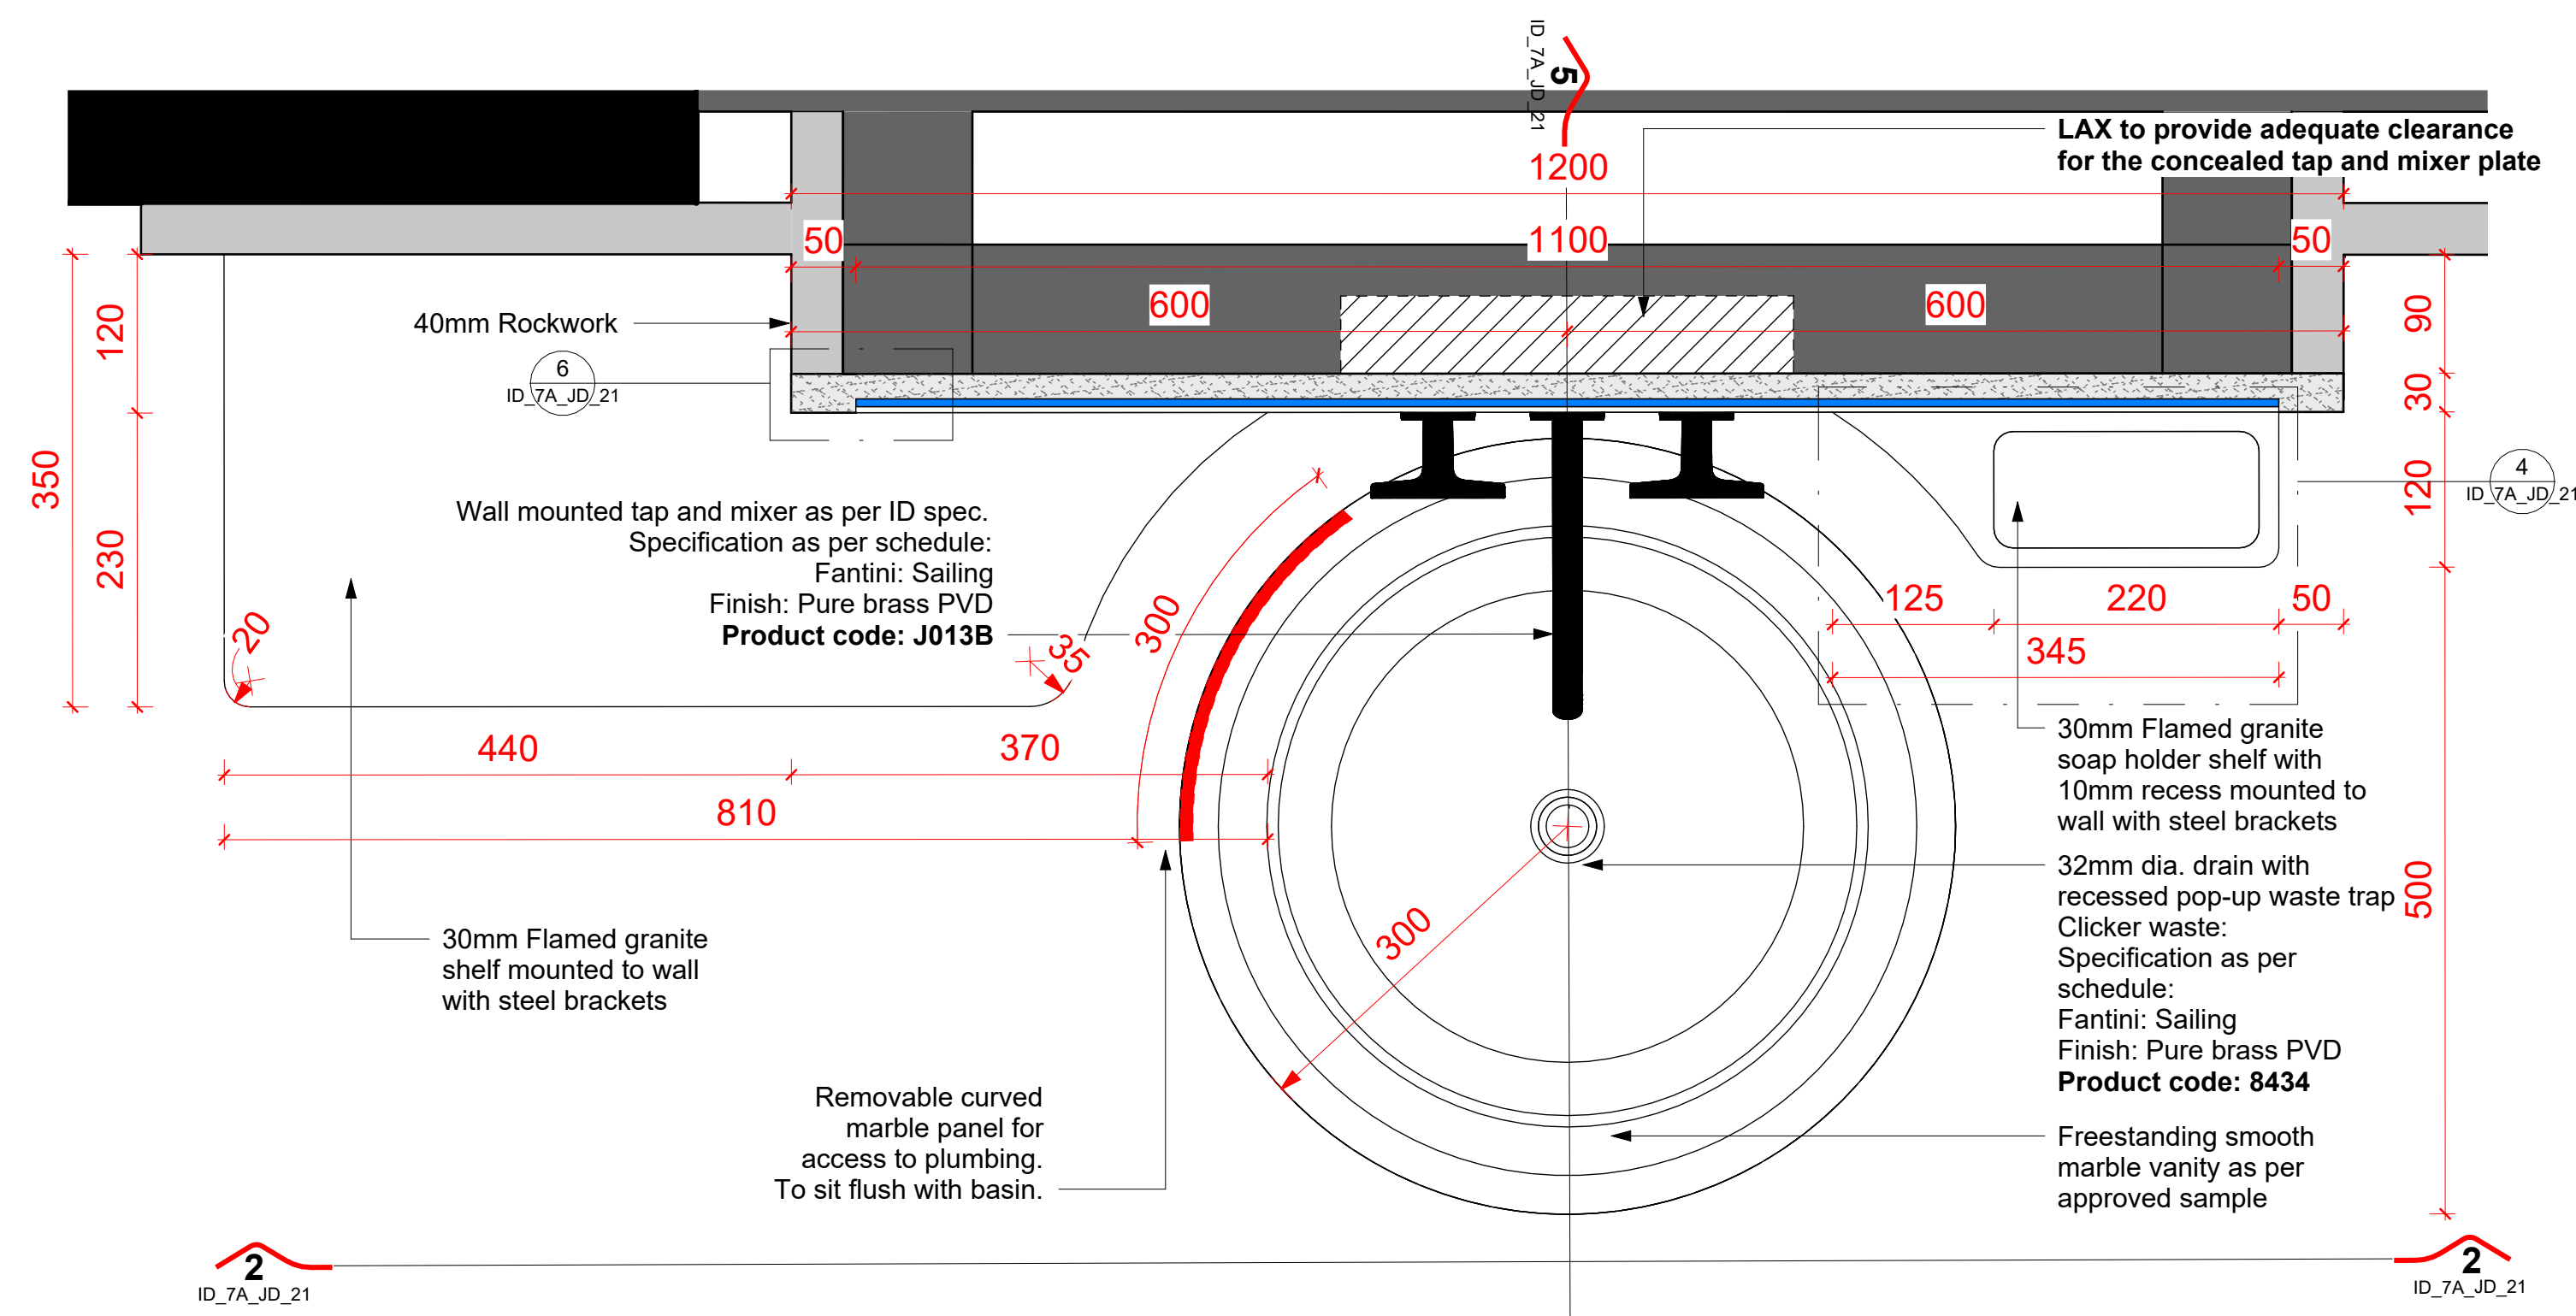


Callout Plan - Backing board | 1:1

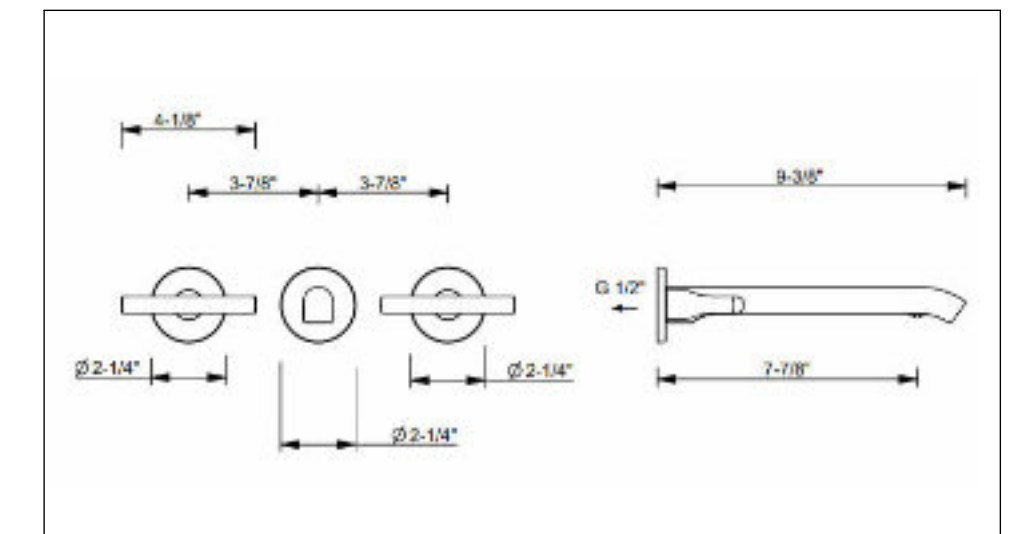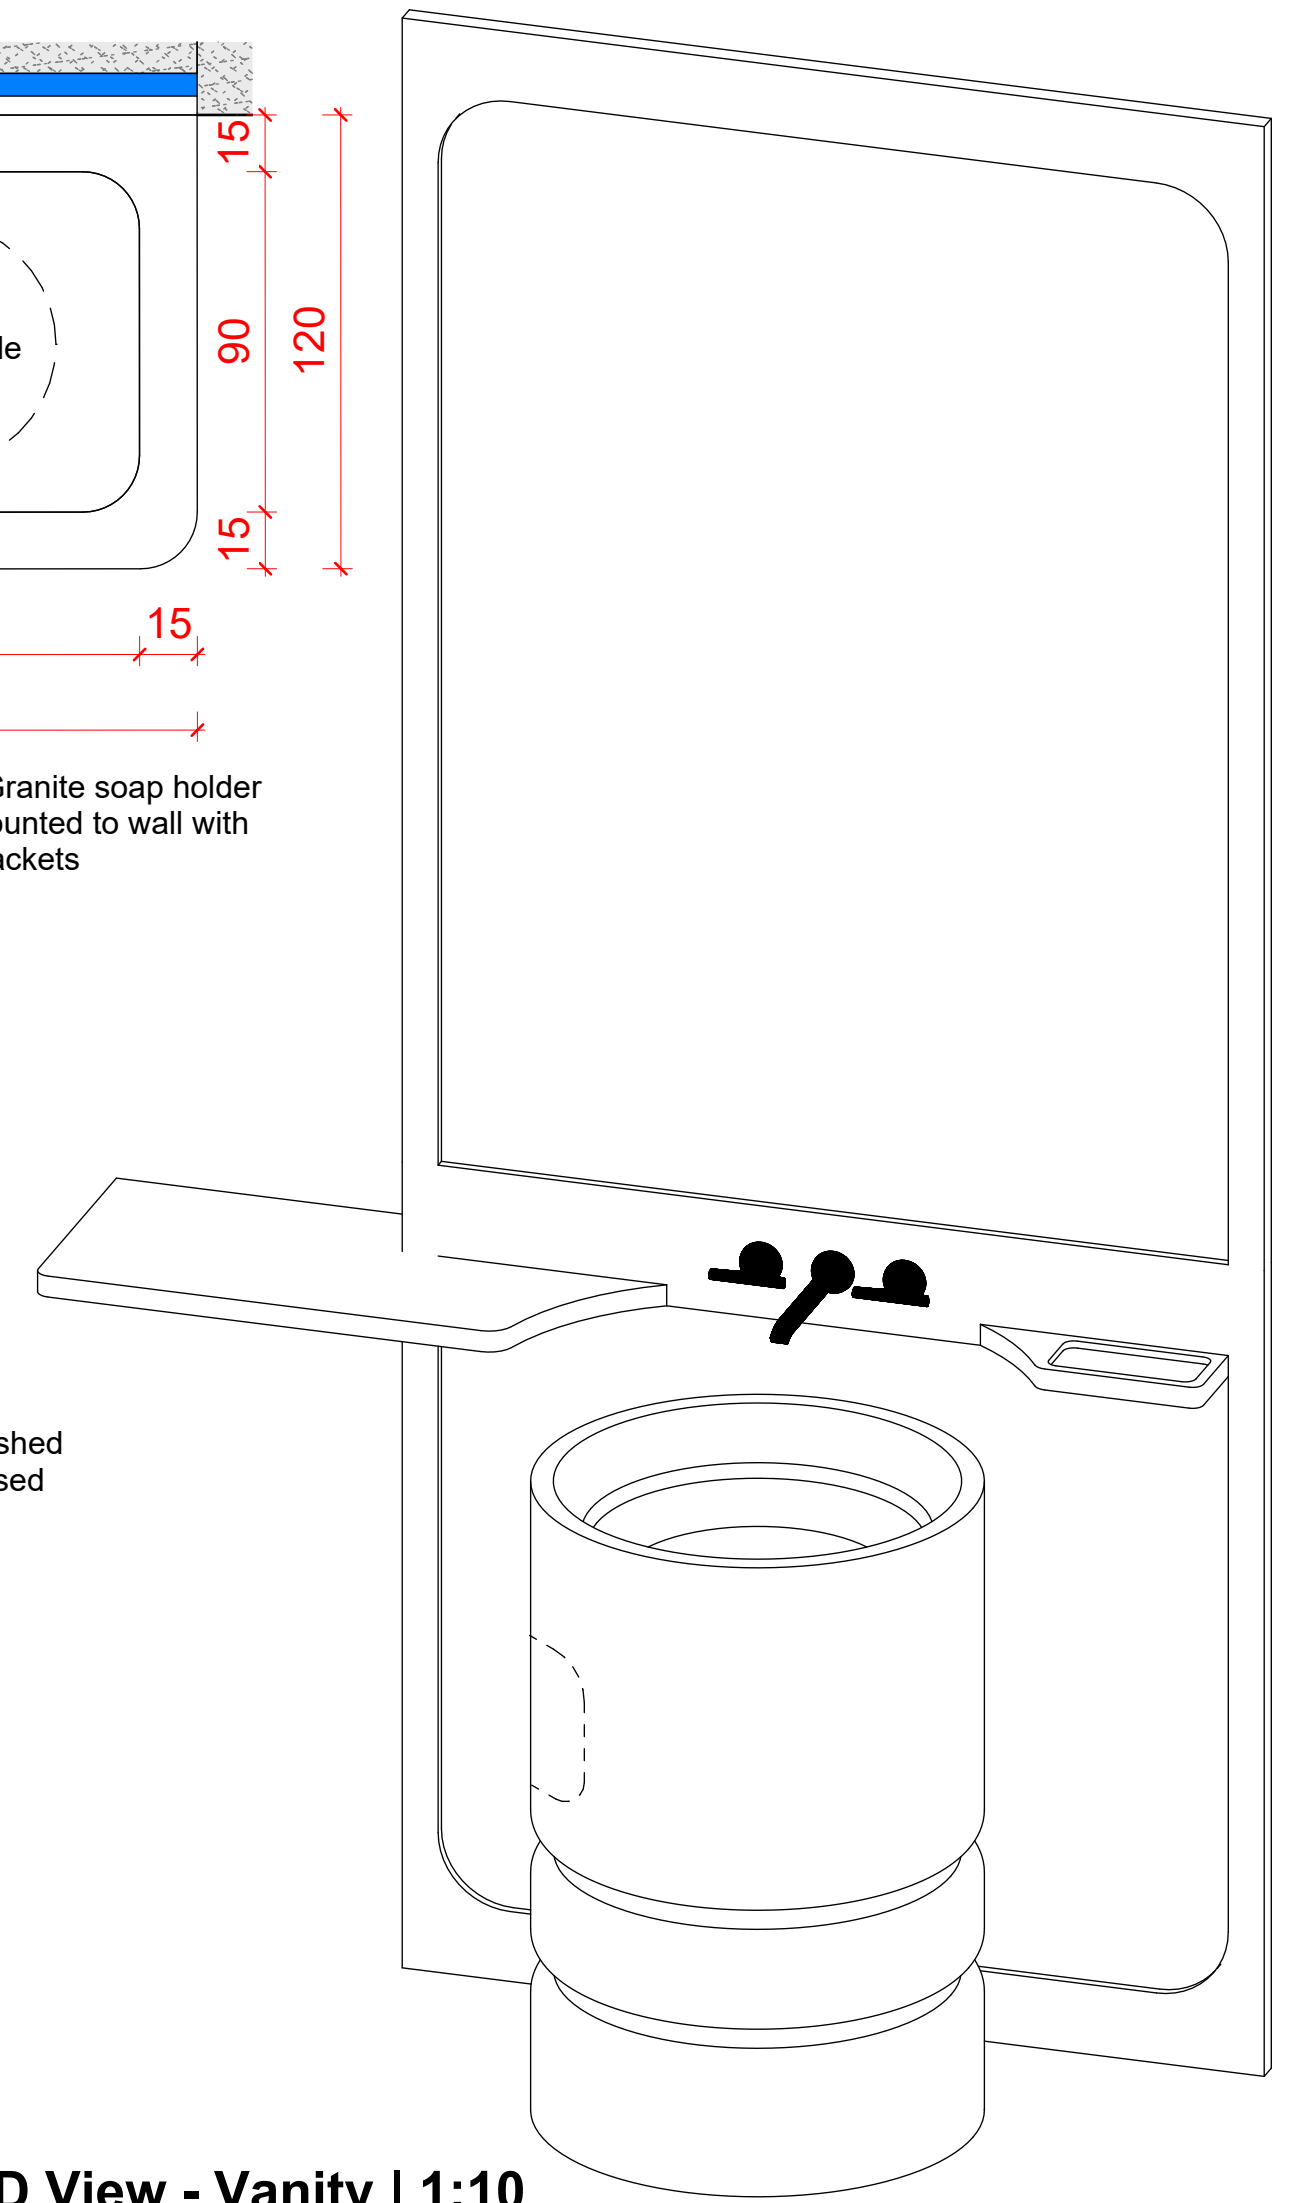


Tap & Mixer



Finish: Pure brass PVD

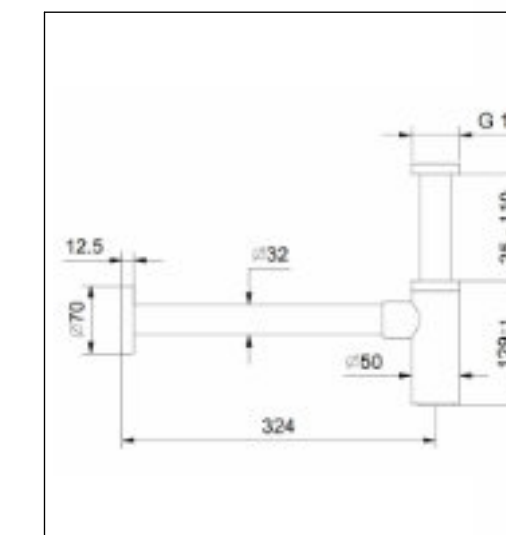

Bottle Trap

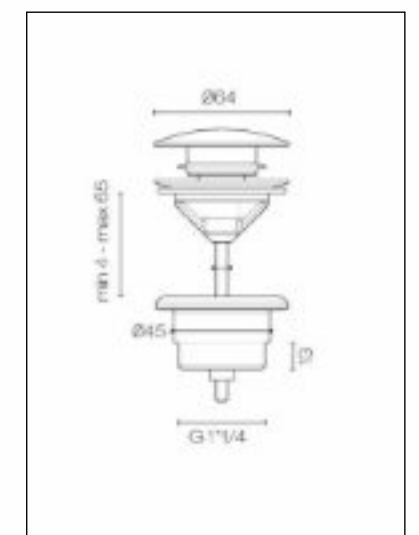

Clicker Waste

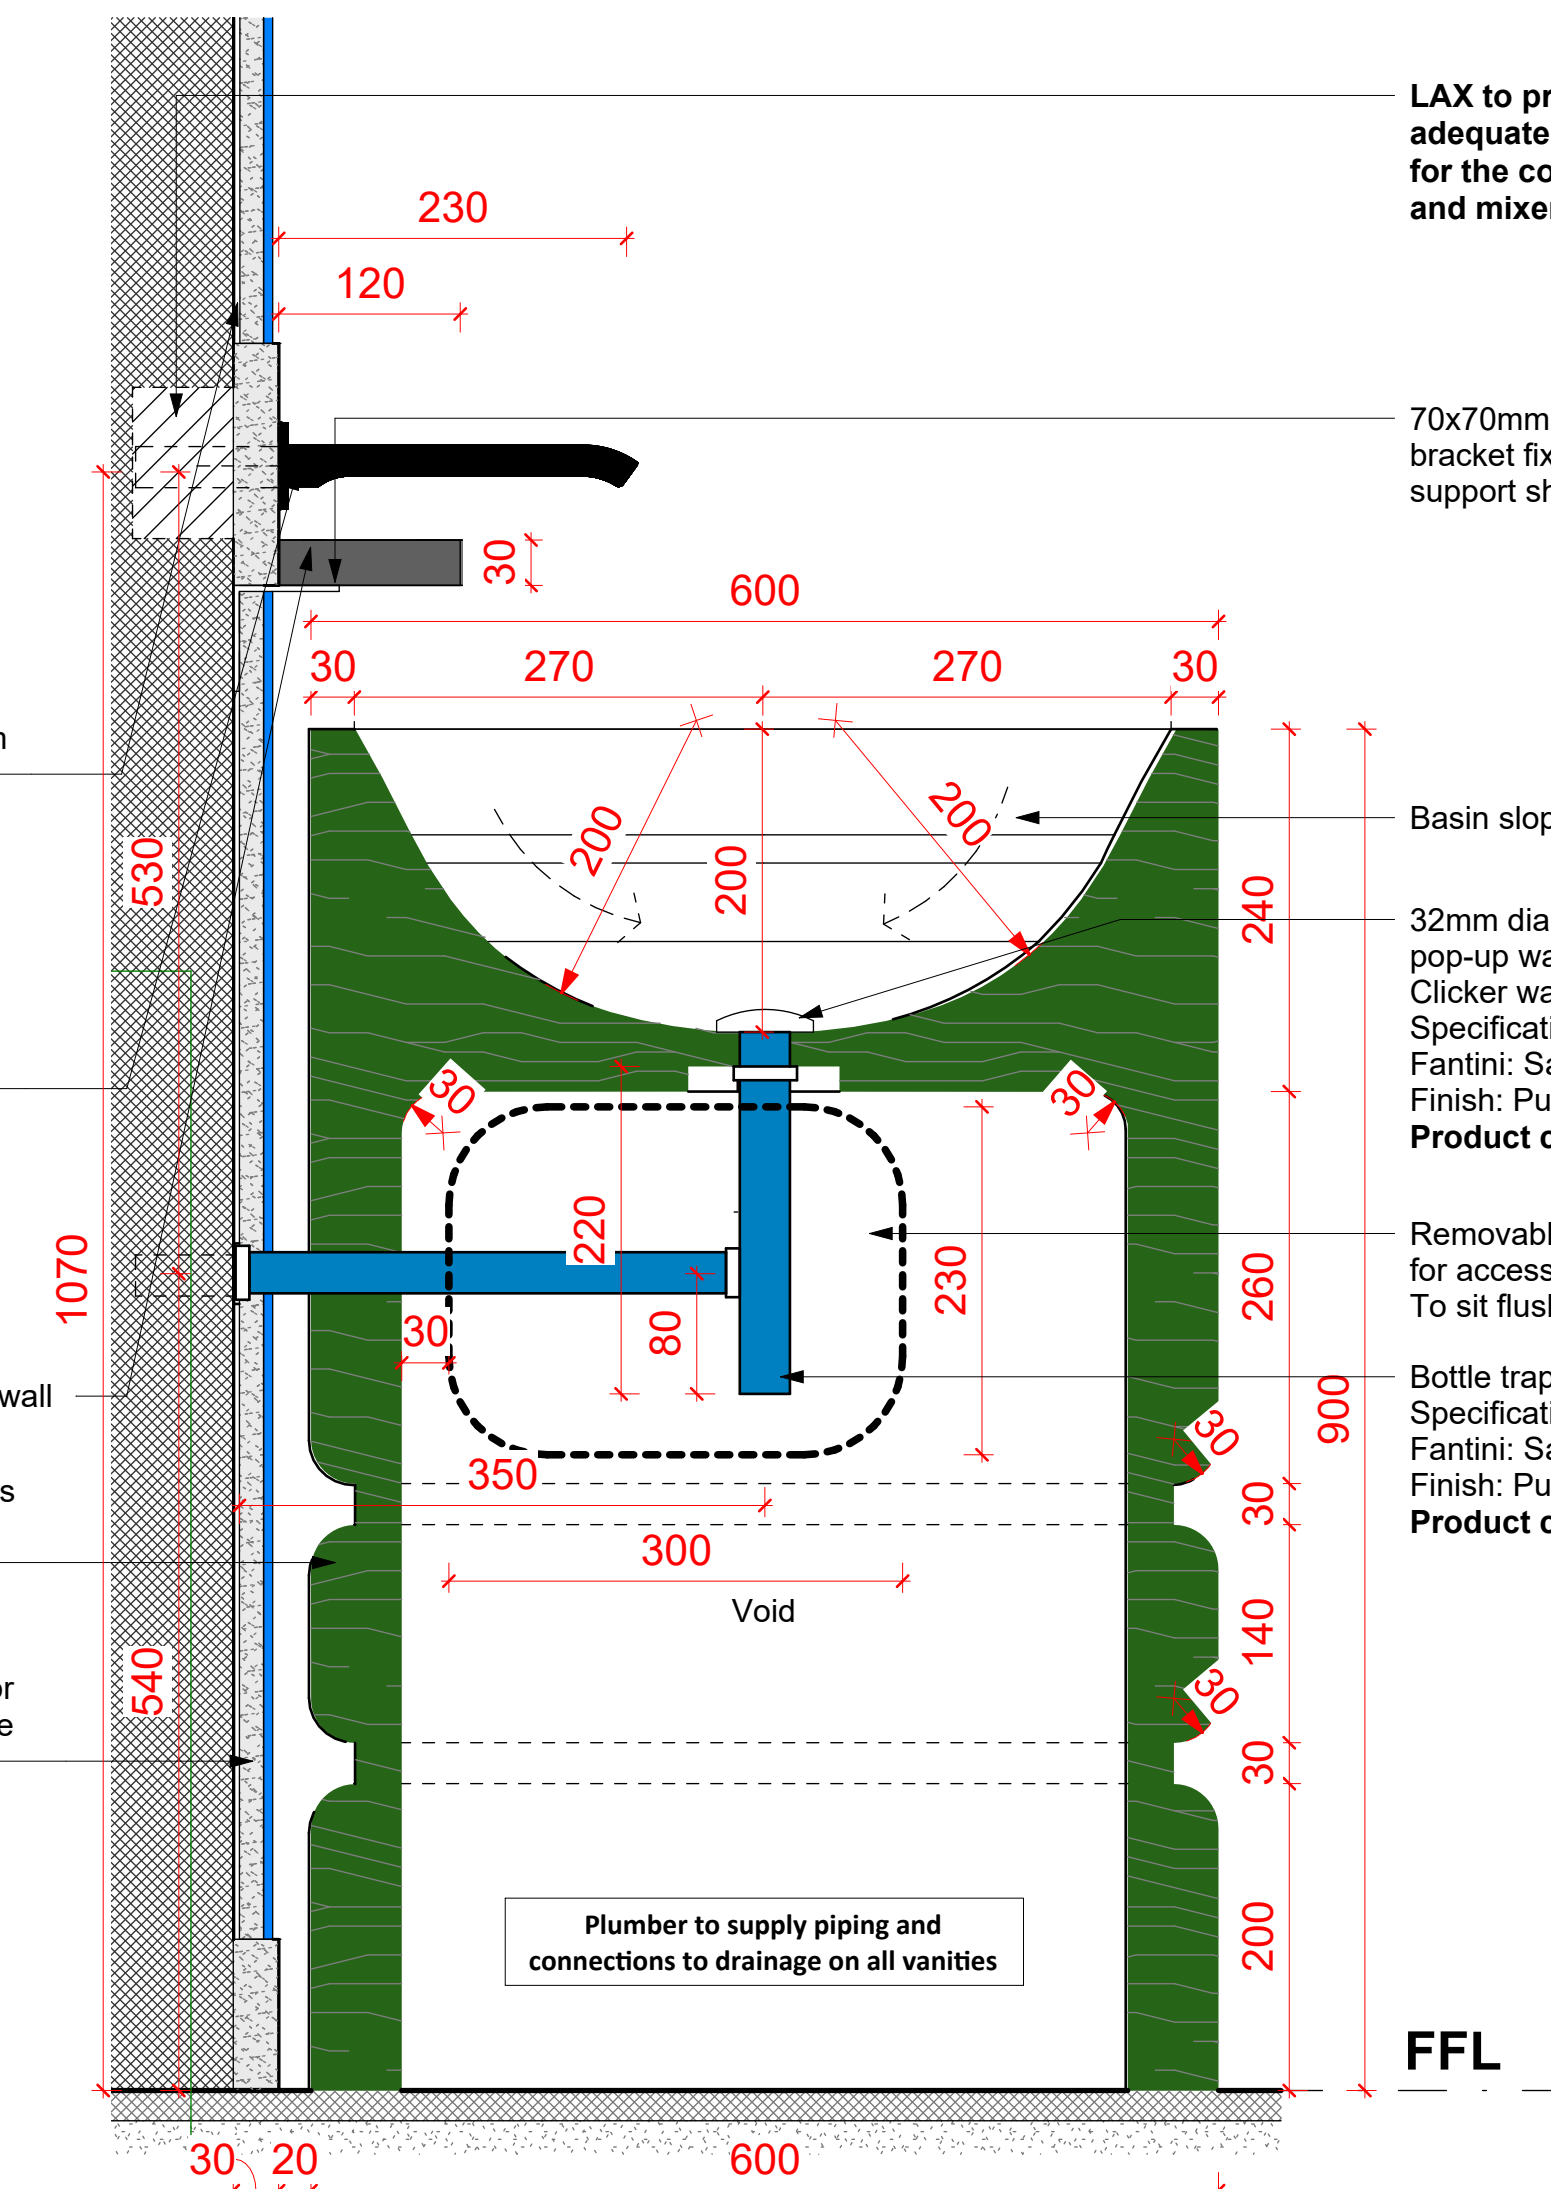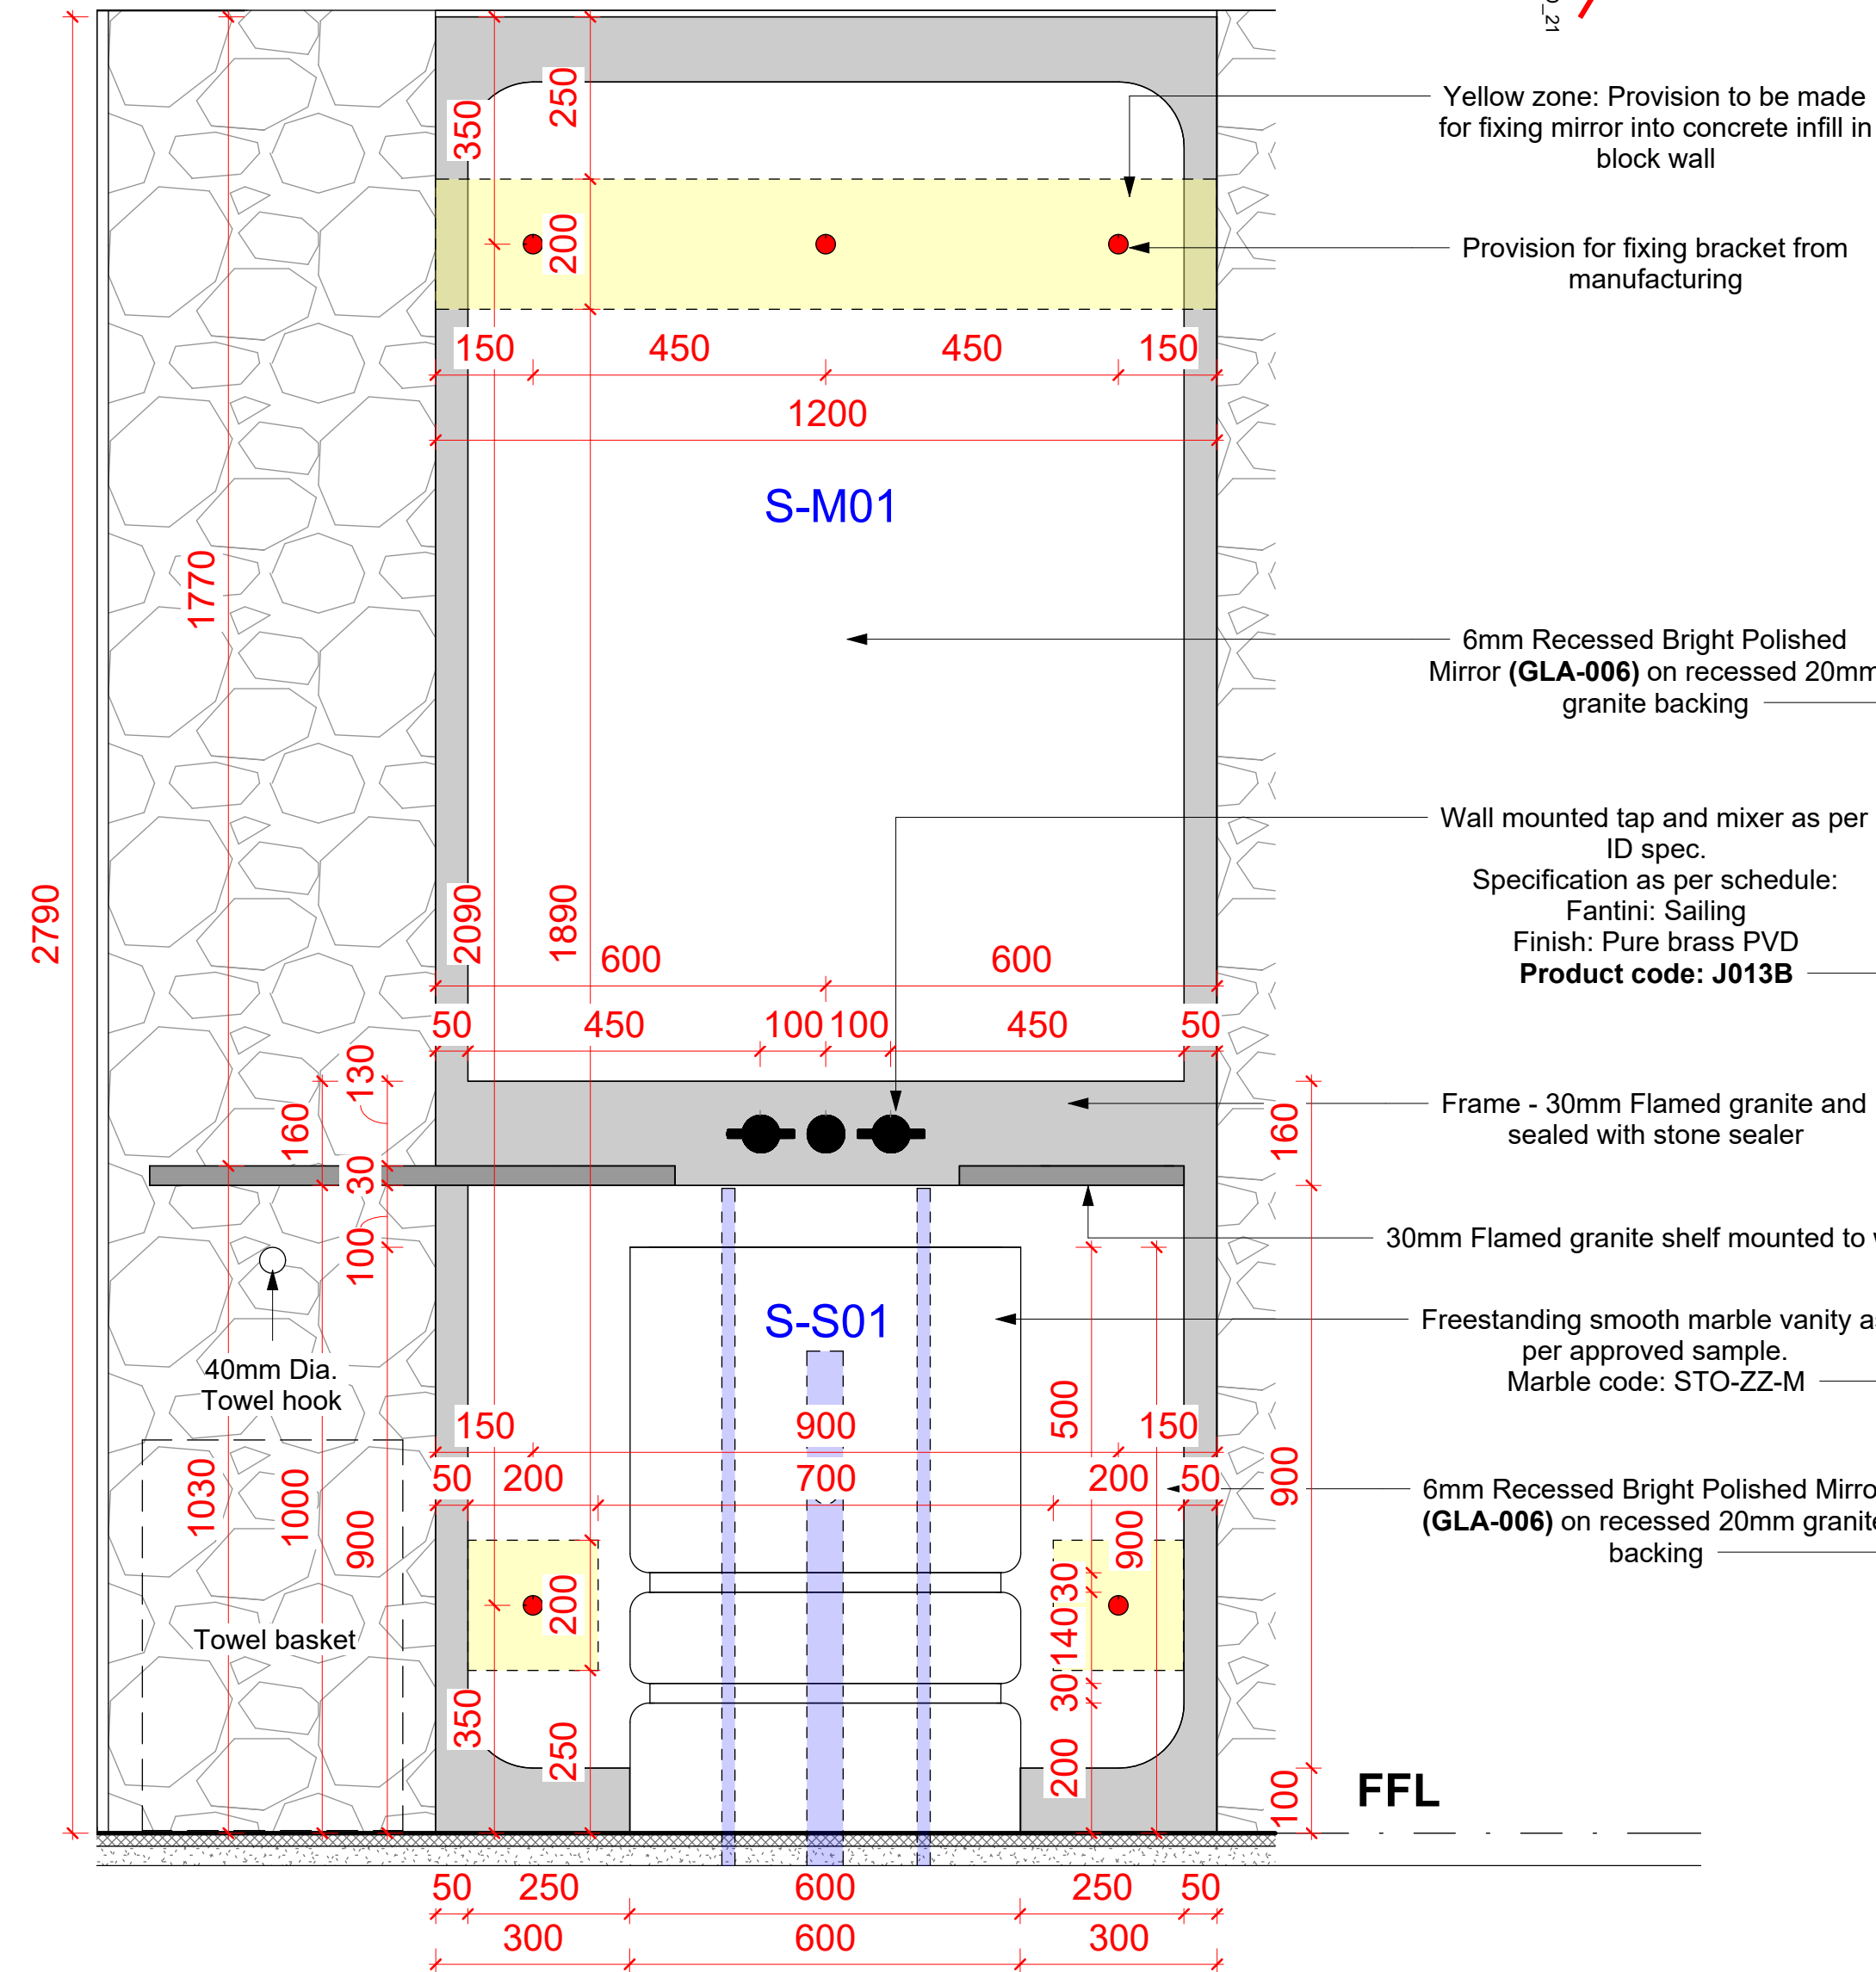

Section - Vanity | 1:5

gym freestanding basin