




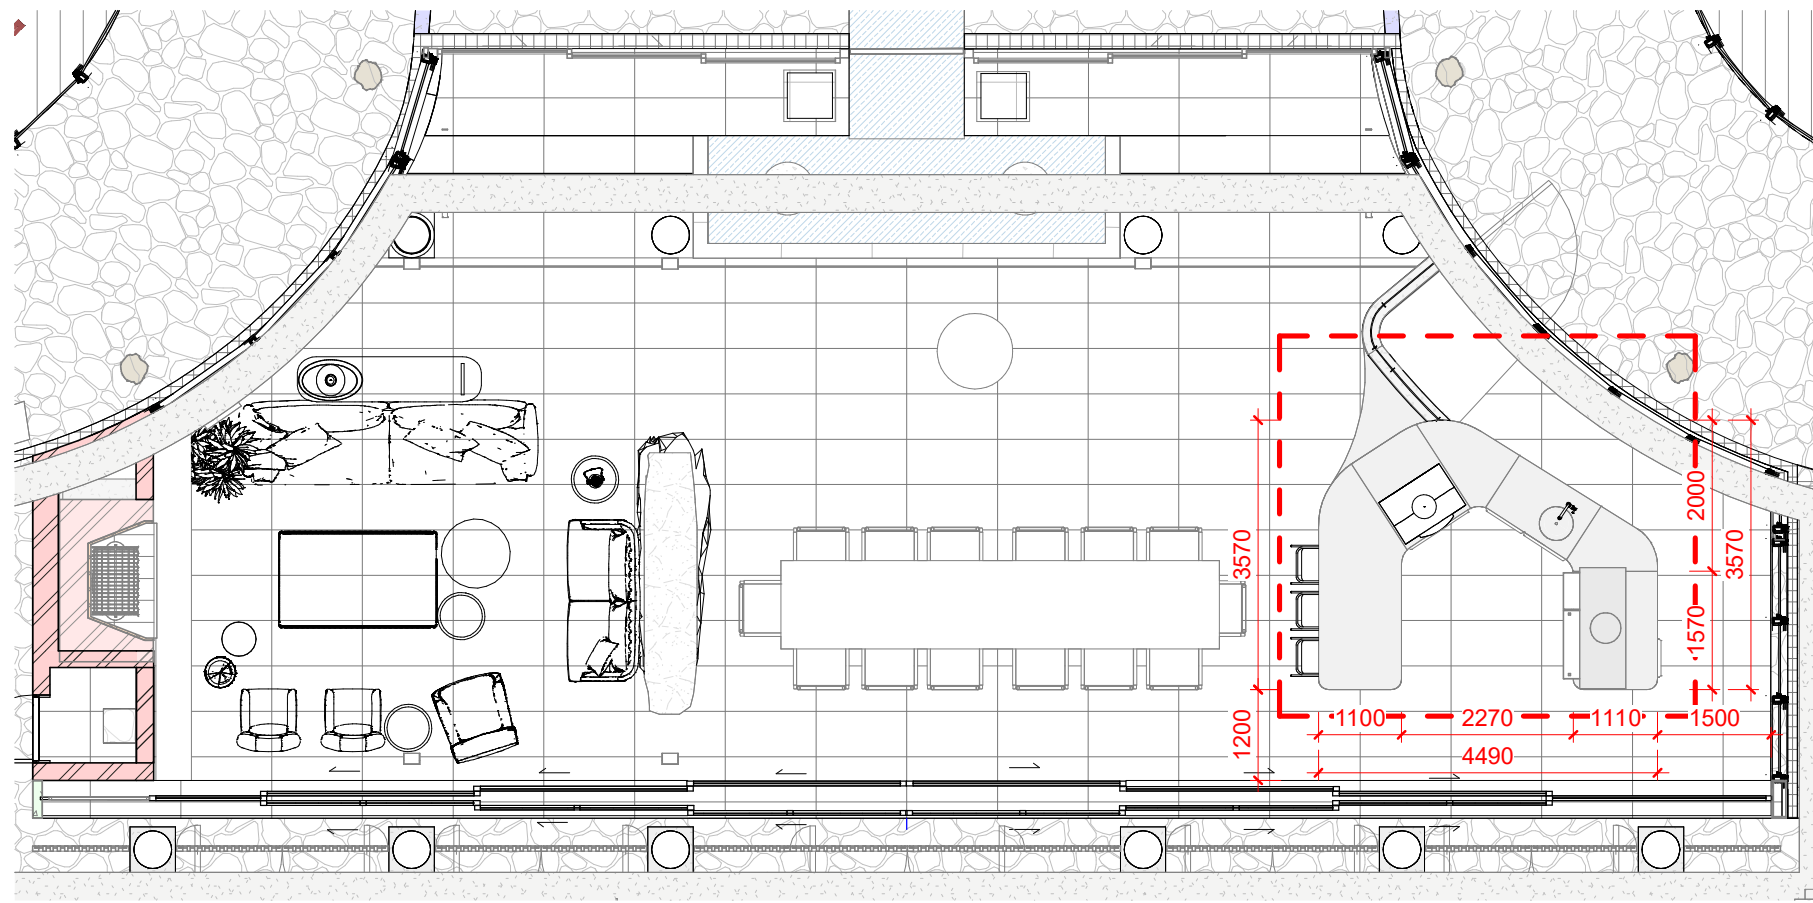


① Reference Plan - Pavilion - Cooking Station
1:100

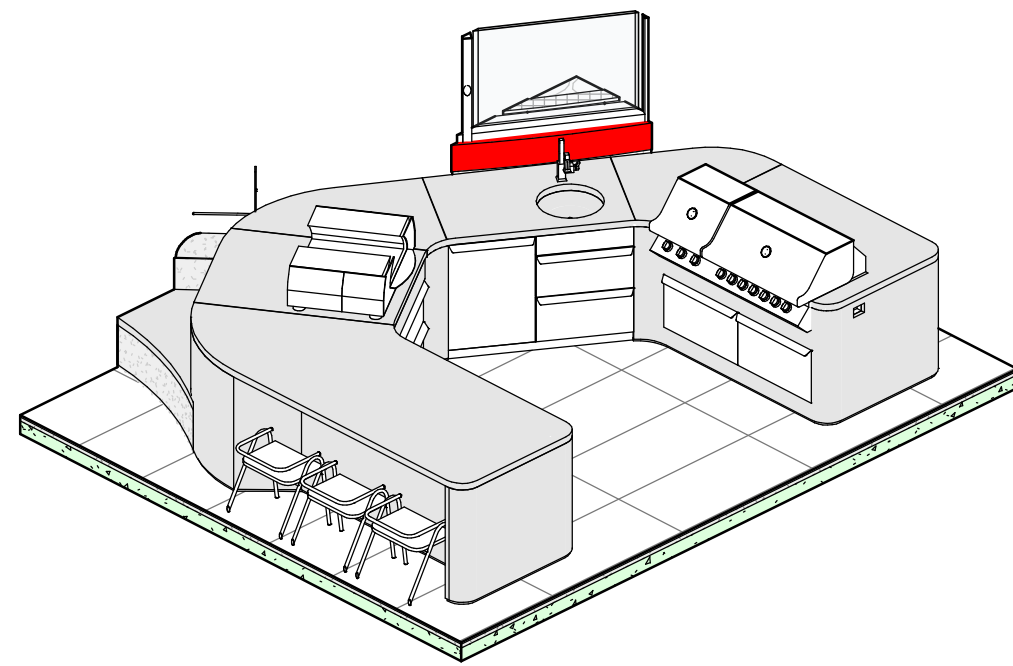

② 3D - Pavilion Cooking Station

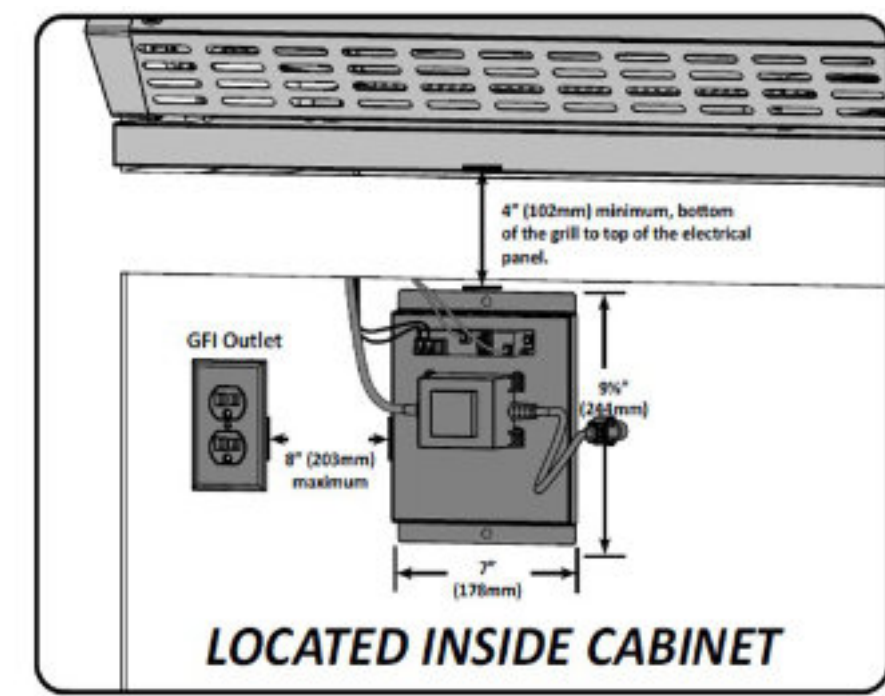


Reference Image
Socket and control panel for gas braai.

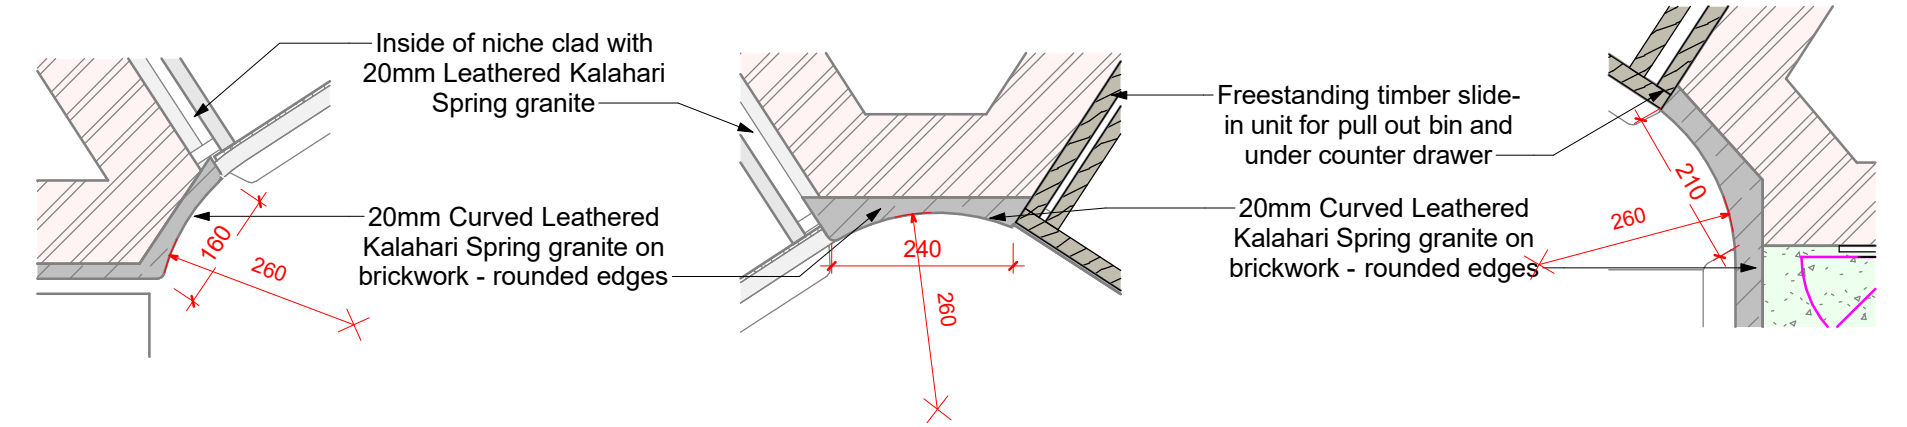

⑤ Plan Callout 01 - Granite Curve
1:10

⑥ Plan Callout 02 - Granite Curve
1:10

⑦ Plan Callout 03 - Granite Curve
1:10

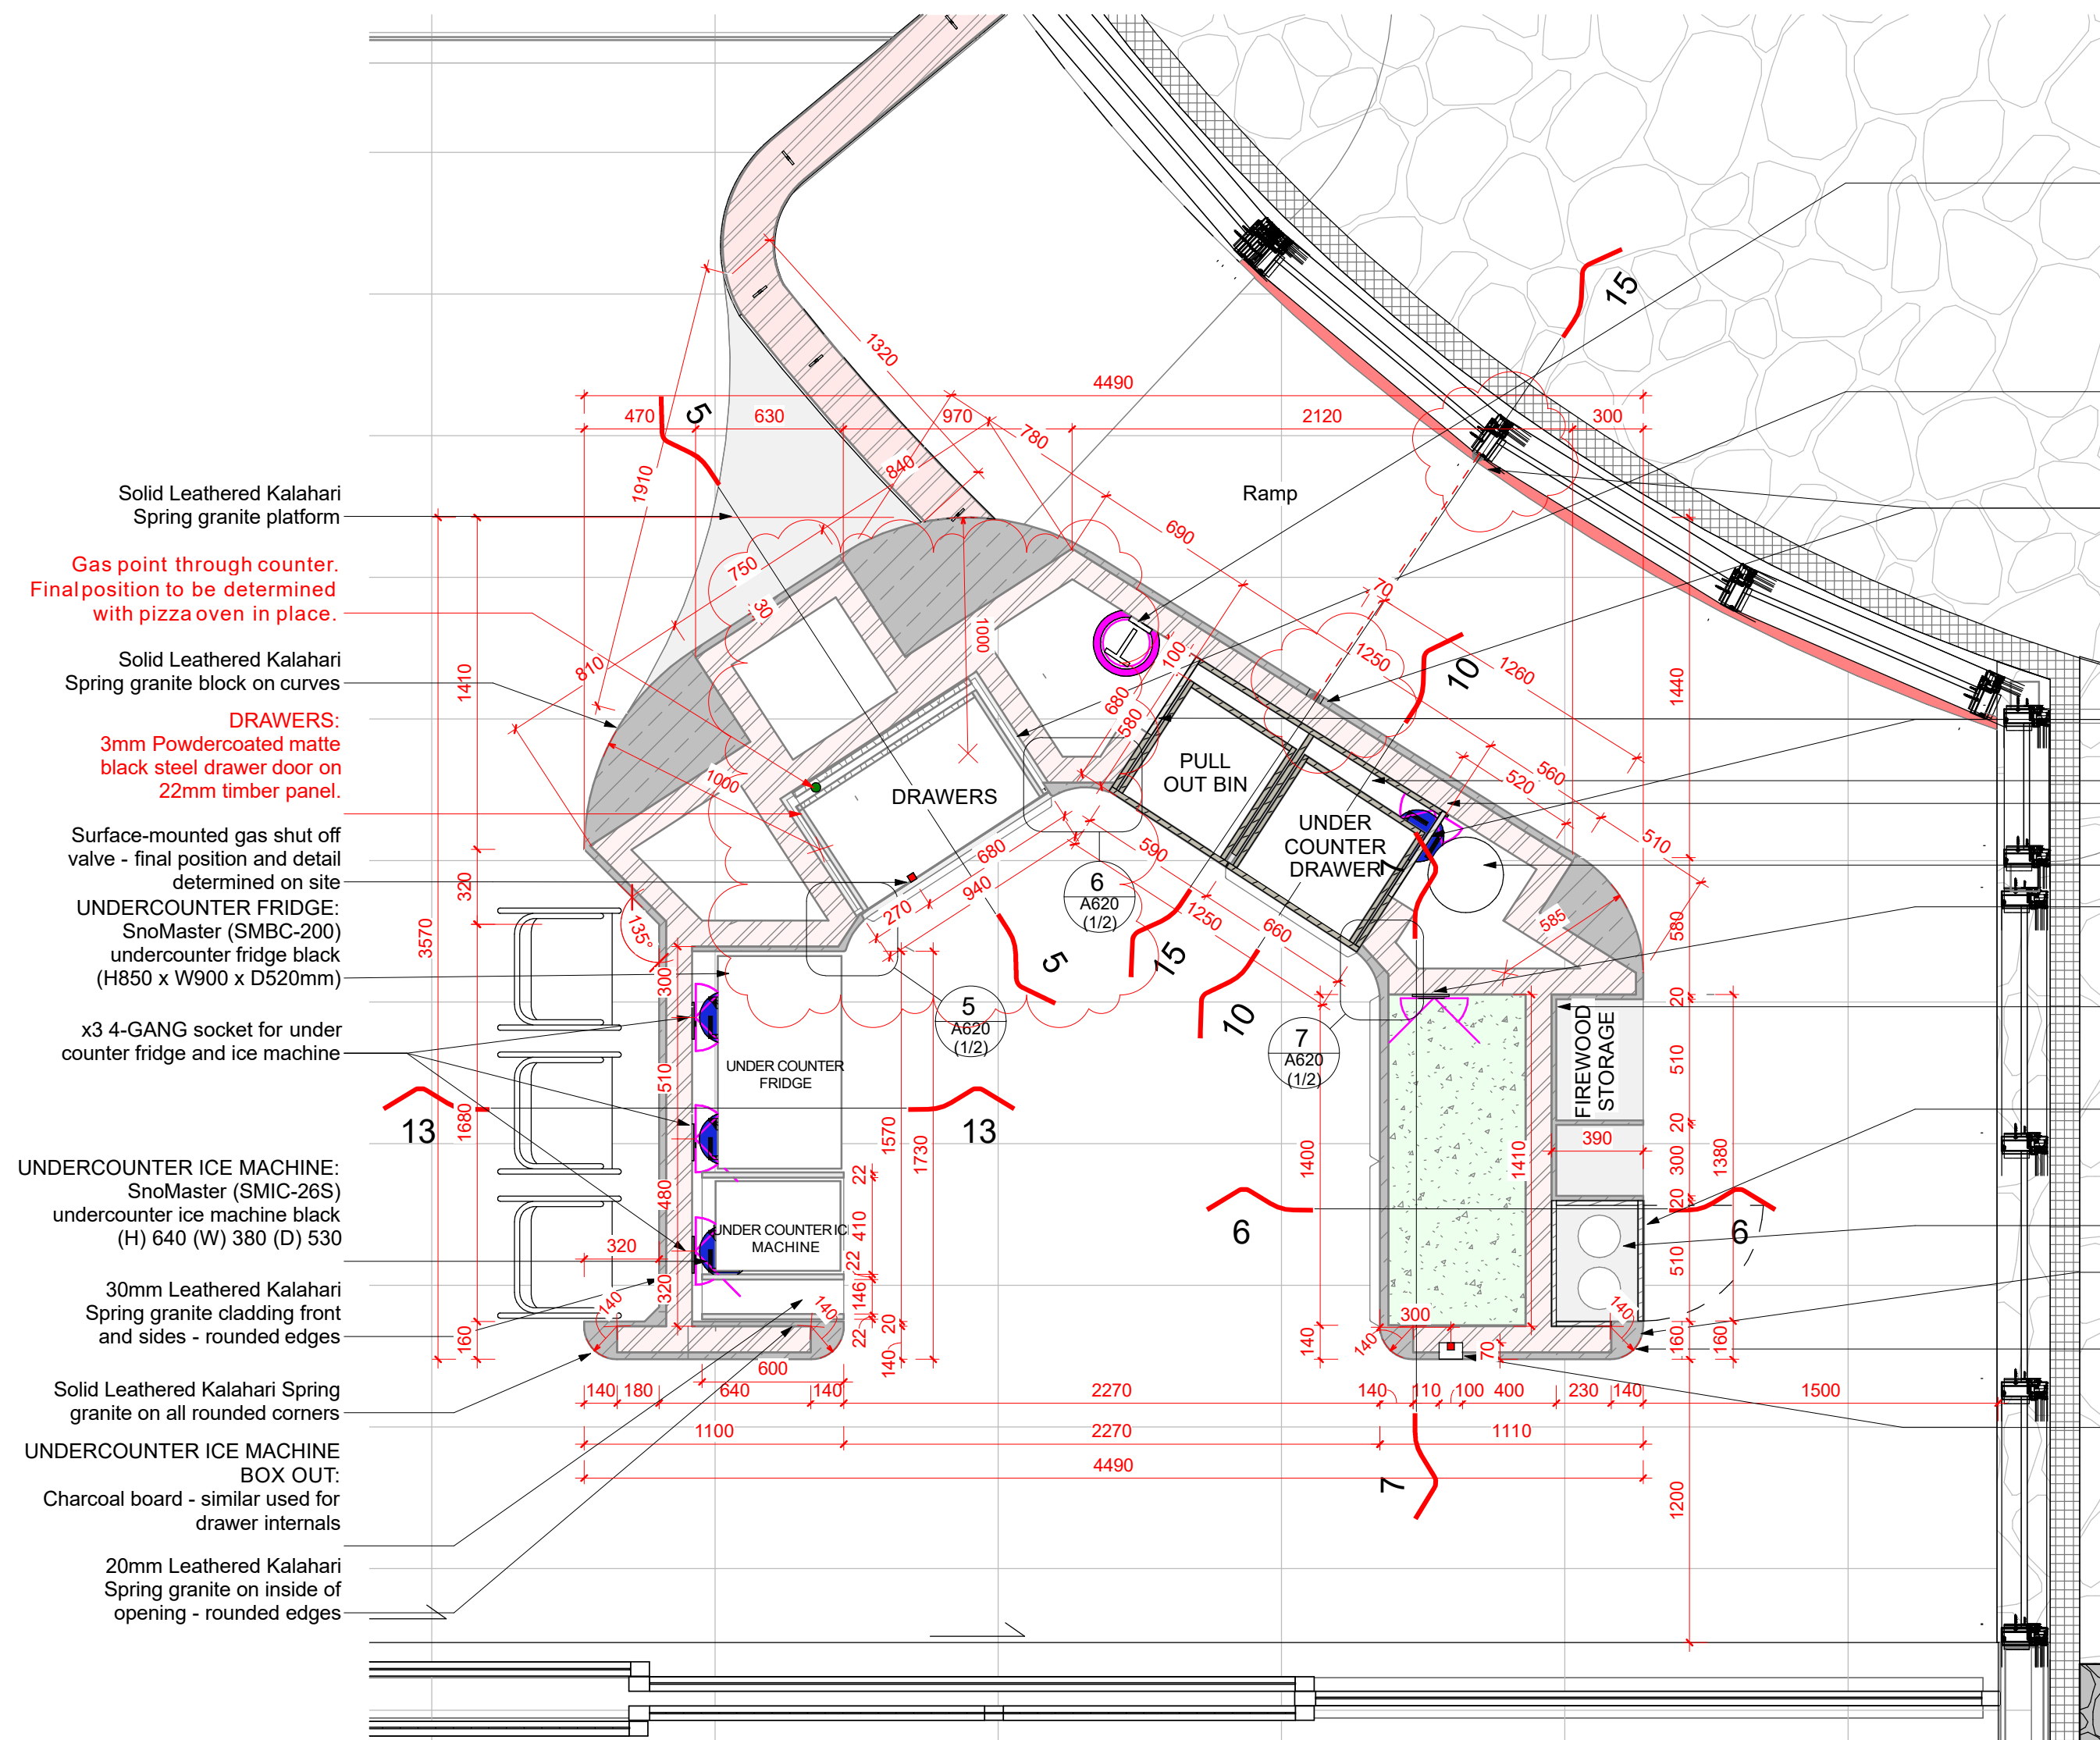

③ Plan Lower Level - Pavilion Cooking Station
1:25

Telephone point.
Hole in counter top for electric cord.
Access from inside of cupboard.

Inside of niche clad with
20mm Leathered Kalahari
Spring granite

Sensor for automatic door -
recessed on side of counter in
70 x 100mm cut out
Sensor on aluminum frame to
line up in height - see Section
05/View 15 on A620 (2/2)

Removeable panel to access
electrics and quick hot

4-GANG socket for quick hot
Drawer and pull out bin to be
freestanding unit that slides in

Geyser

Socket to side of wall


Inside of niche clad with
20mm Leathered Kalahari
Spring granite on brickwork

Cupboard door with 3mm
powdercoated matte black
steel door on 22mm panel
and angled steel handle

Fire extinguisher

Brickwall clad with 30mm
Leathered Kalahari Spring
granite and rounded corners
Corners to have rounded
solid edges

Recessed gas shut off
valve.
See detail 12.

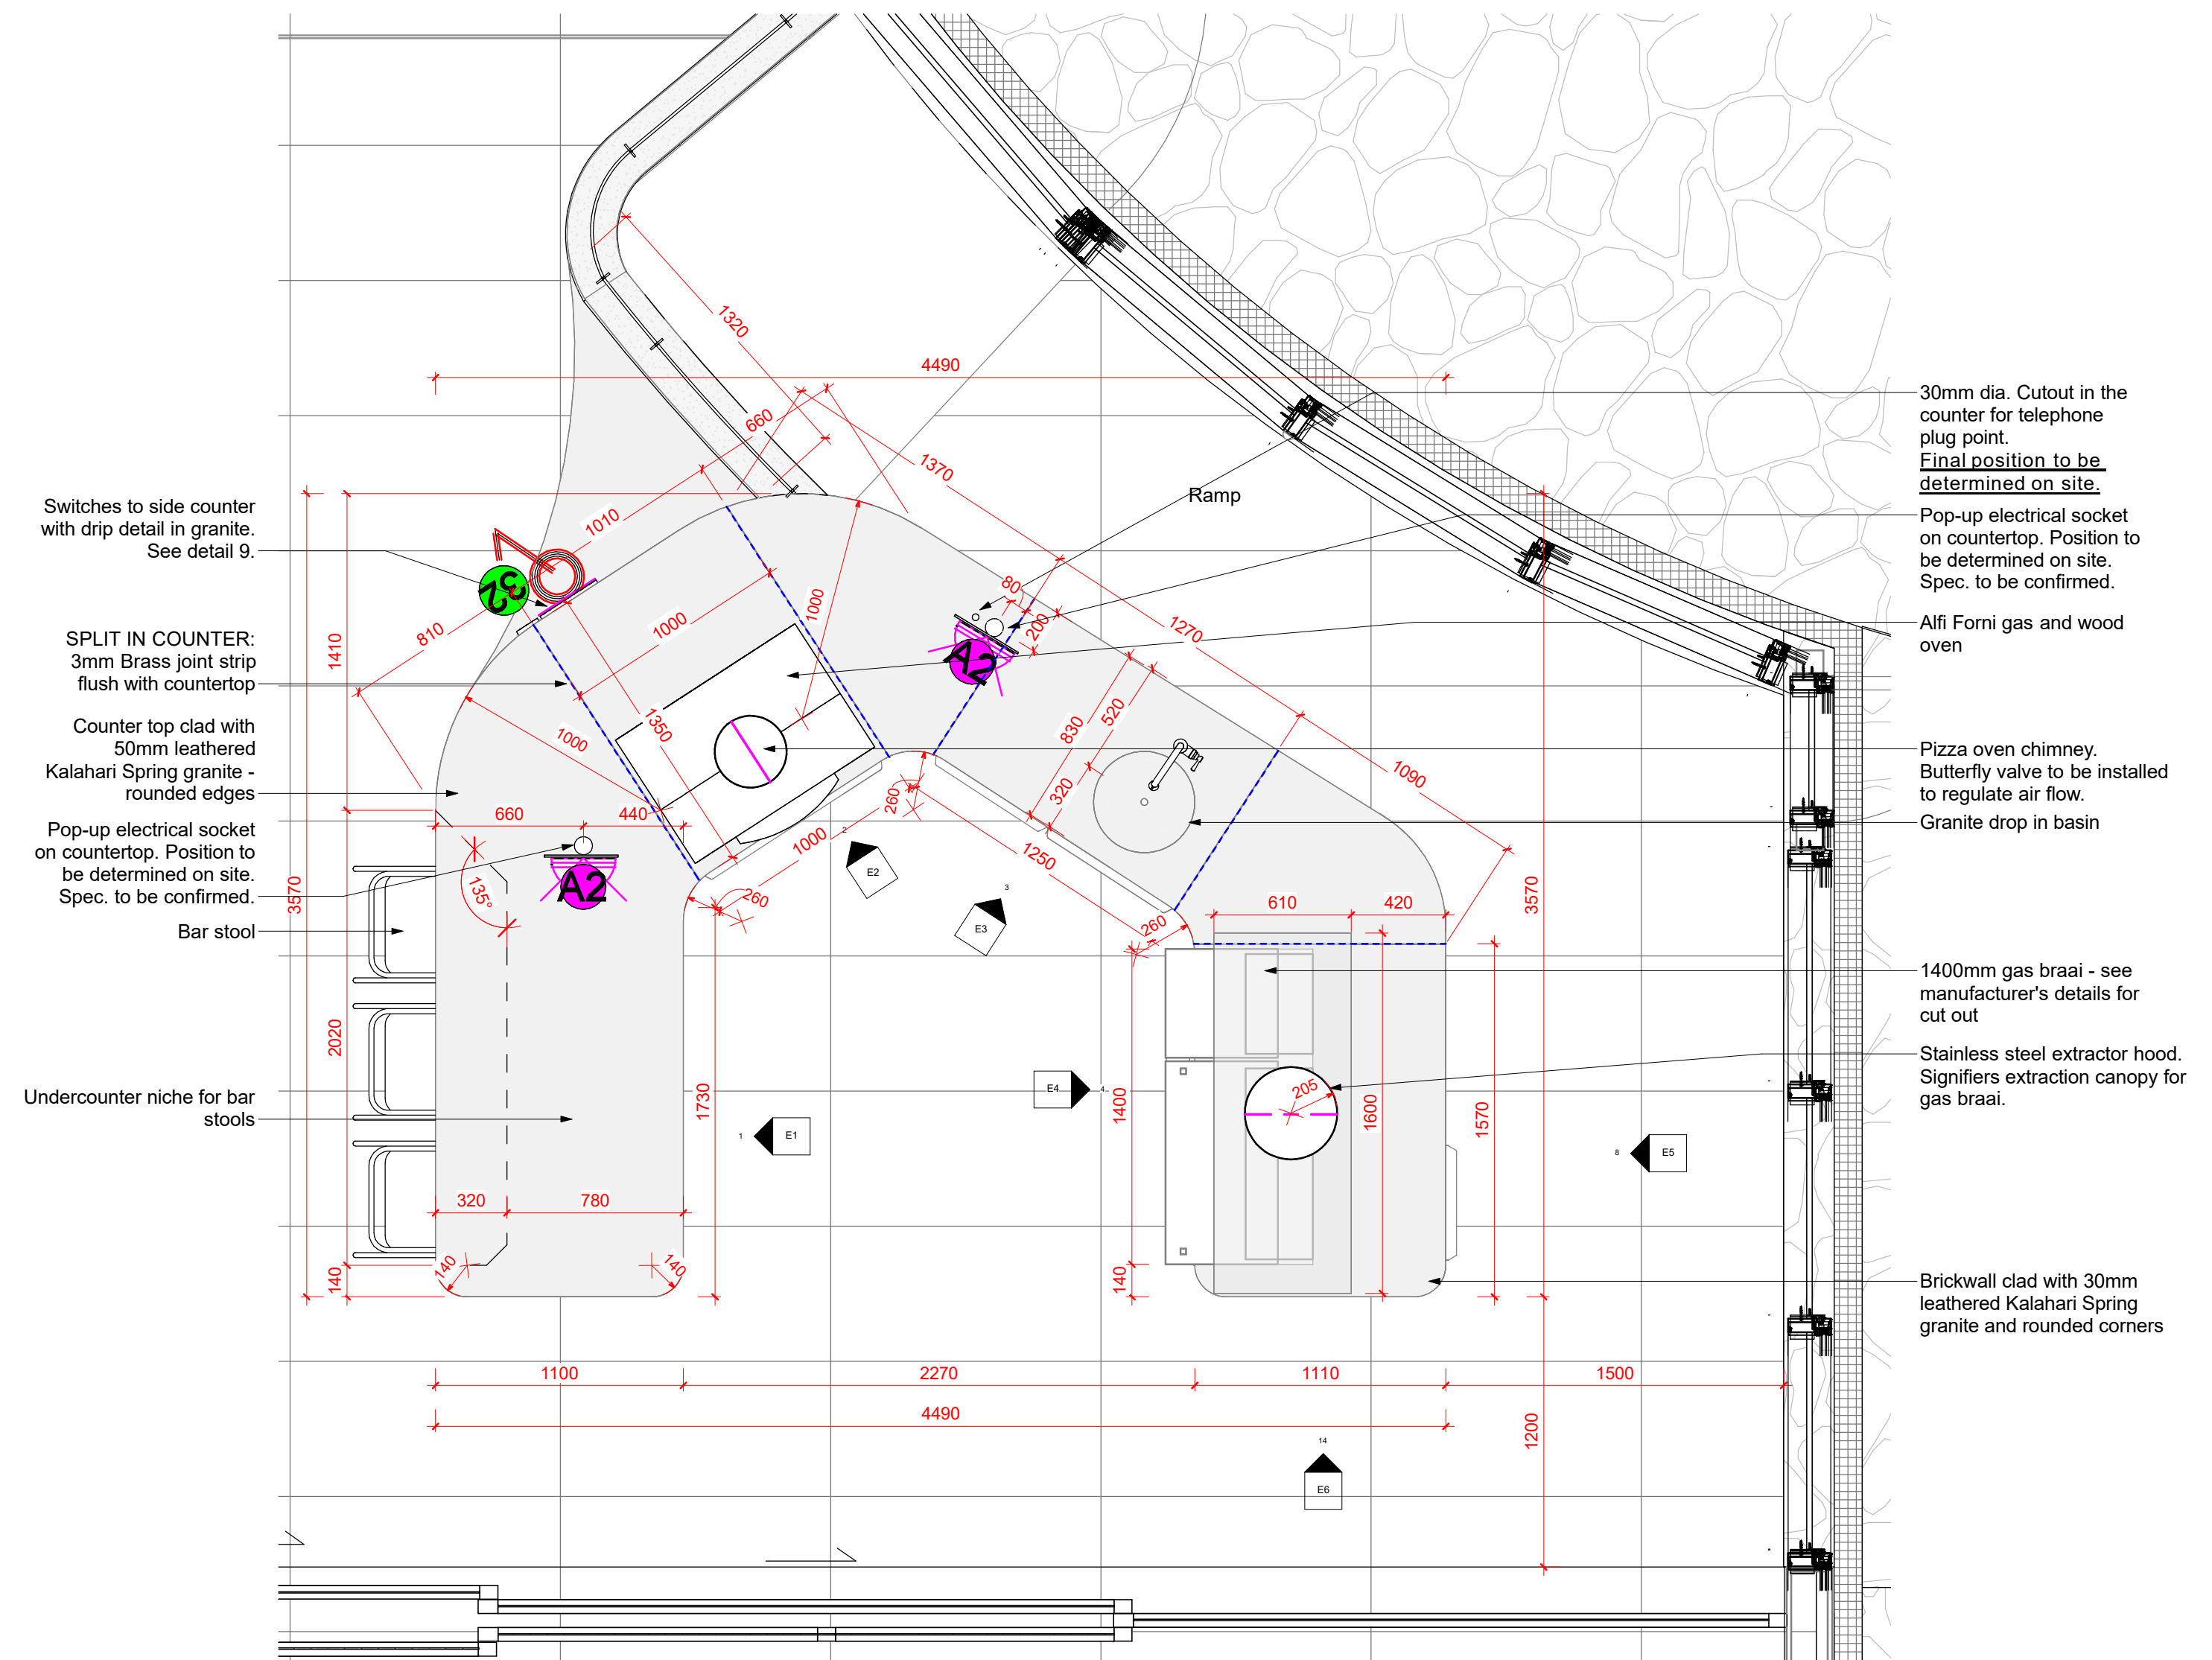

④ Plan Upper Level - Pavilion Cooking Station
1:25

30mm dia. Cutout in the
counter for telephone
plug point.
Final position to be
determined on site.

Pop-up electrical socket
on countertop. Position to
be determined on site.
Spec. to be confirmed.

Alfi Forni gas and wood
oven


Pizza oven chimney.
Butterfly valve to be installed
to regulate air flow.
Granite drop in basin

1400mm gas braai - see
manufacturer's details for
cut out


Stainless steel extractor hood.
Signifiers extraction canopy for
gas braai.

Brickwall clad with 30mm
leathered Kalahari Spring
granite and rounded corners


Pavilion BBQ Counter Detail

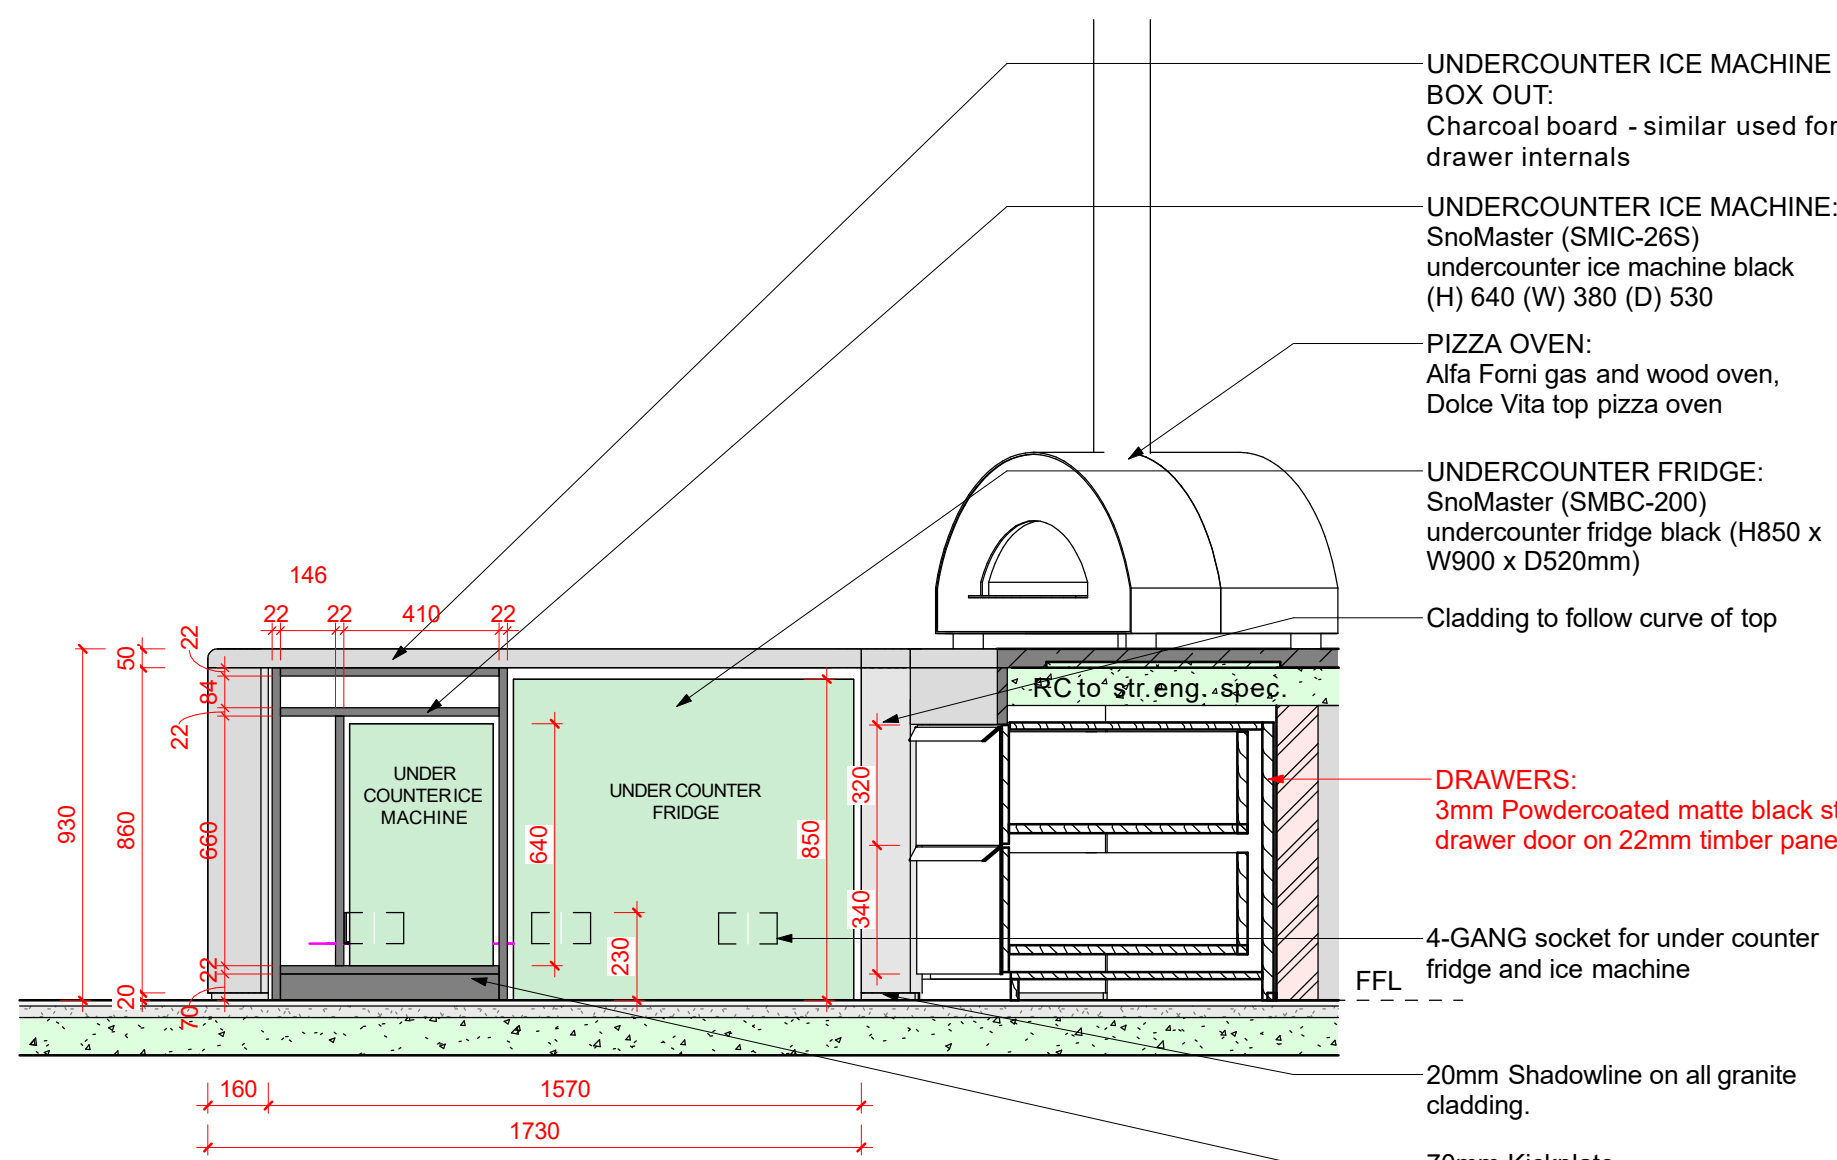


① Elevation 01 - Fridge & Freezer
1 : 20

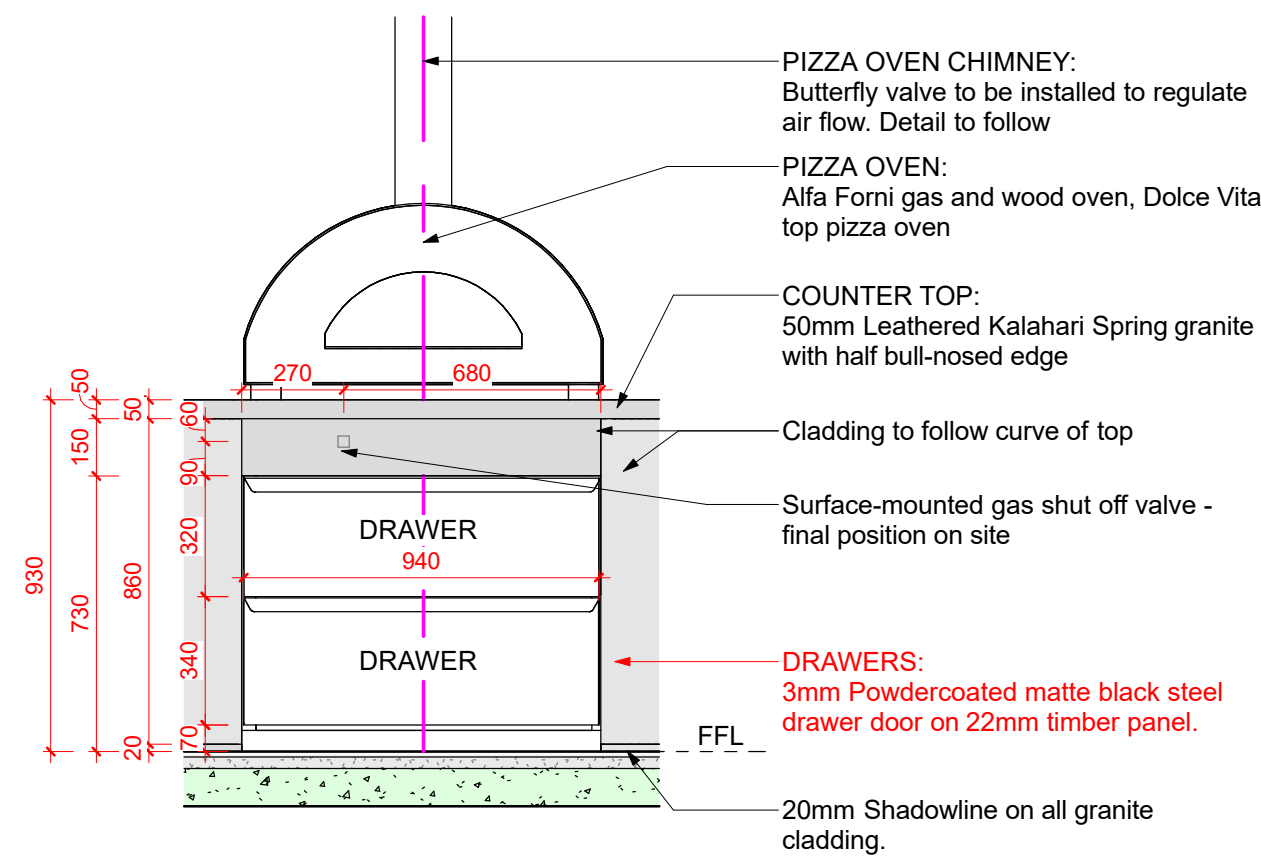


② Elevation 02 - Pizza Oven
1 : 20

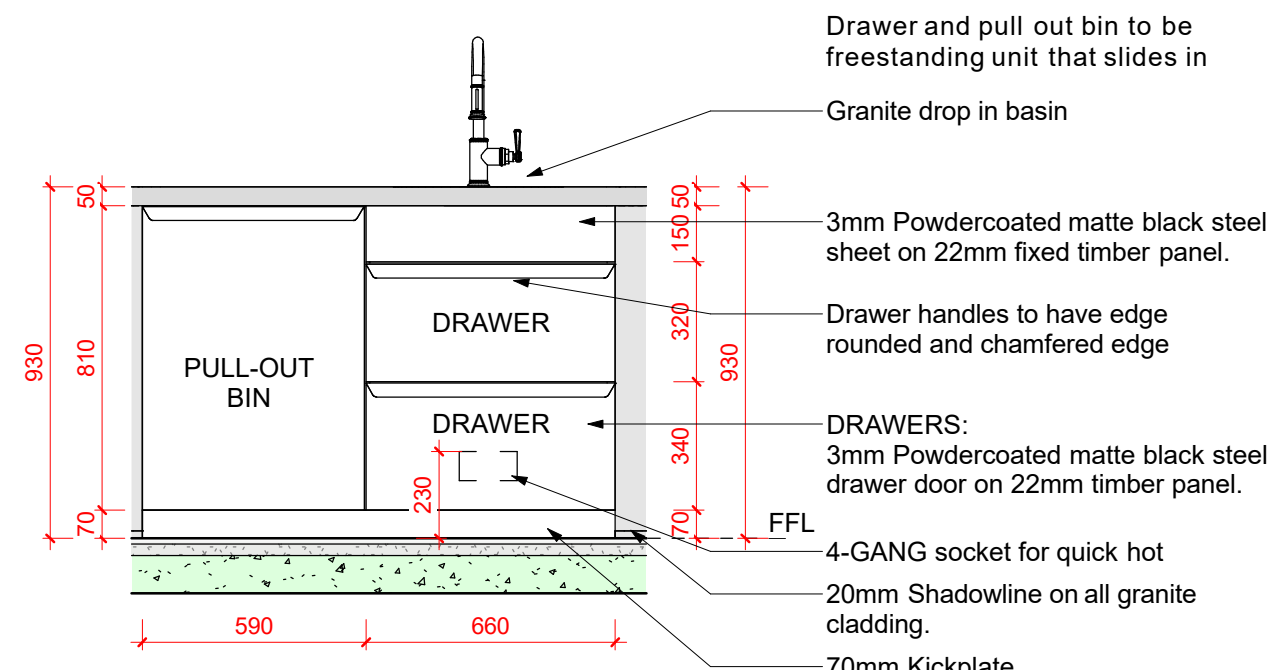


③ Elevation 03 - Drawers, Bin & Basin
1 : 20

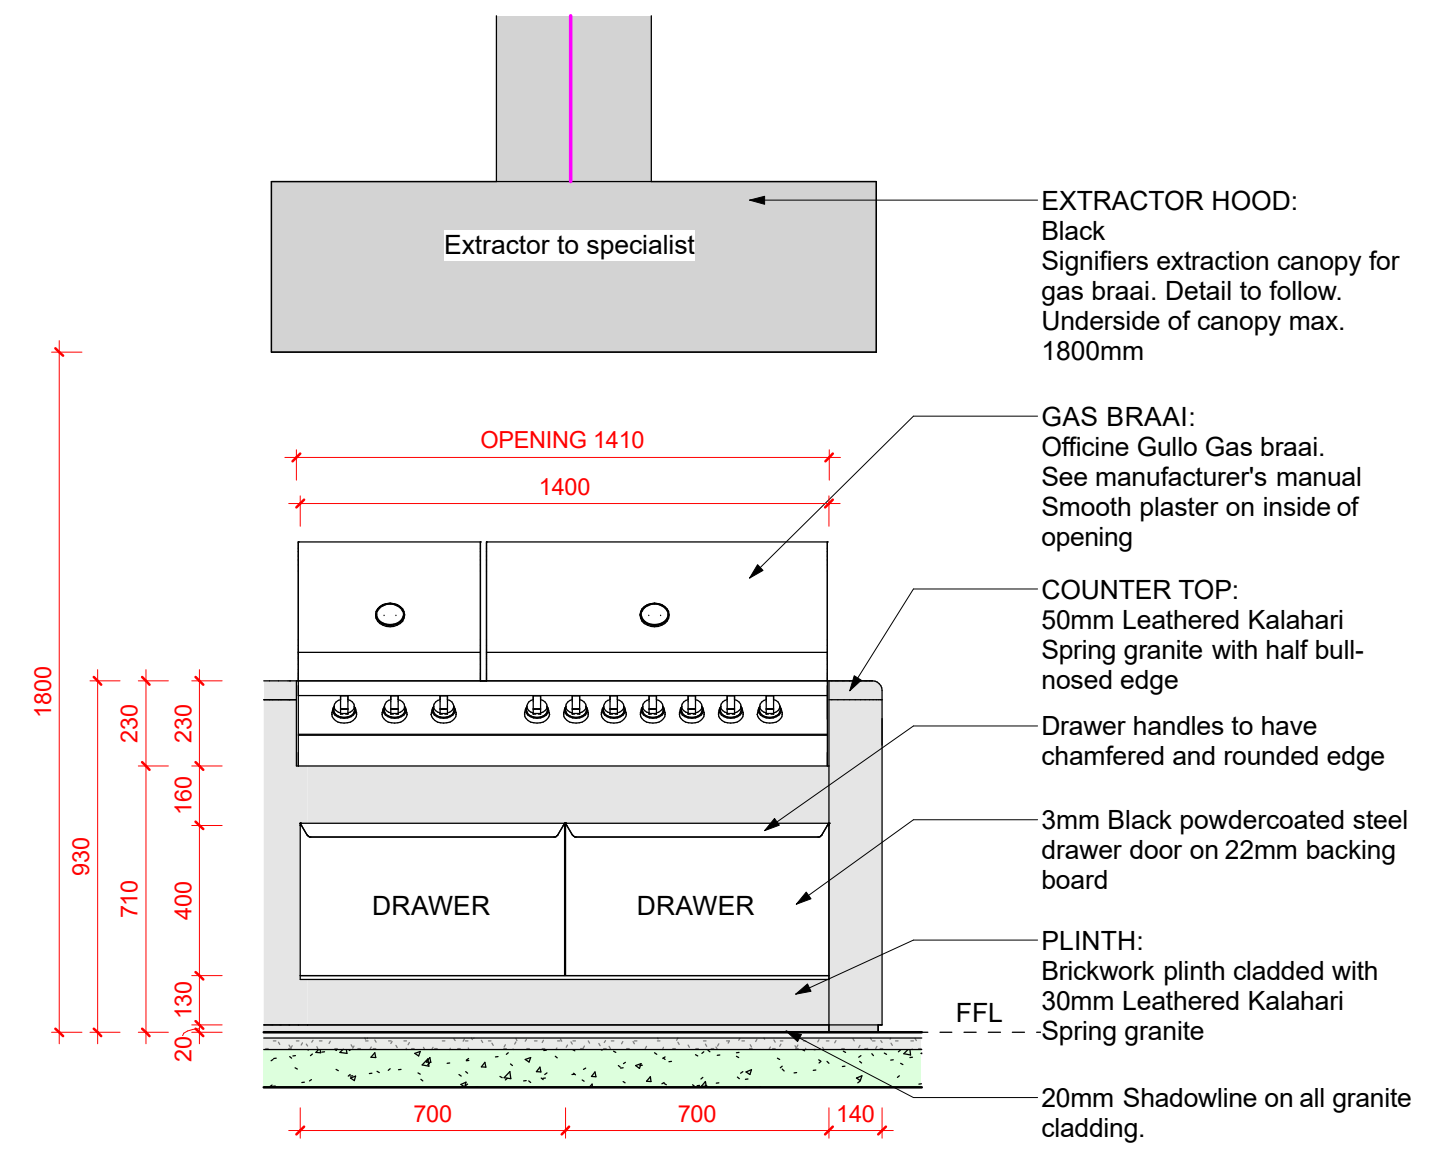


④ Elevation 04 - Gas Braai & Extractor
1 : 20

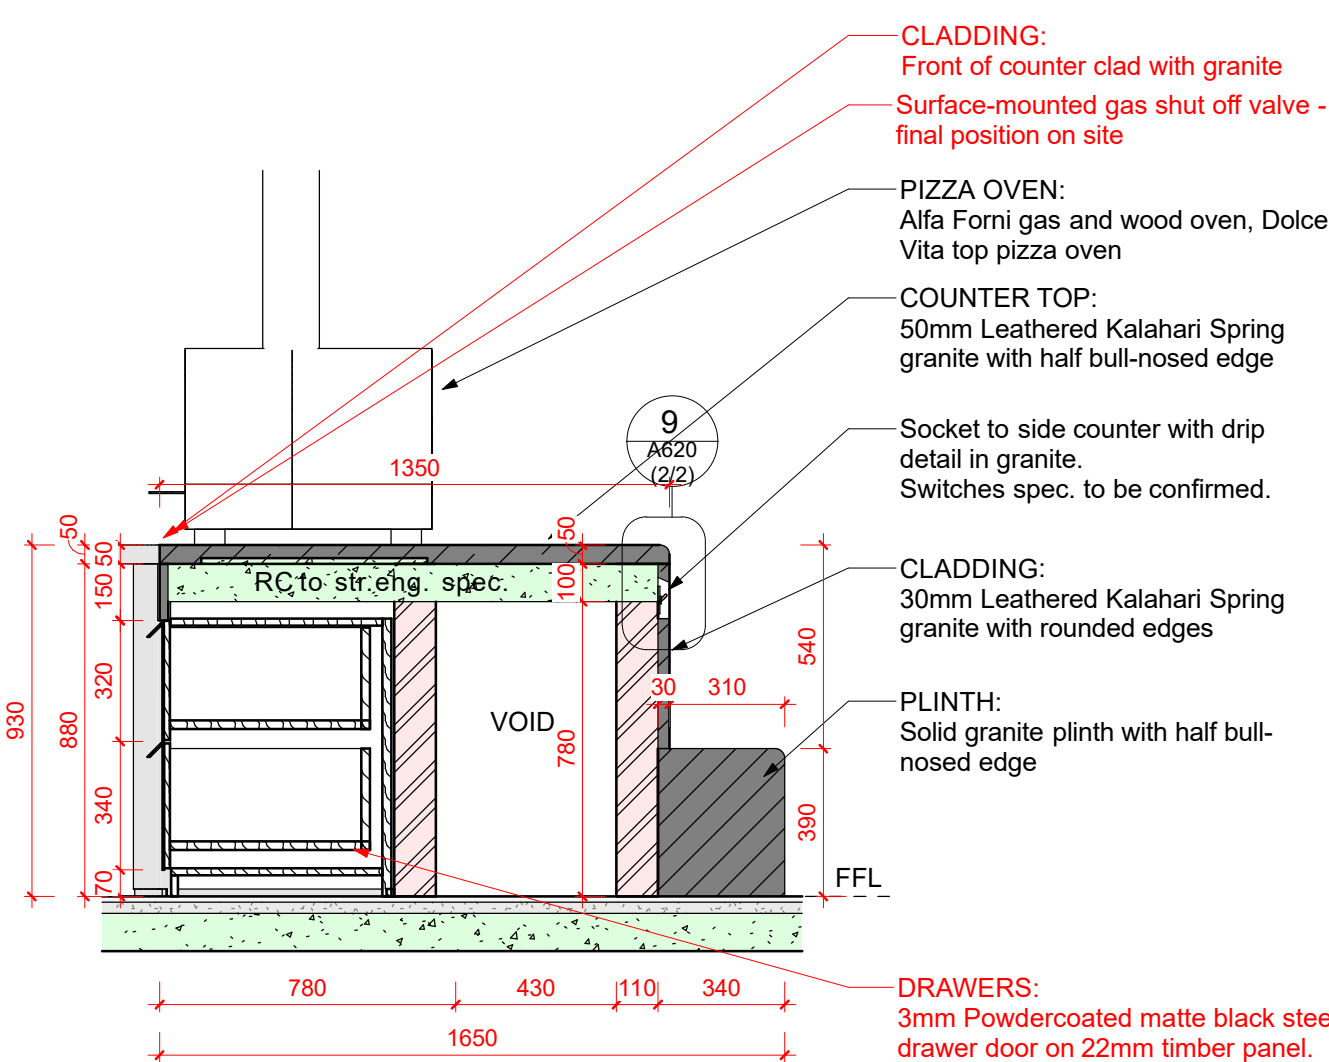


⑤ Section 01 - Pizza Oven & Pull-out Trolley
1 : 20

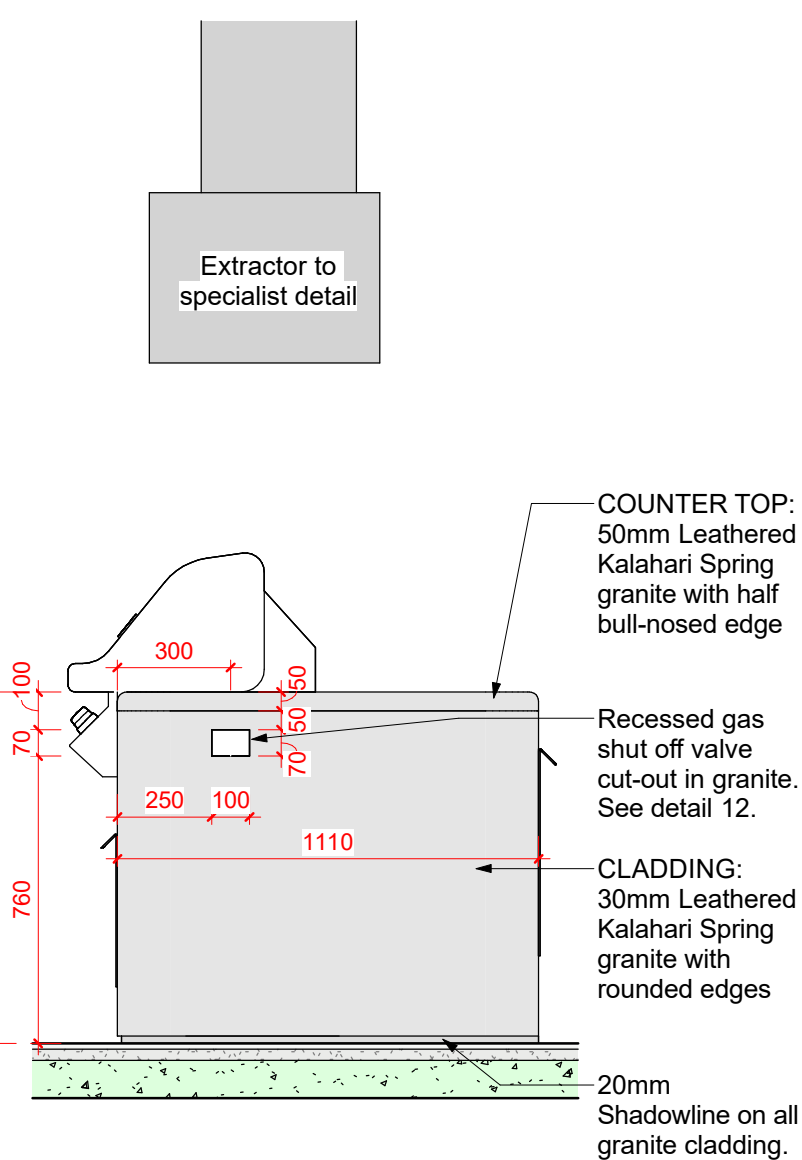


⑭ Elevation 06 - Gas Shut off valve
1 : 20

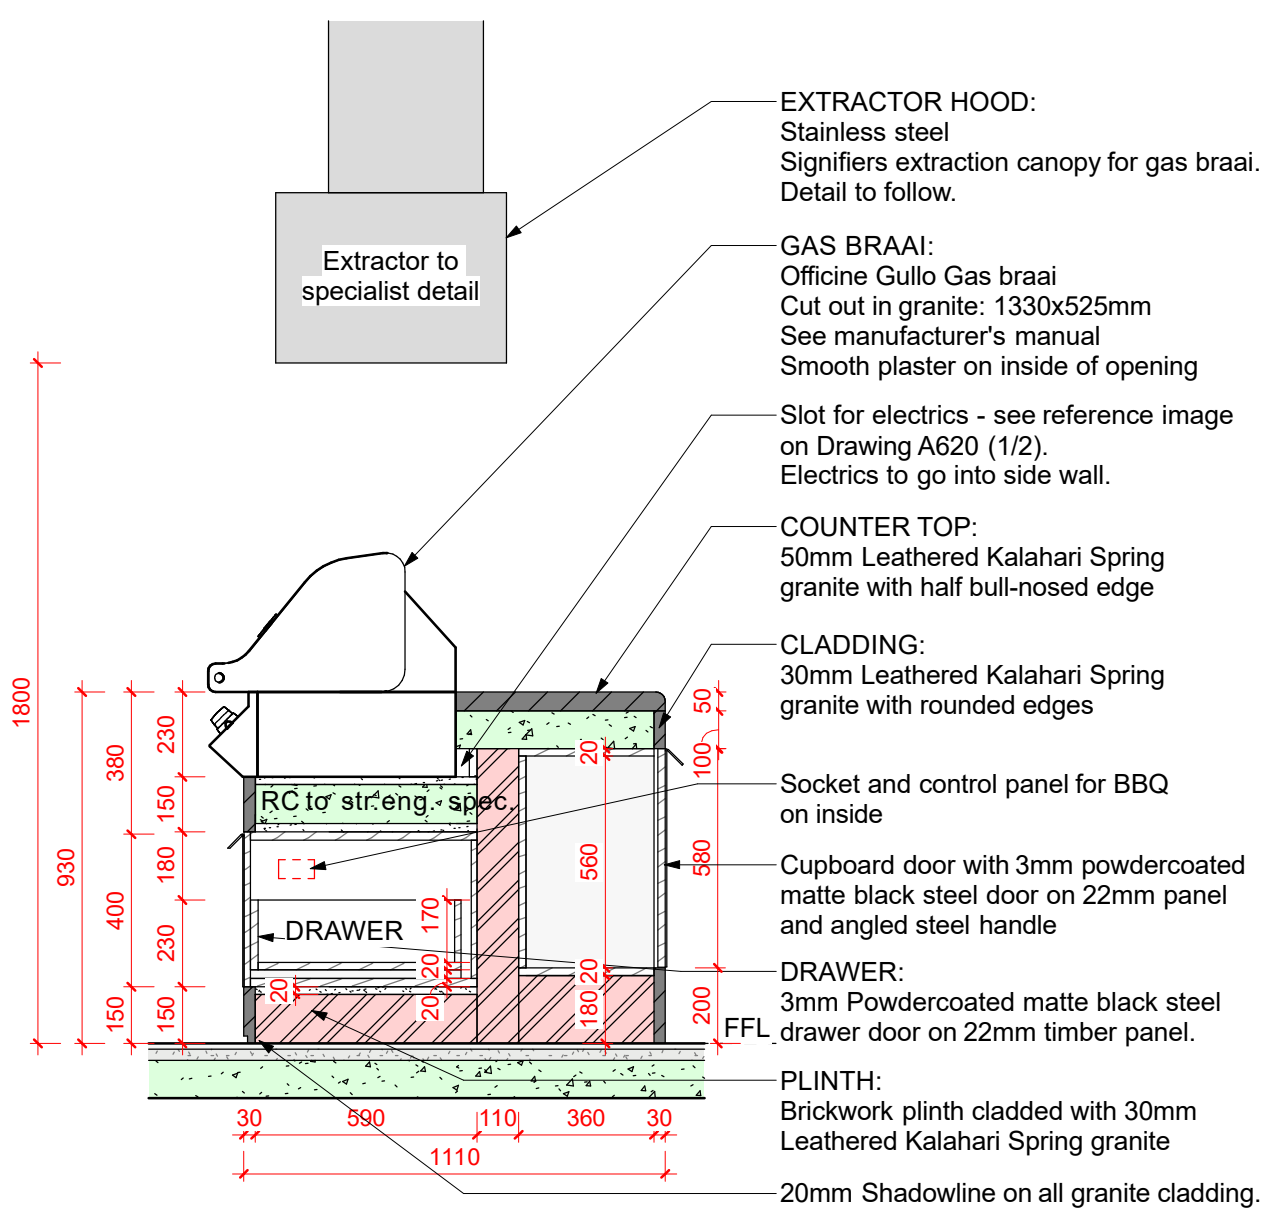


⑥ Section 02 - Gas Oven & Drawers
1 : 20

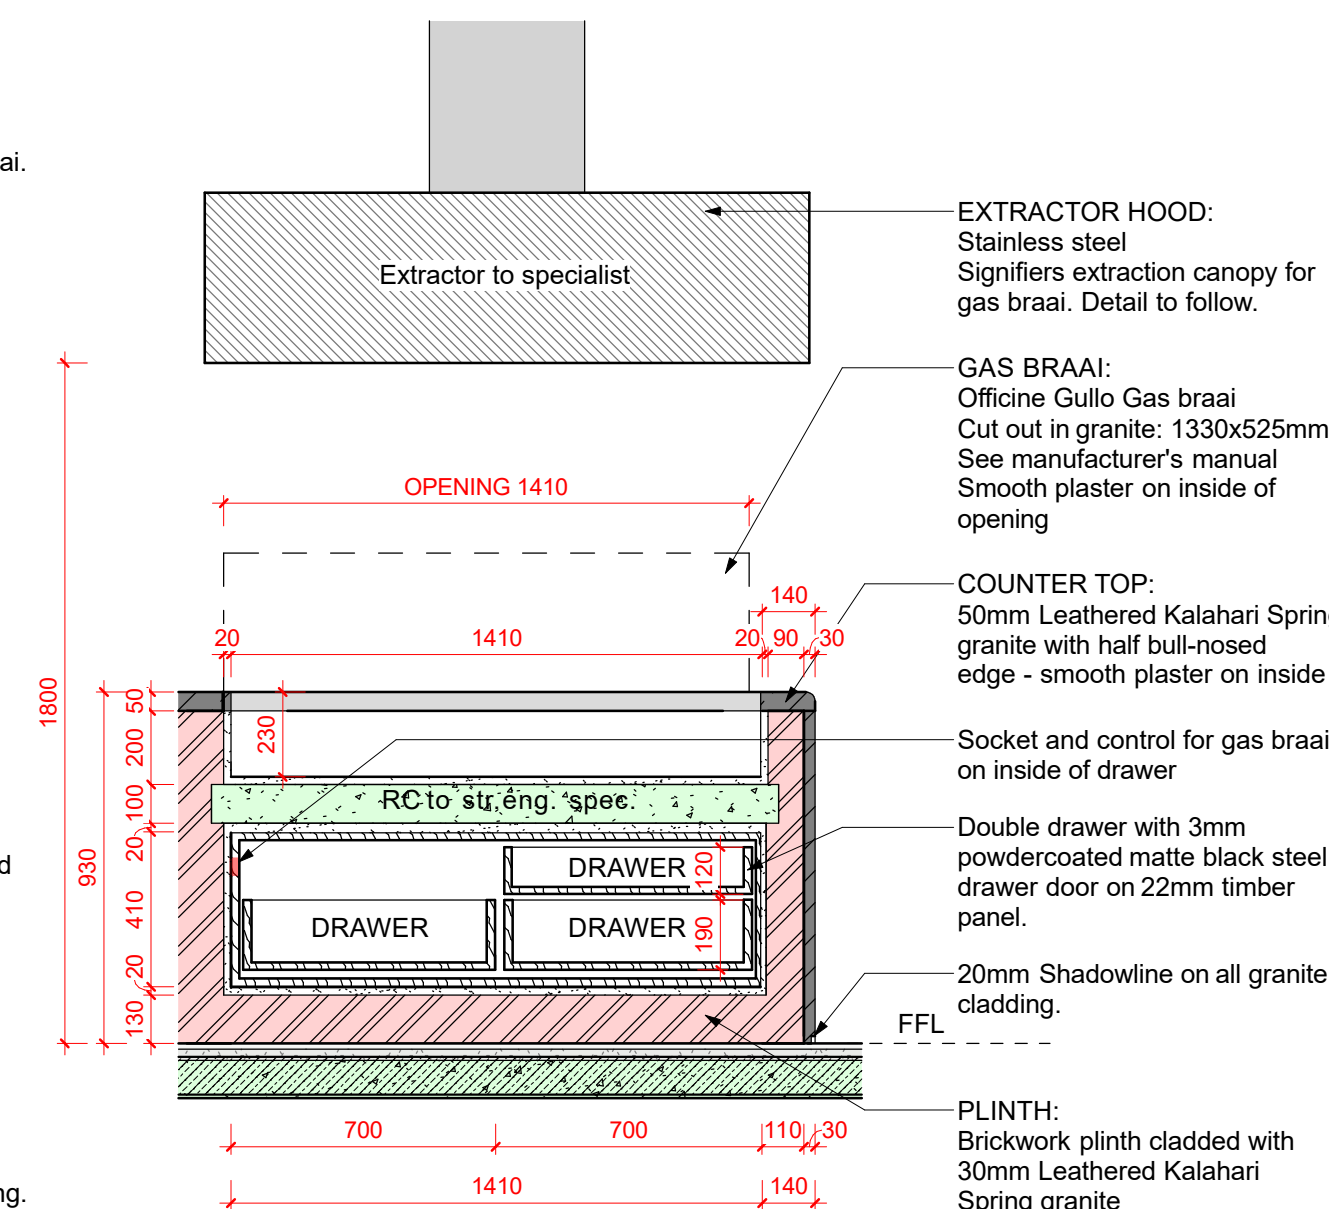


⑦ Section 03 - Gas Oven & Drawers
1 : 20

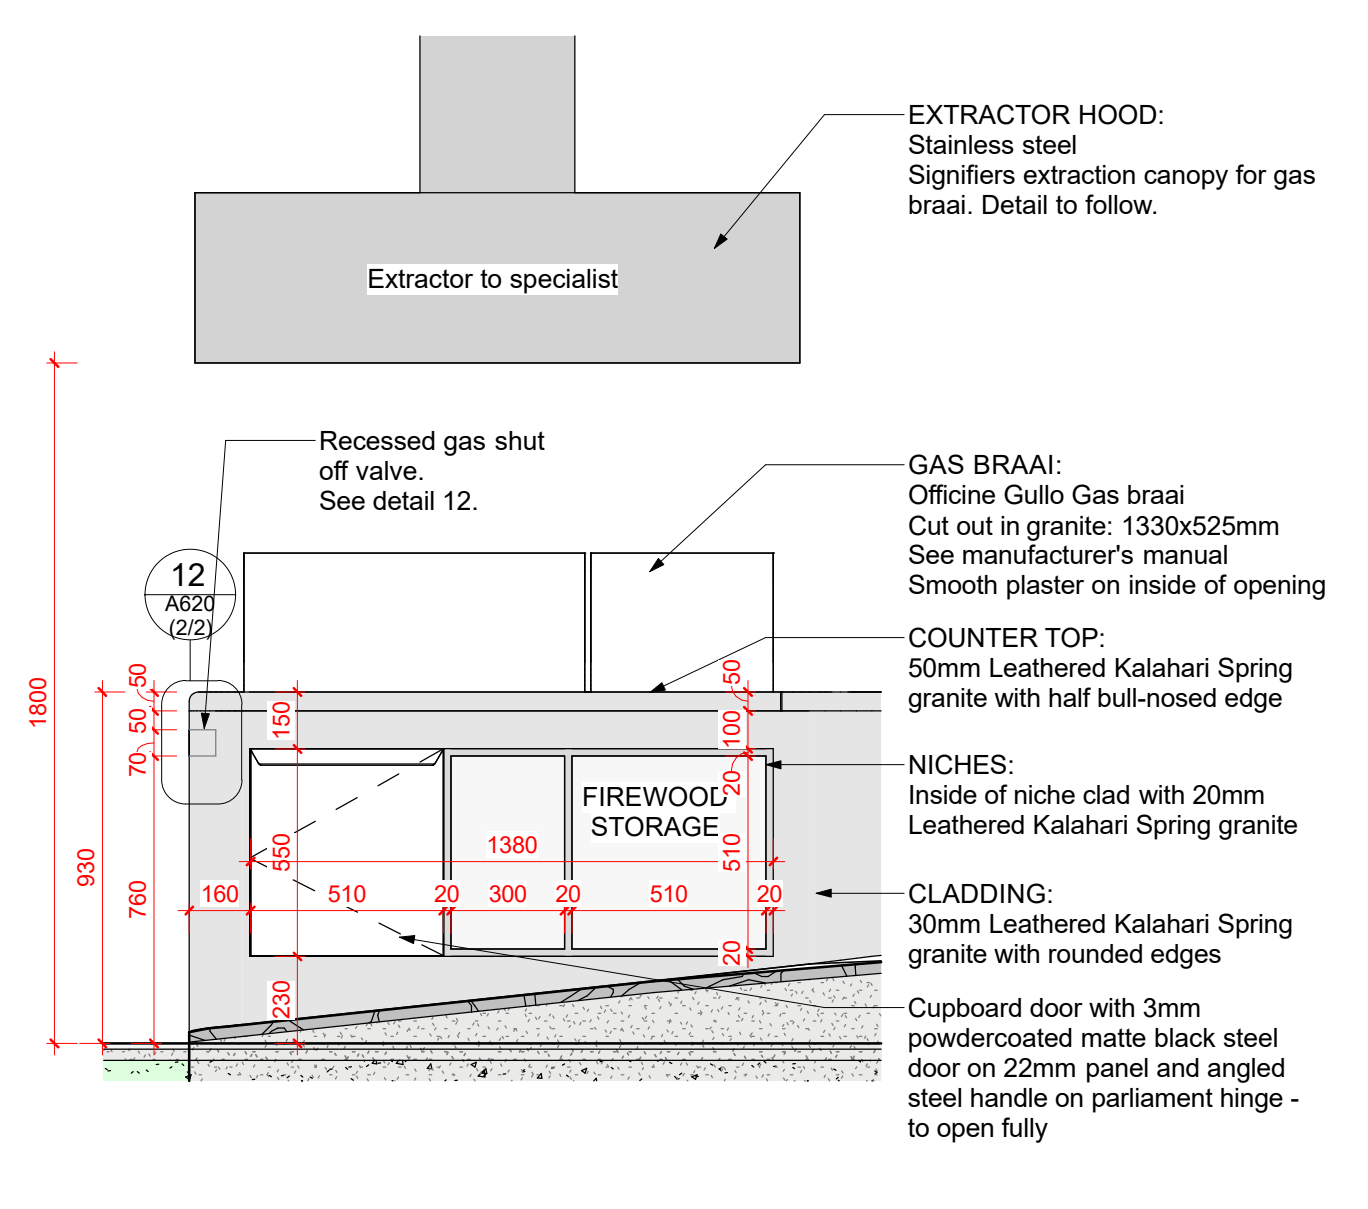


⑧ Elevation 05 - Fire Extinguisher Cabinet and Firewood Storage
1 : 20

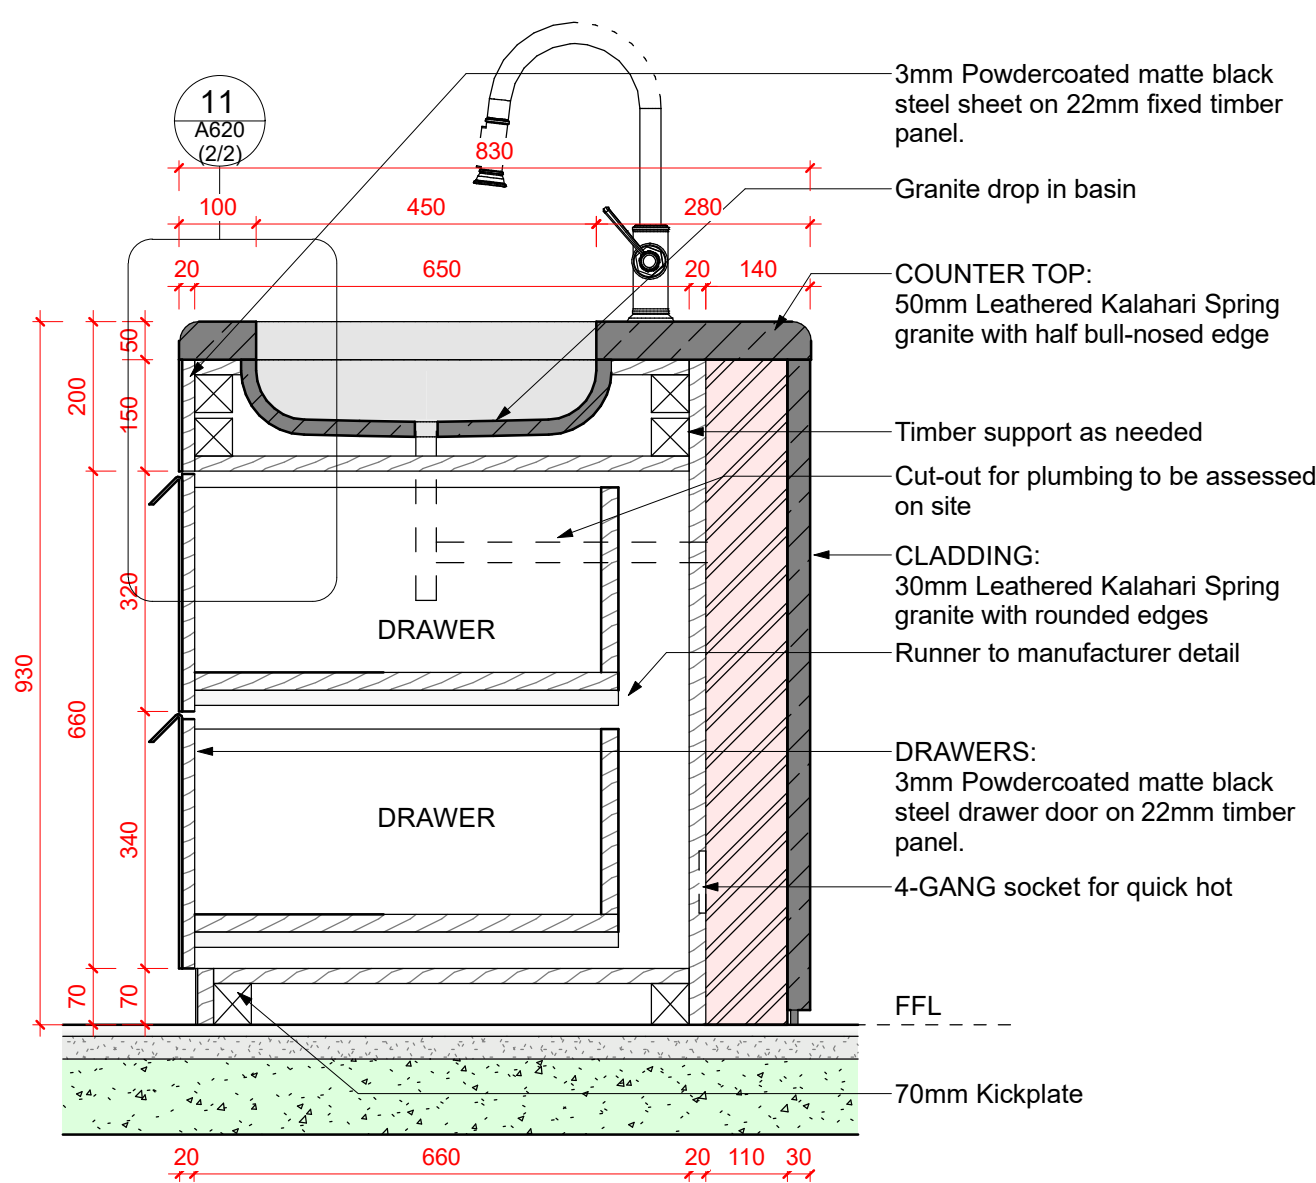


⑩ Section 04 - Drawers
1 : 10

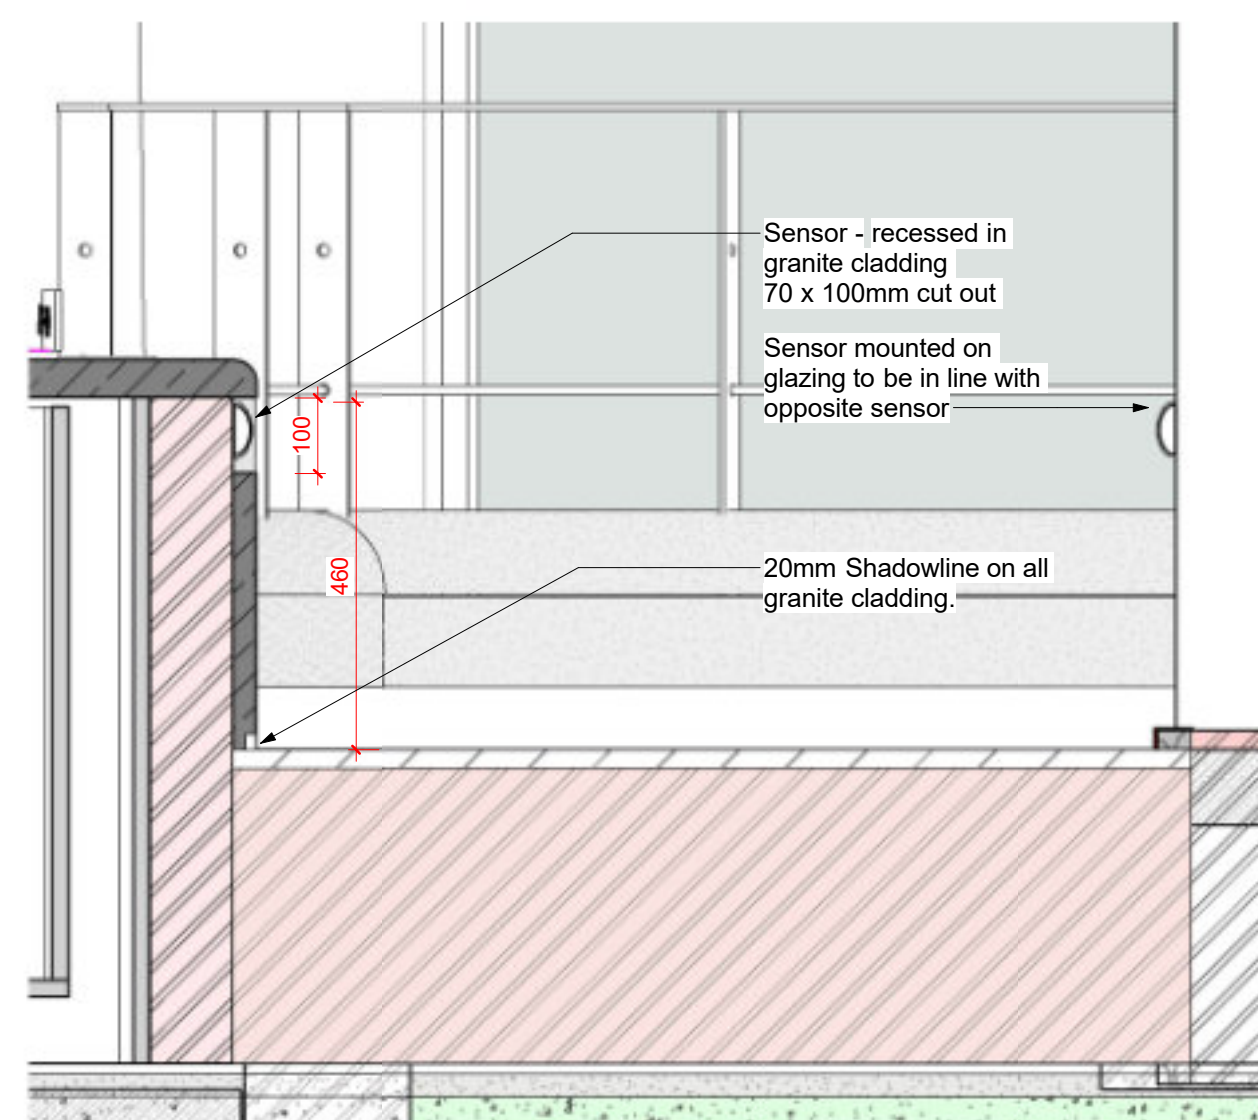


⑮ Section 05 - Sensor Position
1 : 10

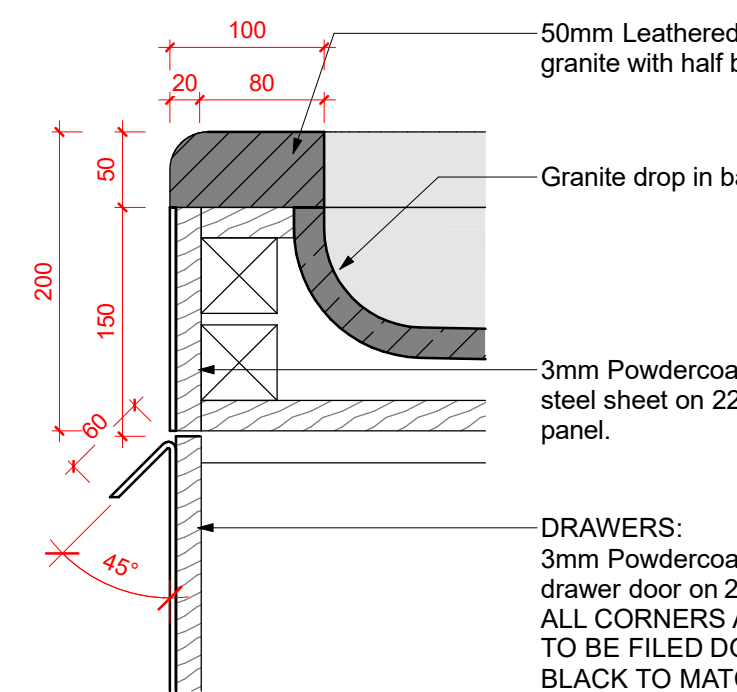


⑪ Callout - Recessed Panel for Sockets
1 : 5

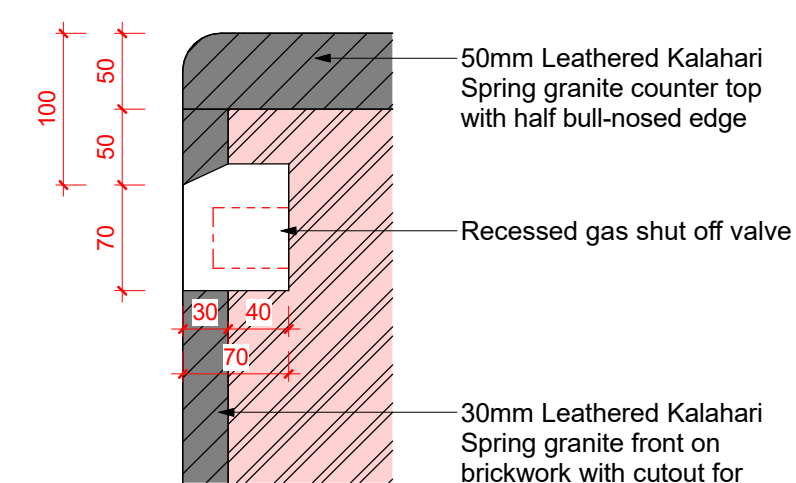

⑫ Callout - Recessed gas shut off valve
1 : 5

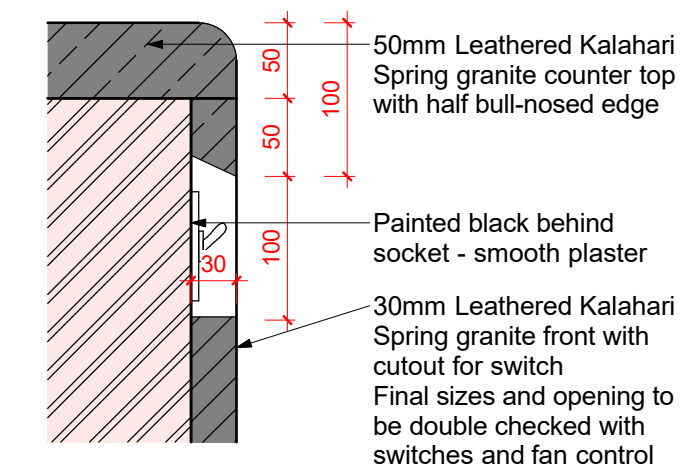

⑨ Callout - Switches cut out
1 : 5

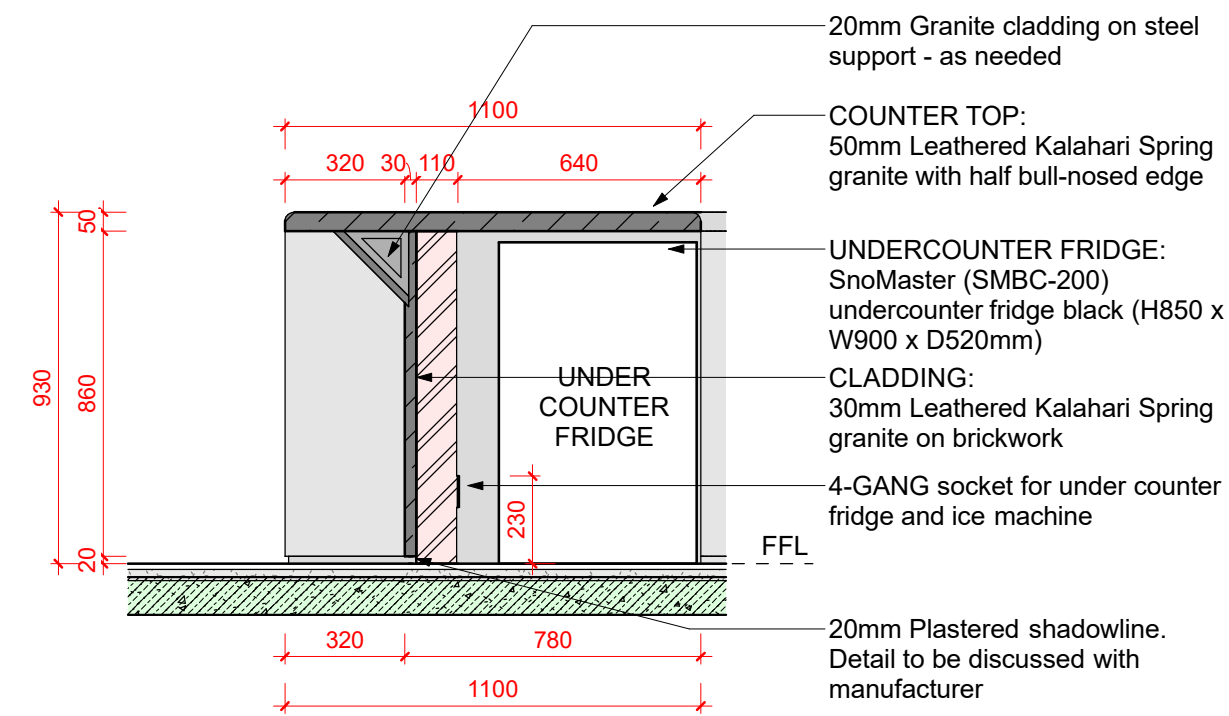

⑬ Section 06 - Bar Seating & Fridge
1 : 20

Pavilion BBQ Counter Detail