




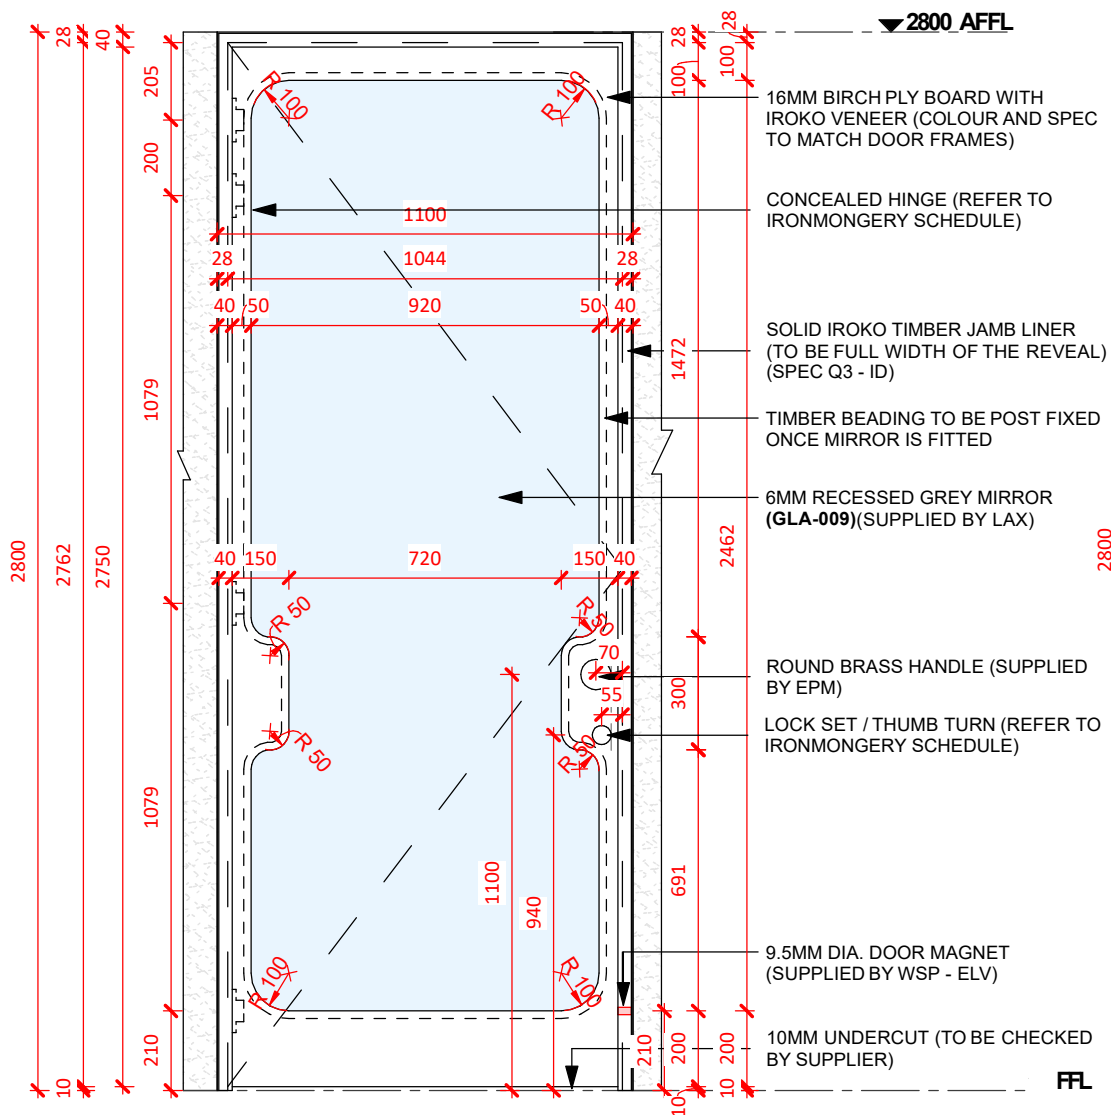


View A - Door Detail Elevation | 1:20

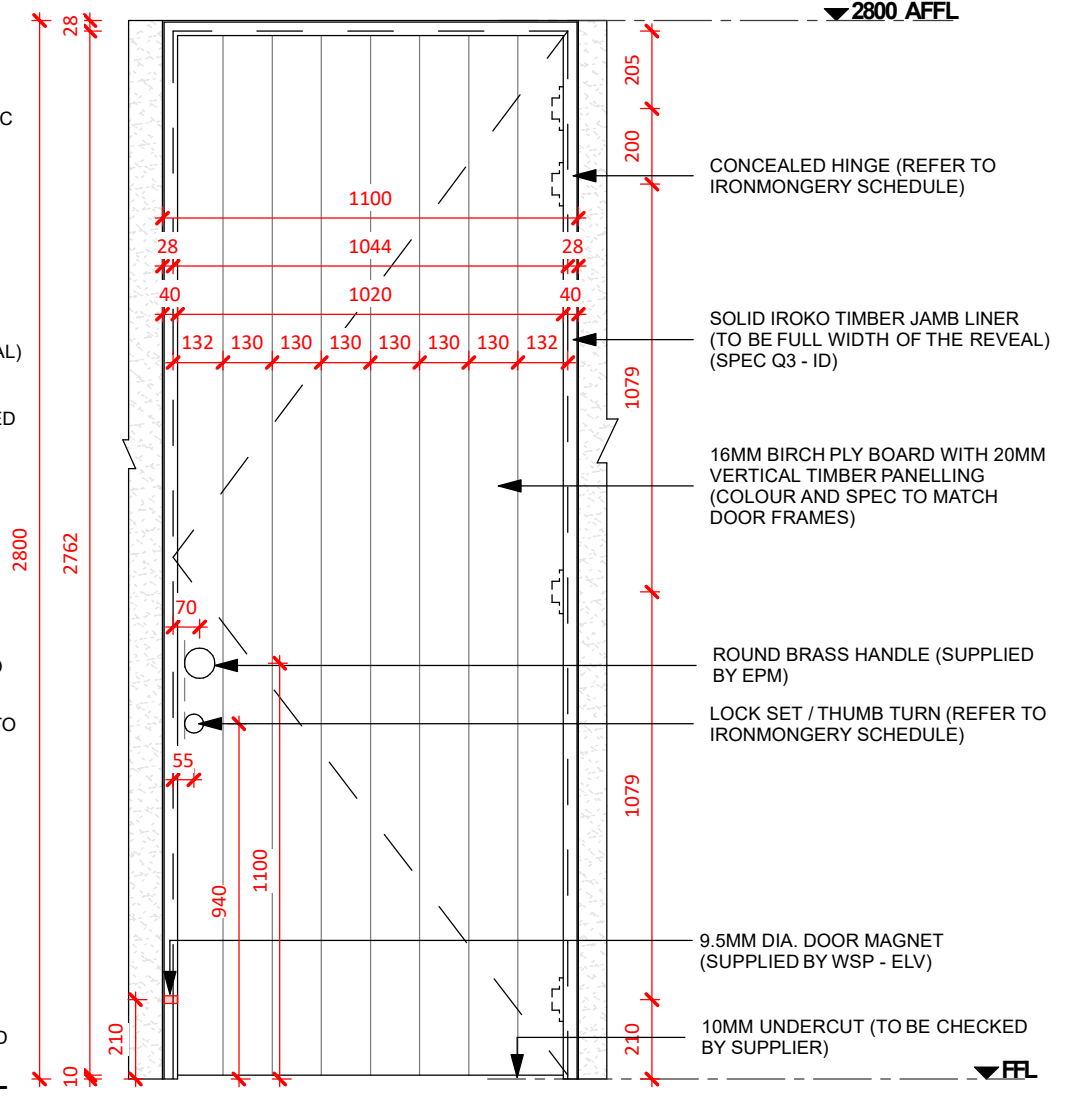


View B - Door Detail Elevation | 1:20

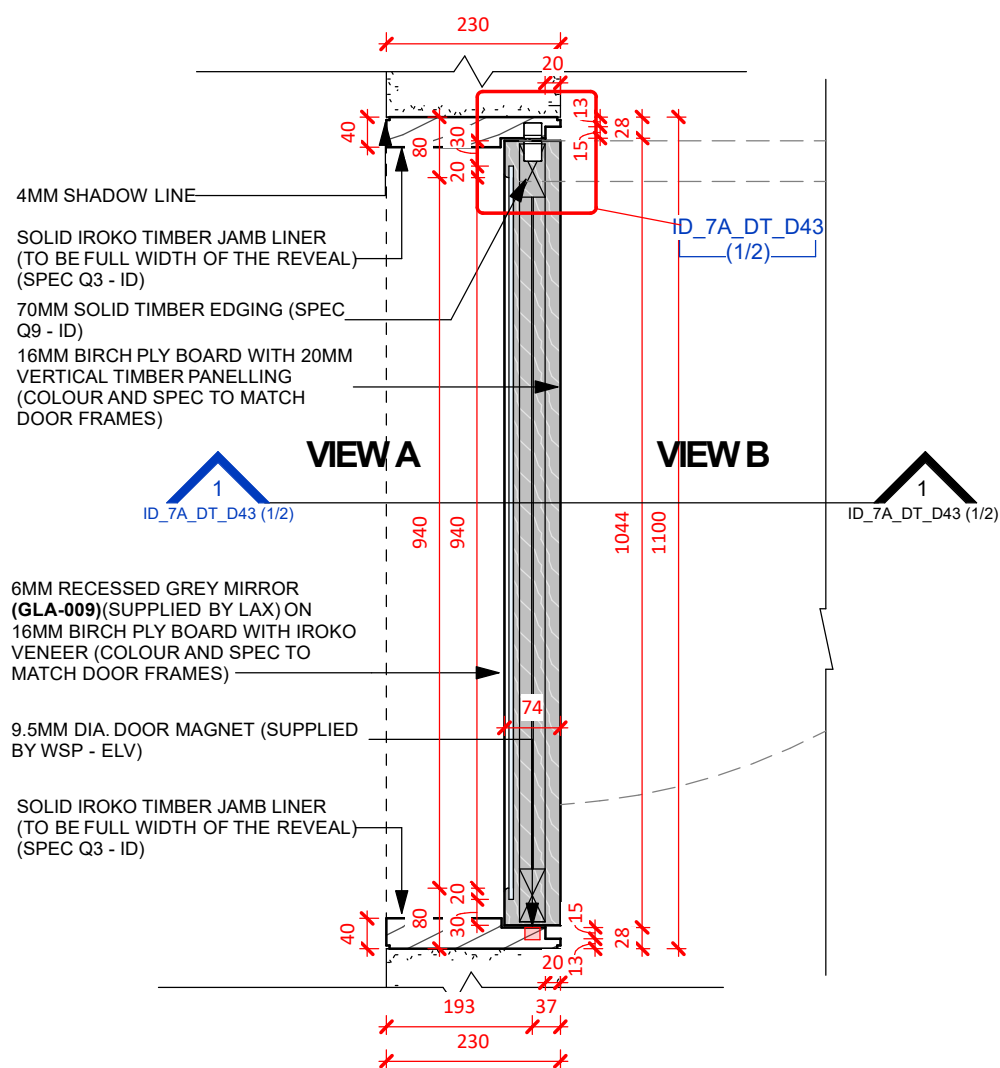


Plan - Single Hinge Door | 1:10

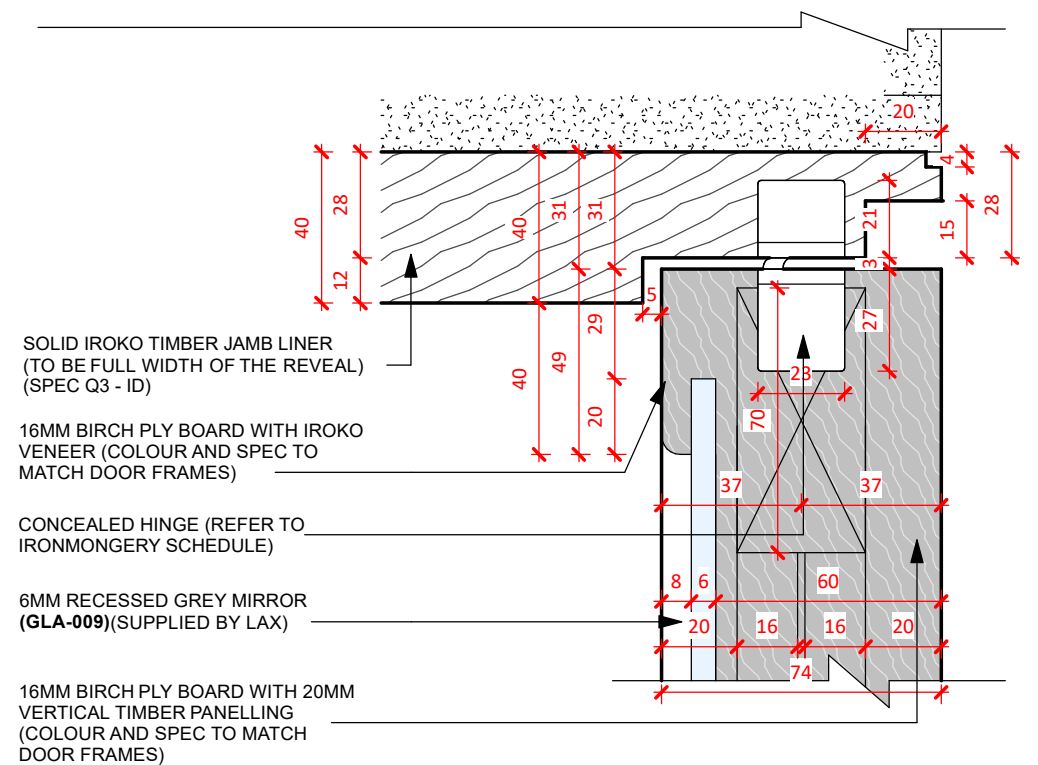

Detail Plan - Single Hinge Door | 1:2

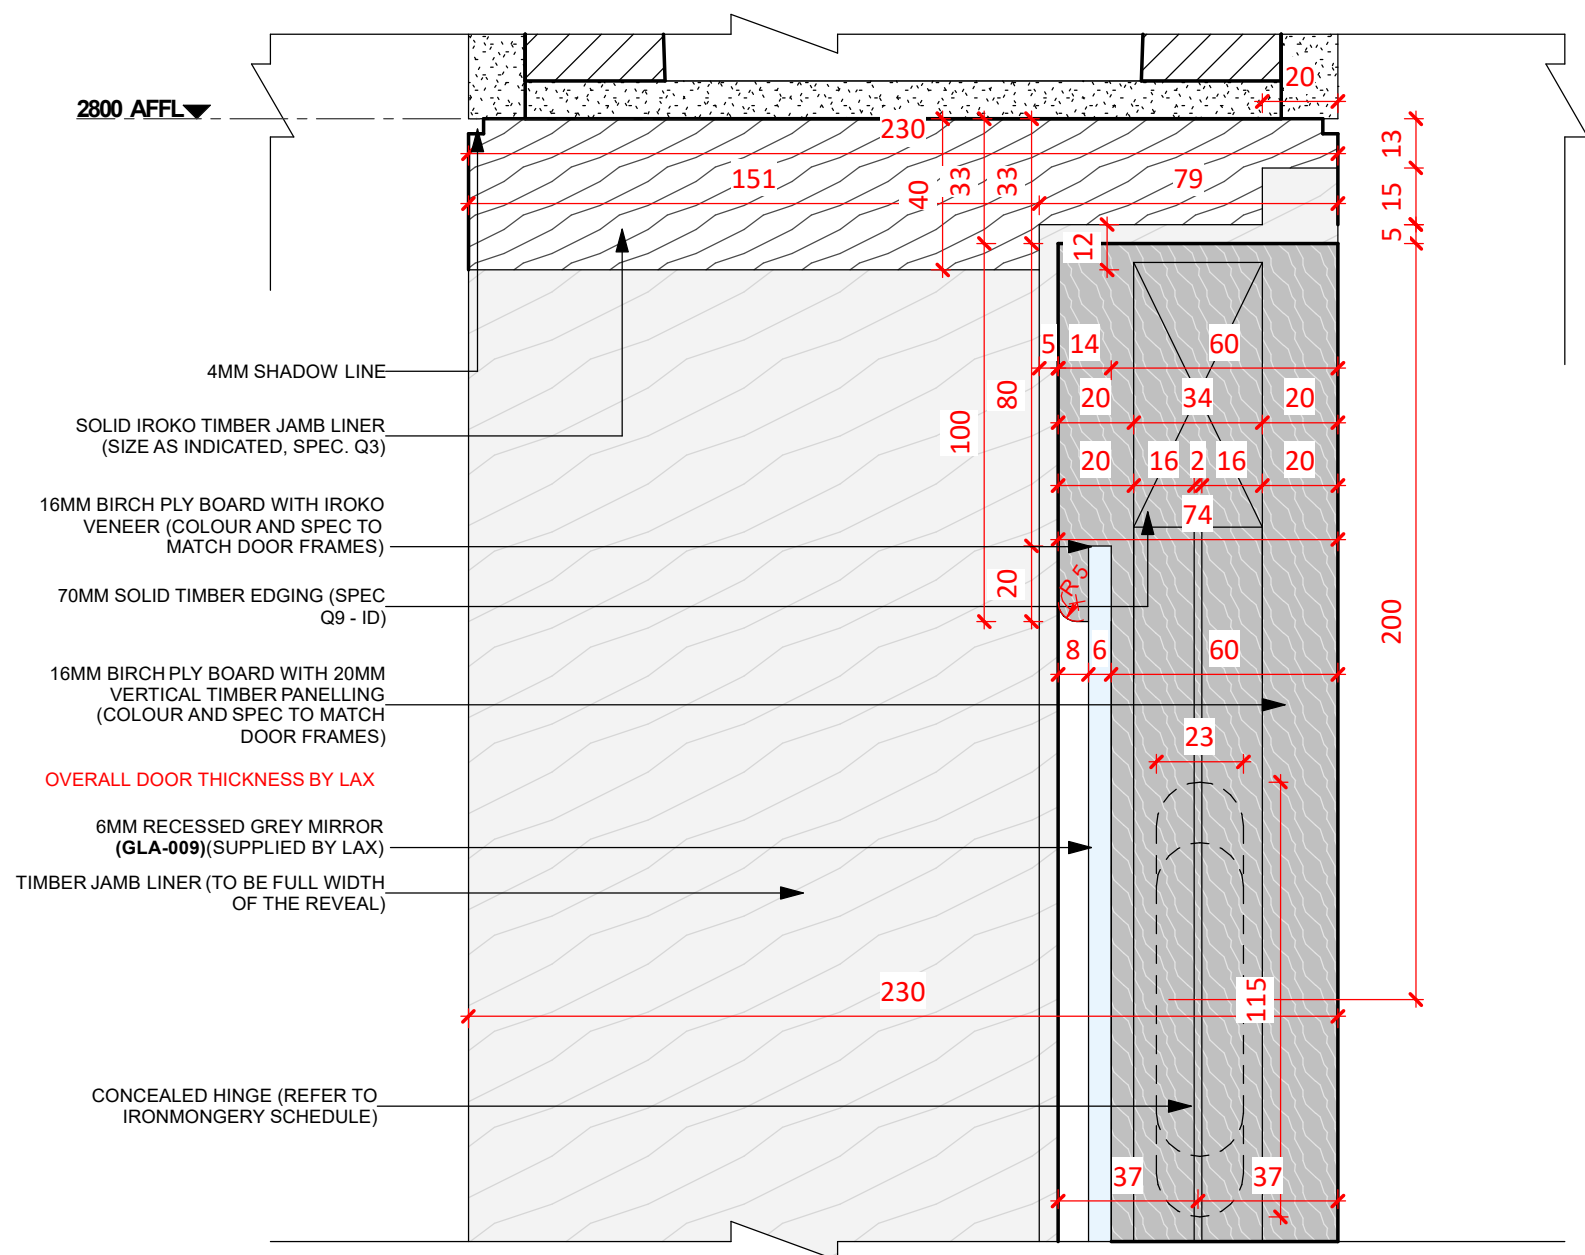

Hinge Door Detail Section - Top of Door | 1:2

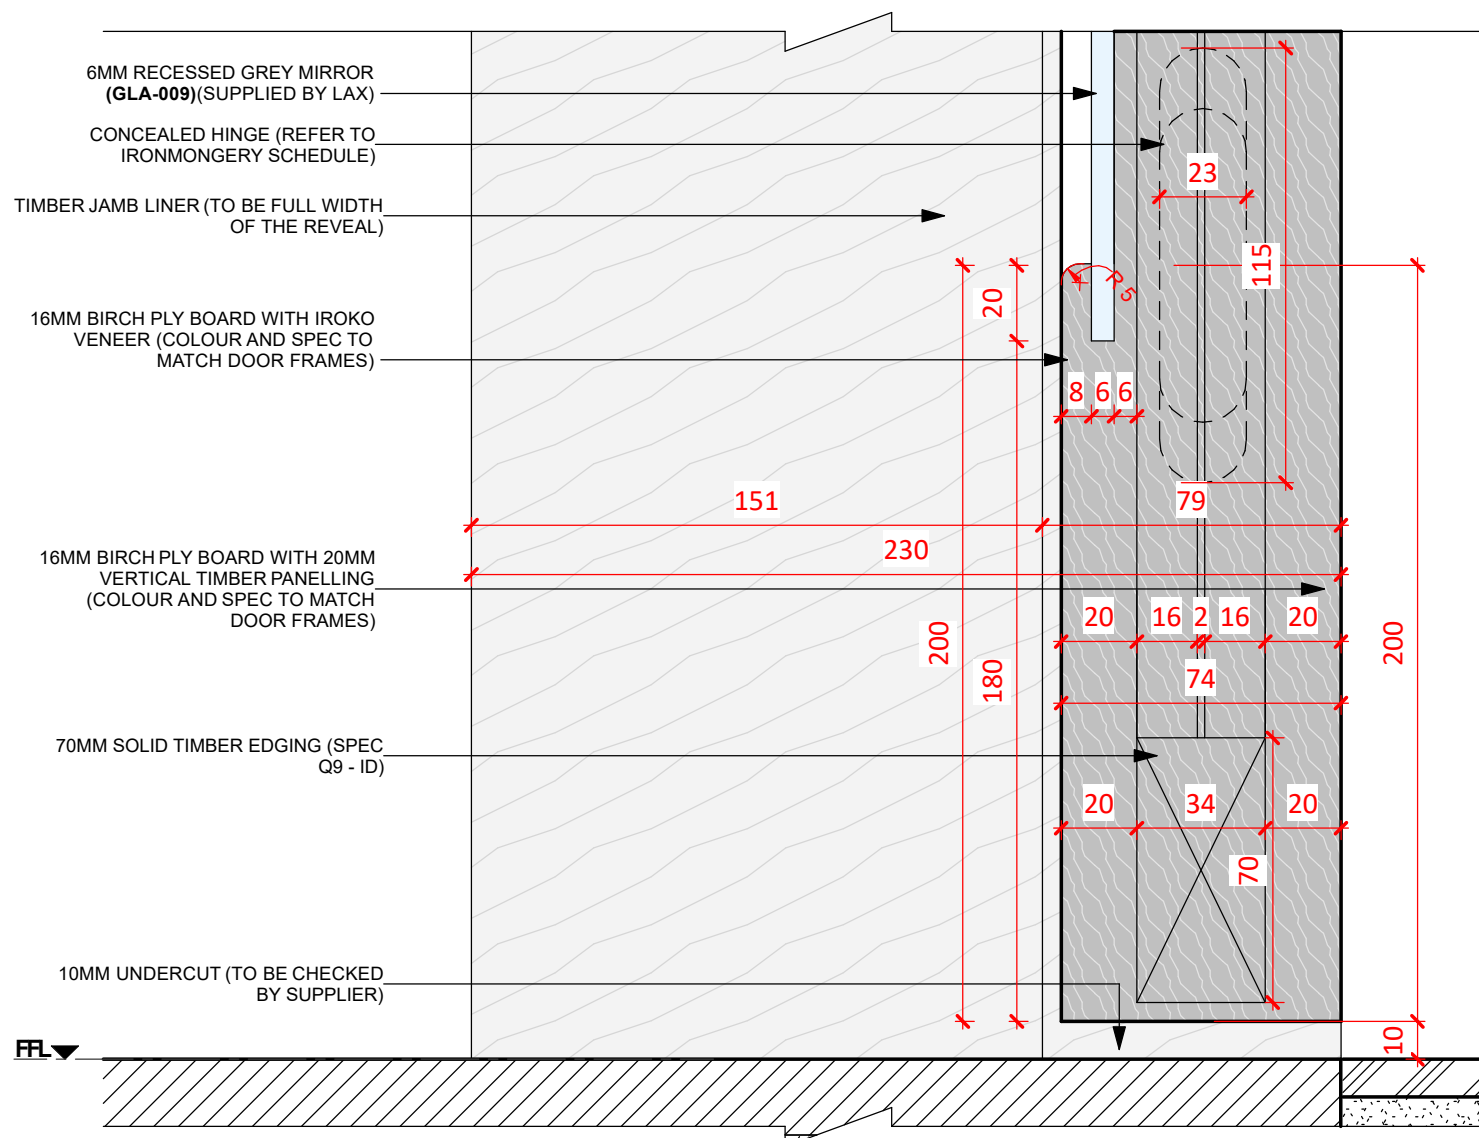

Hinge Door Detail Section - Bottom of Door | 1:2